

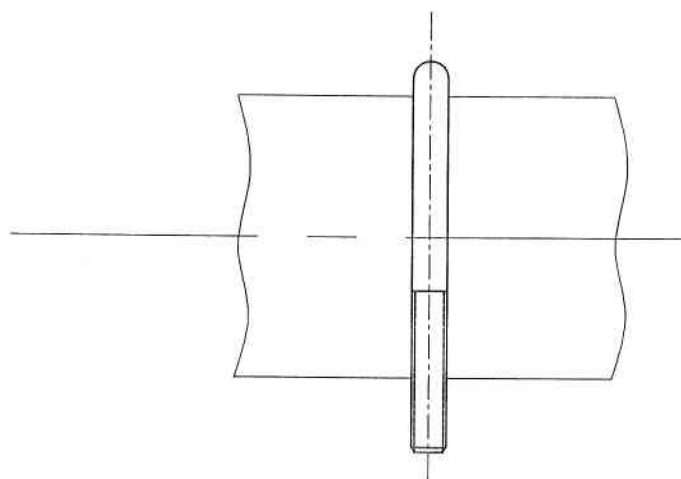


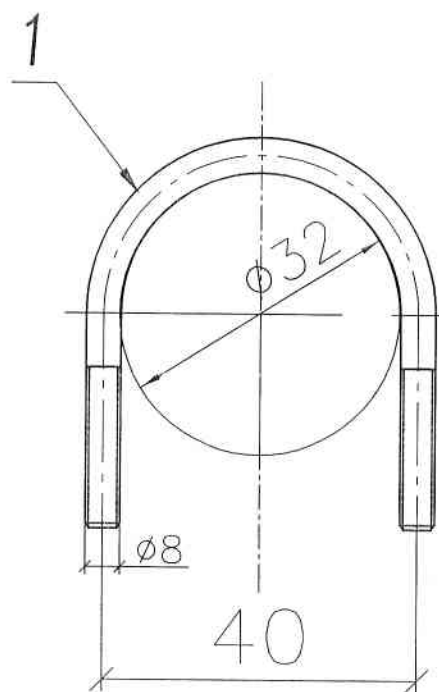

Поз.1

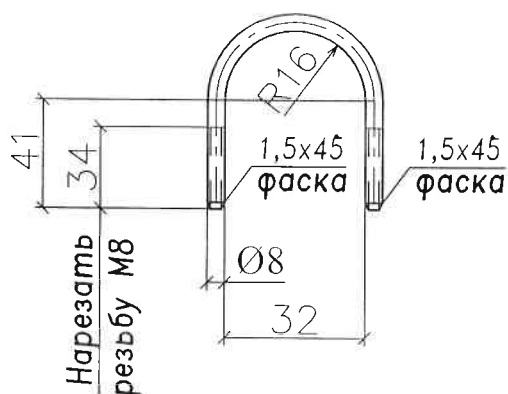

Примечания:

1. Острые кромки притупить.
2. На заводе окрасить грунтом ГФ-021 по ГОСТ 25129-82 в два слоя.
3. Не указанные предельные отклонения размеров по Н14, h14. $\pm IT14/2$.
4. Маркировать контрастной на смываемой краской Х-32

							0,057		
1	1		Кр.Ø8	145	0,057	0,057	0,057		гнуть
	Т.	Н.			ШТ.	ОБЩ.	ЭЛЕМ.	МАРКА	
ДЕТ.	КОЛ.		СЕЧЕНИЕ	ДЛИНА	МАССА В КГ			СТАЛИ	ПРИМЕЧАНИЯ

СПЕЦИФИКАЦИЯ СТАЛИ 09Г2С ГОСТ19281-88

007.ГО.32.Х.000.8112.00

Исполнил						Стадия	Лист	Листов
Проверил						Р	1	1
Рук.груп.	Стахеев							
Гл.конст.								
Гл.техн.								
Гл.инж.	Немиров							
Хомут 32						ООО НПП		
ГОСТ 24137-80						"Строительные технологии"		