

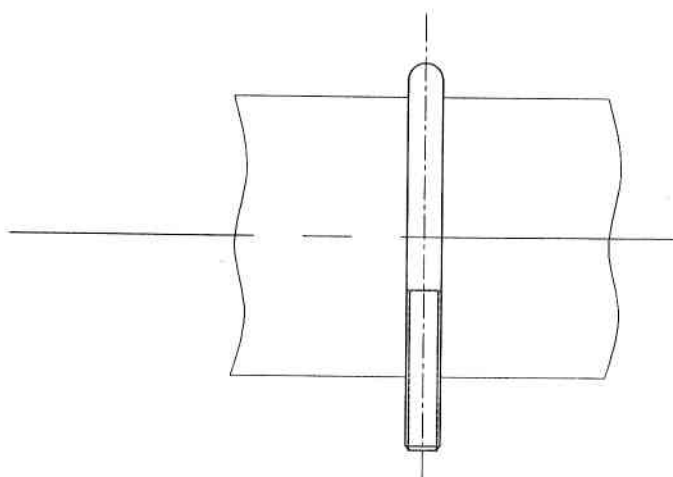


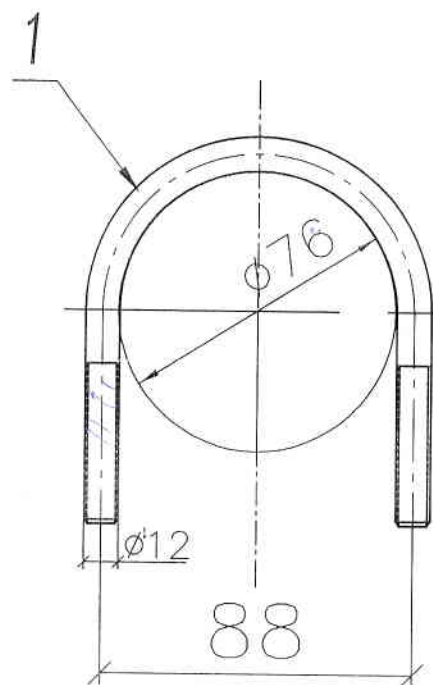

Поз.1

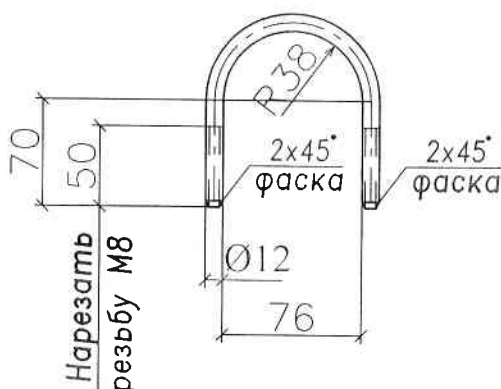

Примечания:

1. Острые кромки притупить.
2. На заводе окрасить грунтом ГФ-021 по ГОСТ 25129-82 в два слоя.
3. Не указанные предельные отклонения размеров по Н14, h14. $\pm IT14/2$.
4. Маркировать контрастной на смываемой краской Х-76

							0,248		
	1	1		Кр.Ø12	279	0,248	0,248		гнуть
		Т.	Н.	СЕЧЕНИЕ	ДЛИНА	ШТ.	ОБЩ.	ЭЛЕМ.	МАРКА СТАЛИ
ДЕТ.	КОЛ.					МАССА В КГ			
									ПРИМЕЧАНИЯ

СПЕЦИФИКАЦИЯ СТАЛИ 09Г2С ГОСТ19281-88

007.ГО.76.Х.000.8121.01

Исполнил									
Проверил									
Рук.груп.	Стахеев								
Гл.конст.									
Гл.техн.									
Гл.инж.	Немиров								
Хомут 76 по туну ГОСТ 24137-80						Стадия	Лист	Листов	
						Р	1	1	
						ООО НПП "Строительные технологии"			