


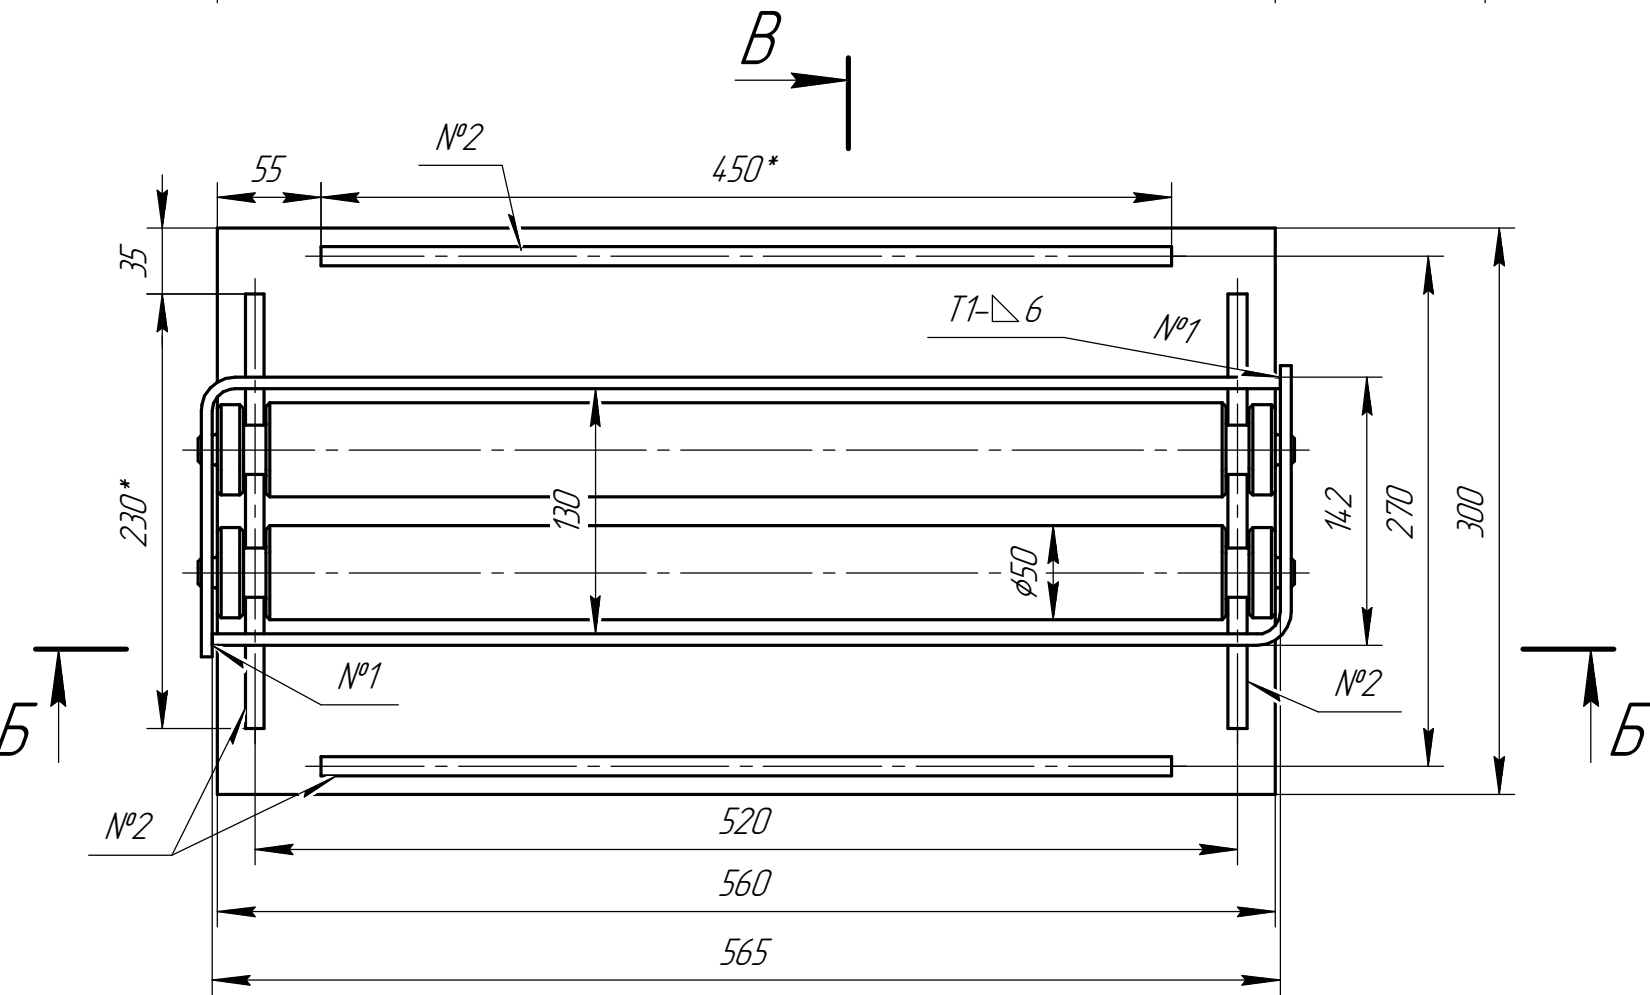
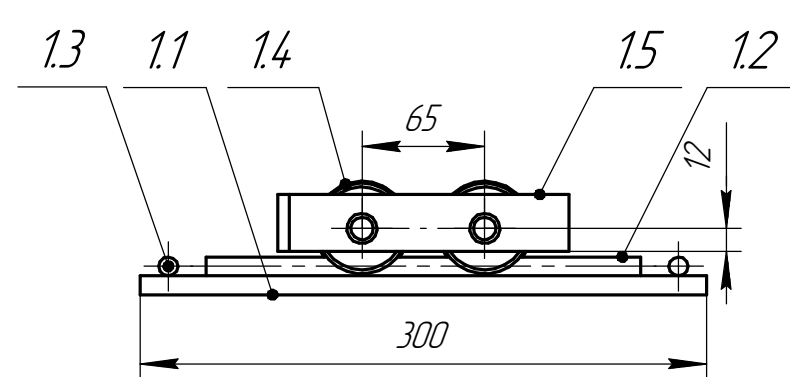
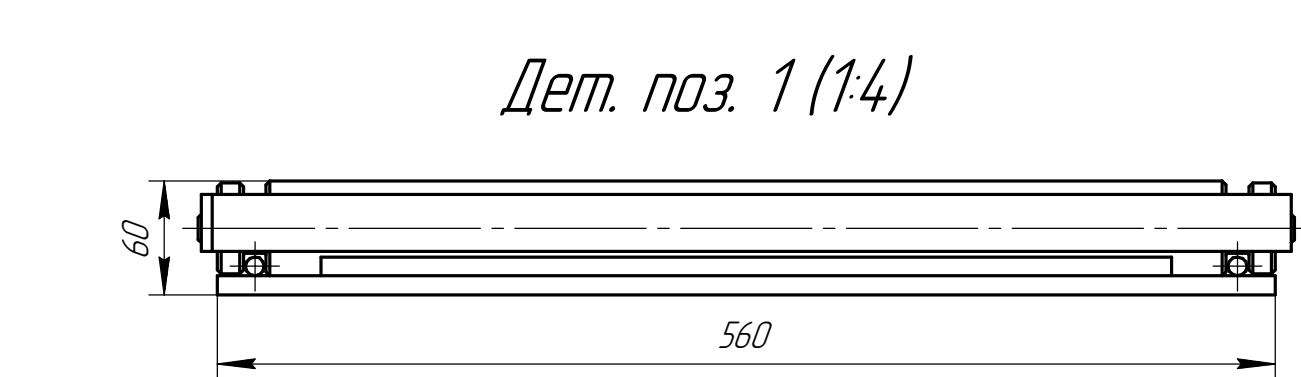
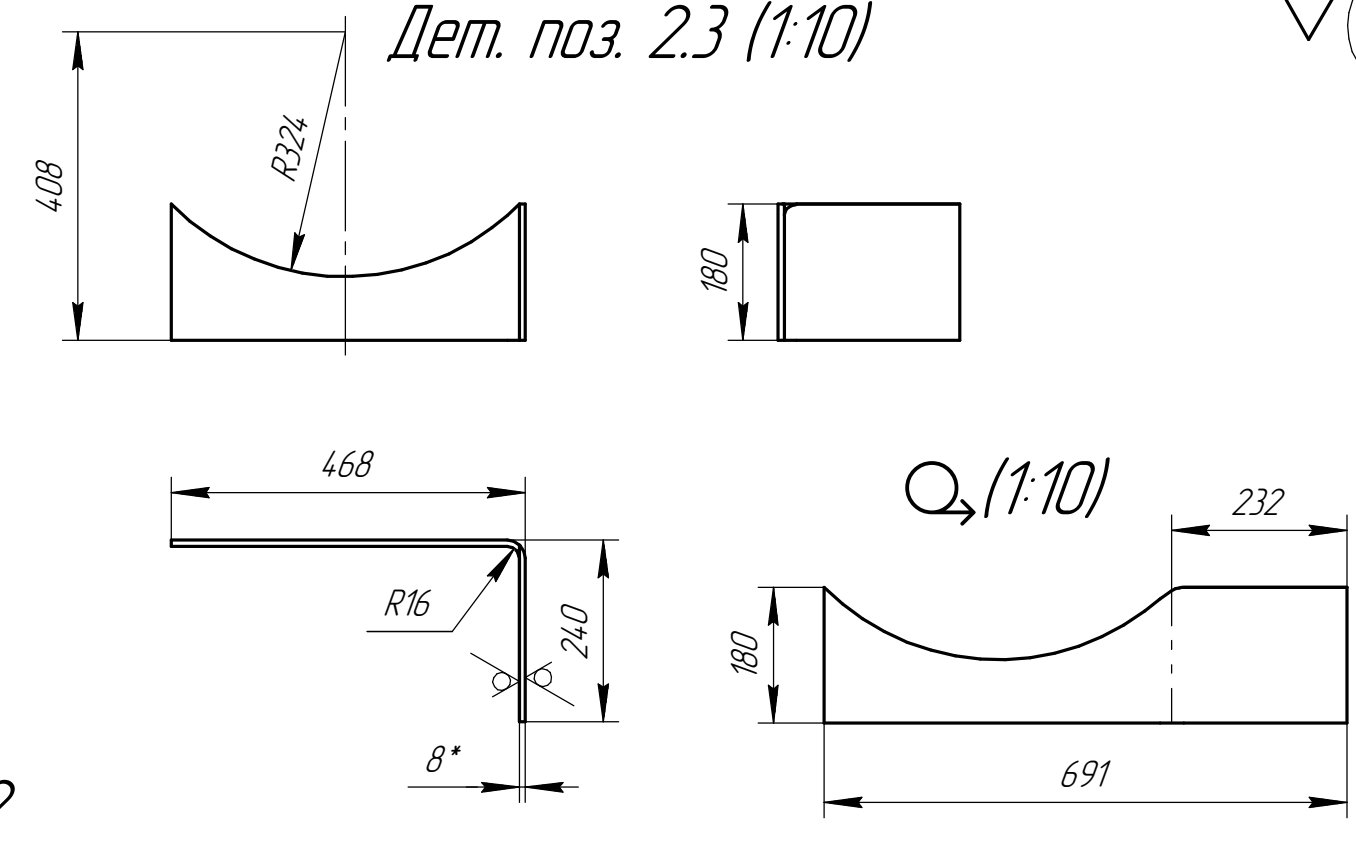
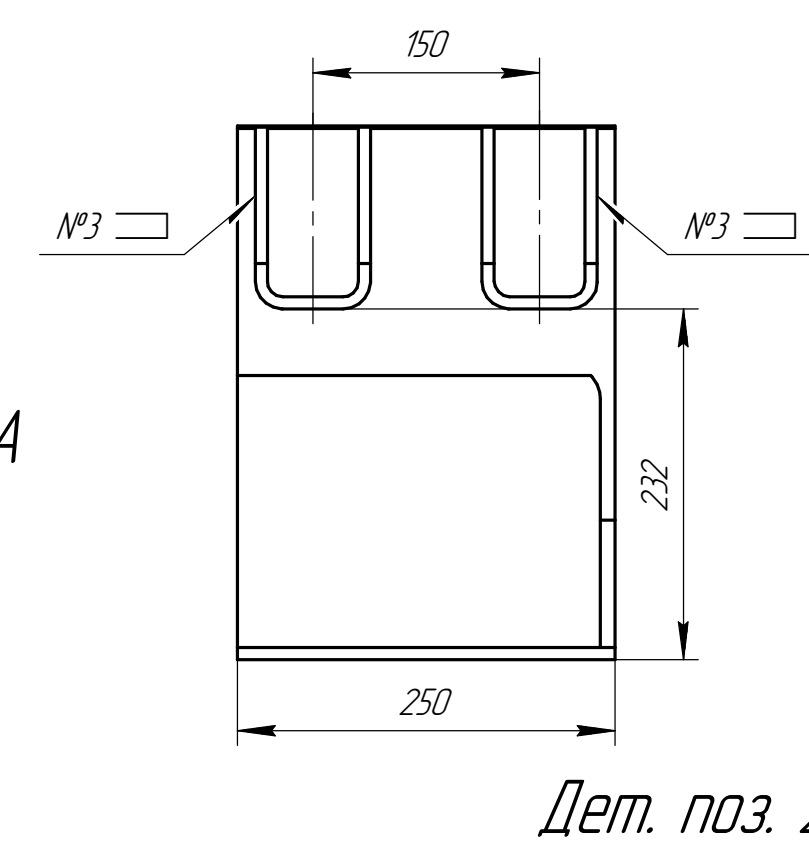
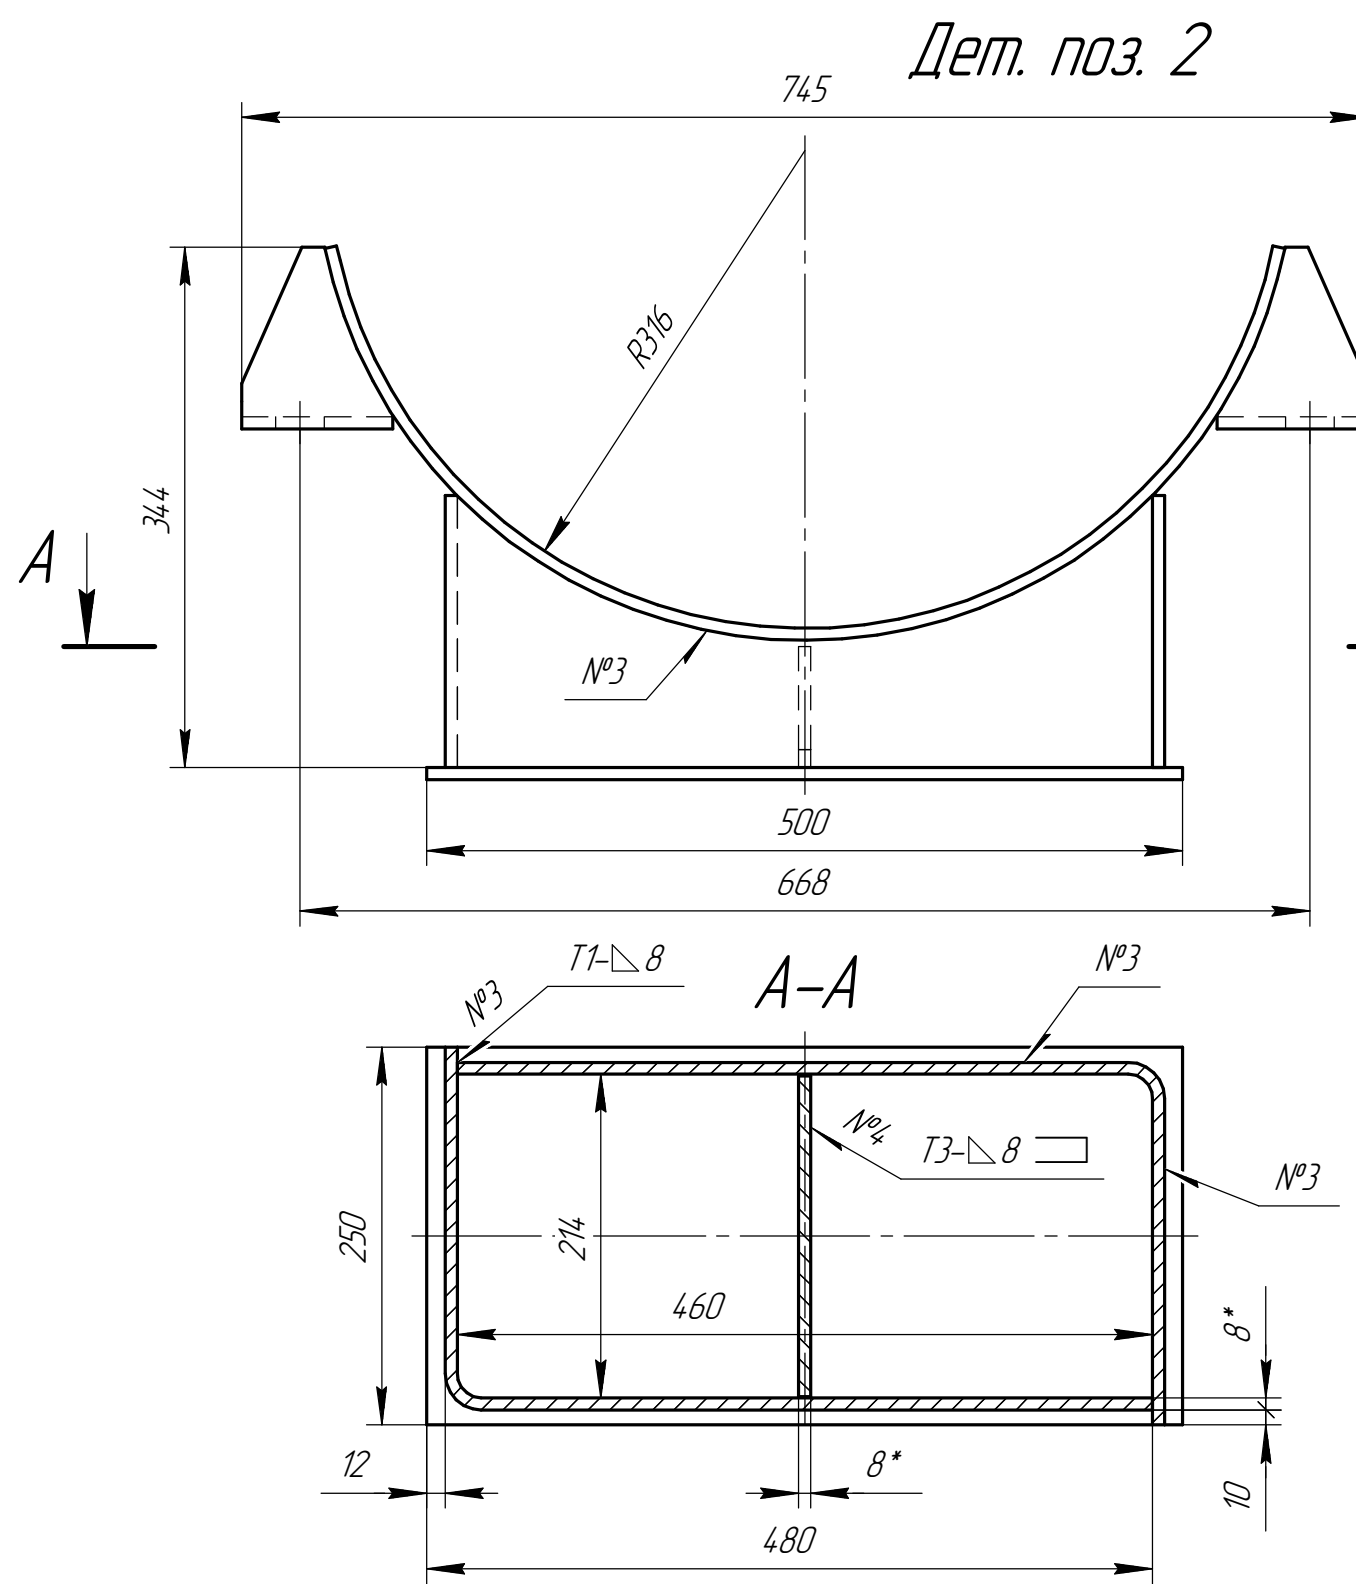
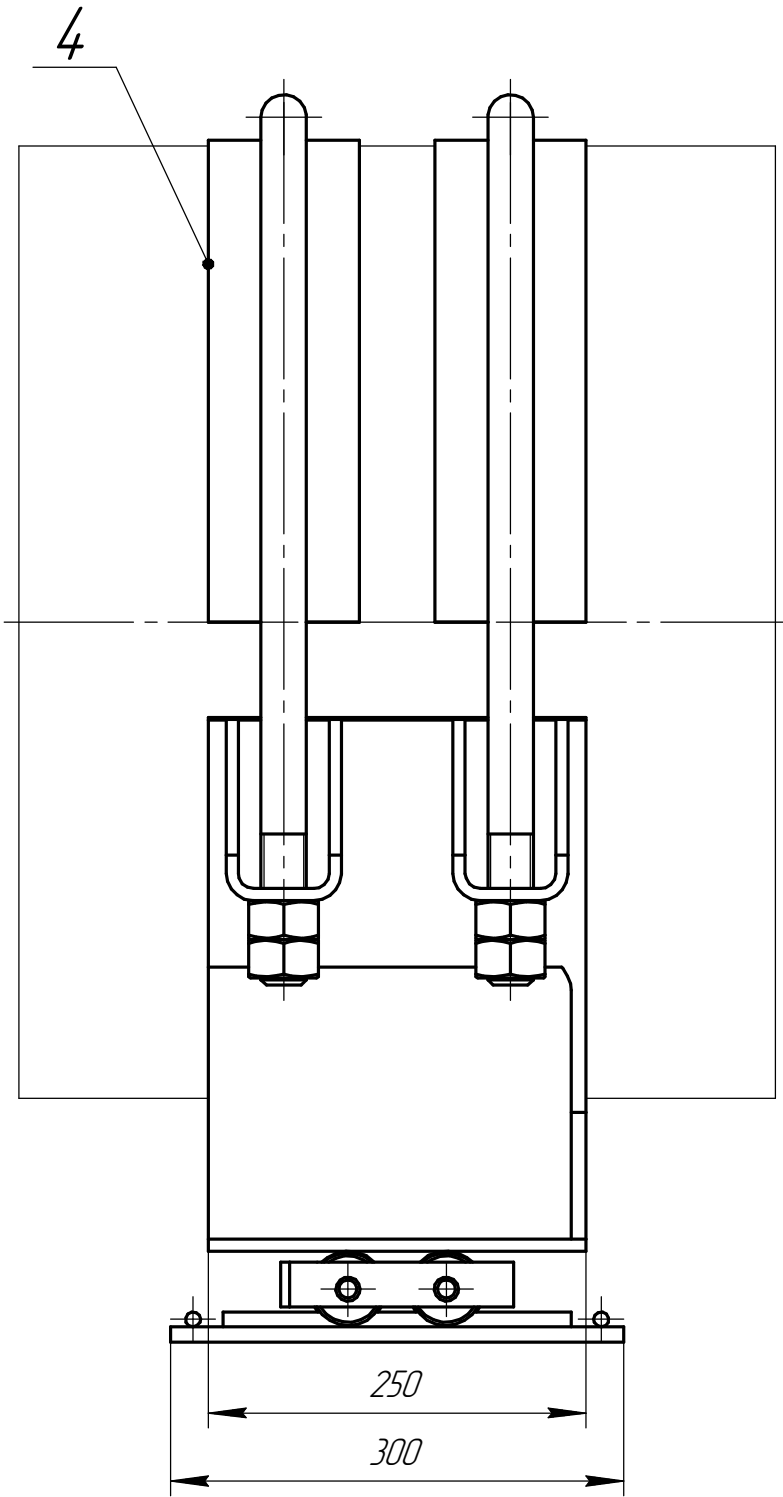


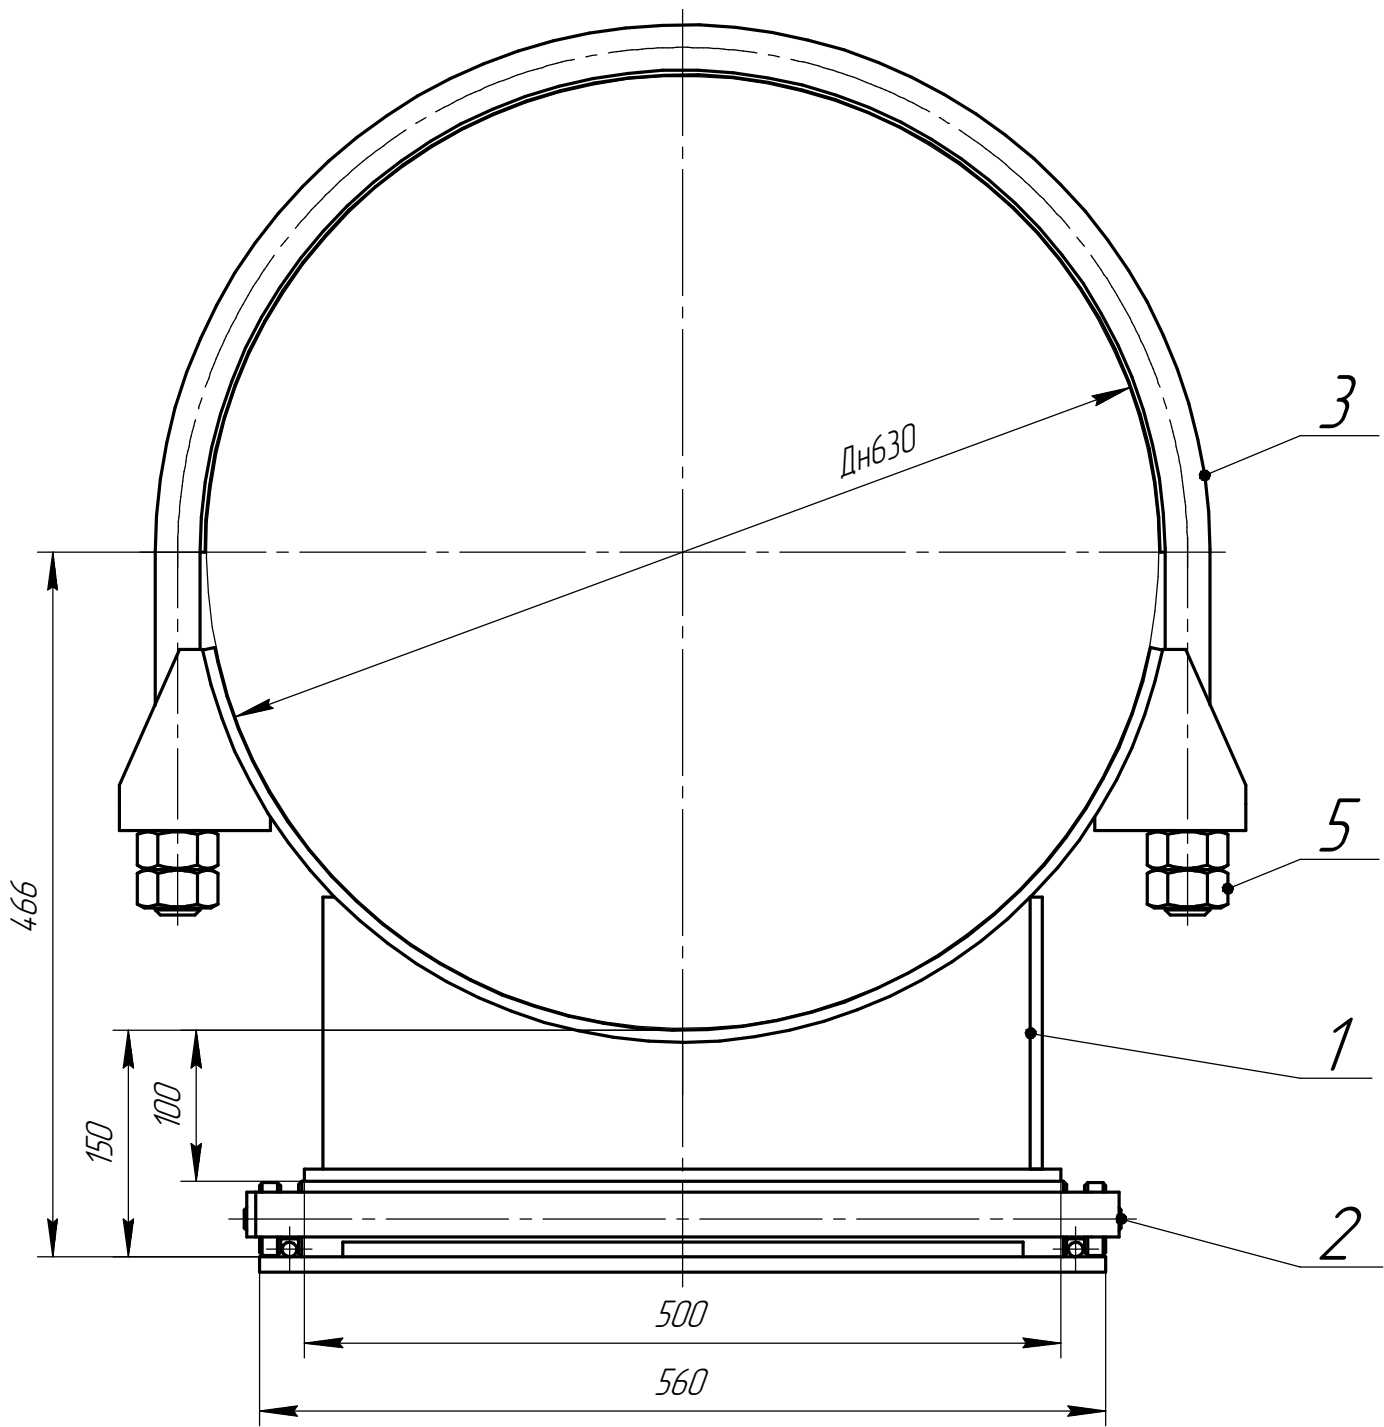


Det. poz. 1 (1:4)

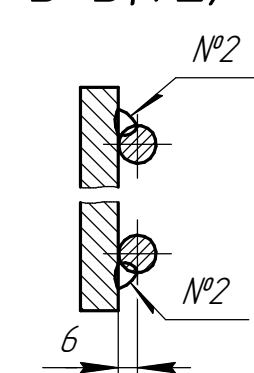


Det. poz. 1 (1:4)

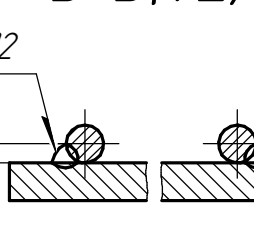


Det. poz. 1 (1:4)

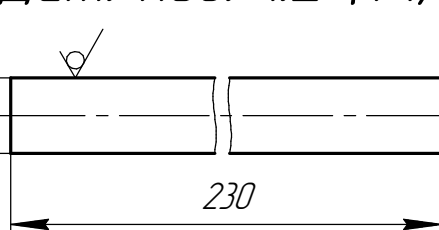

Det. poz. 1 (1:4)

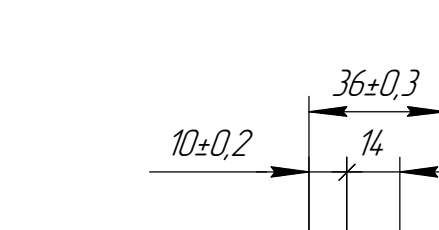


Det. poz. 1 (1:4)

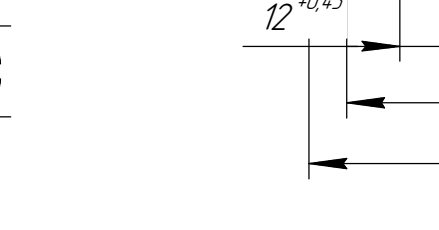


Det. poz. 1 (1:4)


Det. poz. 1 (1:4)

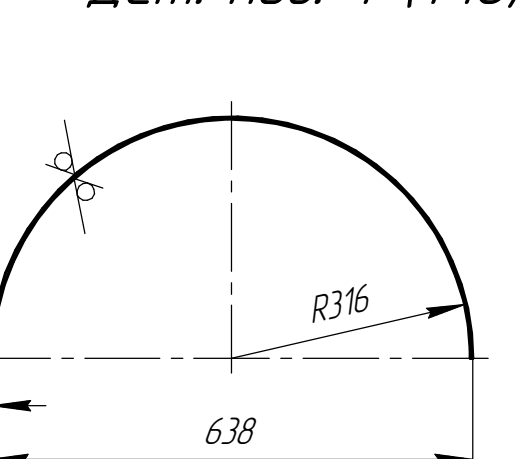


Det. poz. 1 (1:4)

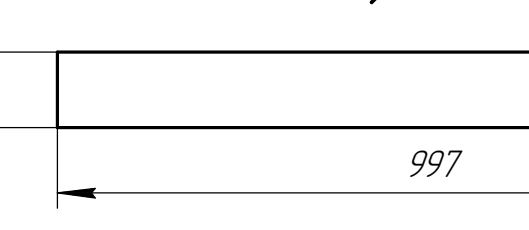


Det. poz. 1 (1:4)

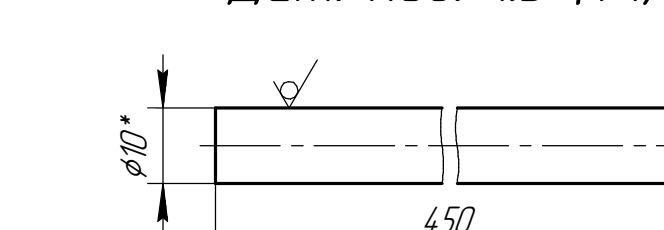

Det. poz. 1 (1:4)


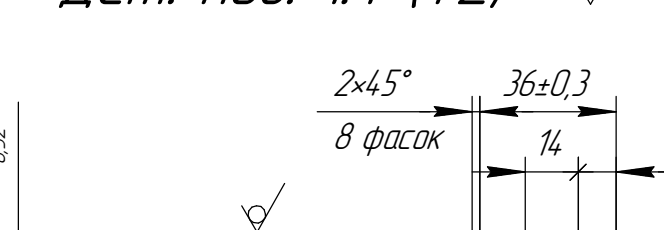


Det. poz. 1 (1:4)

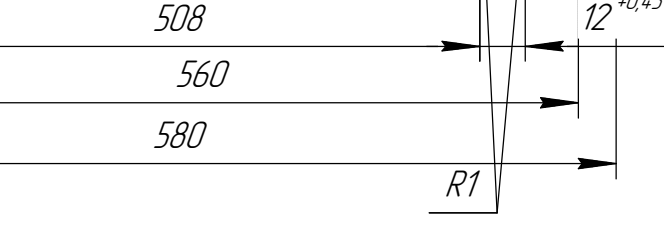


Det. poz. 1 (1:4)

Det. poz. 2

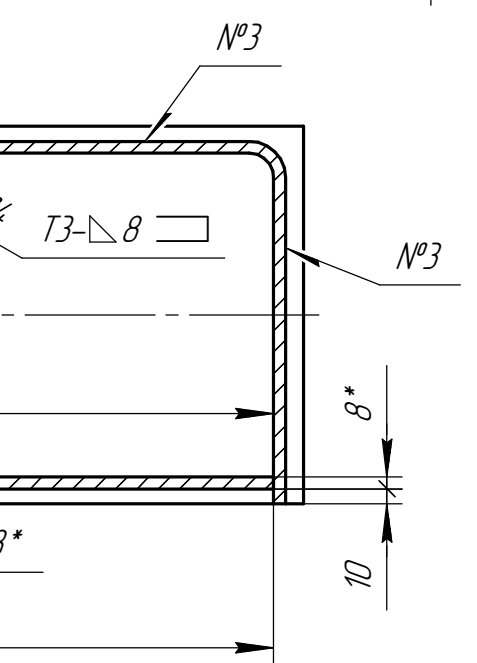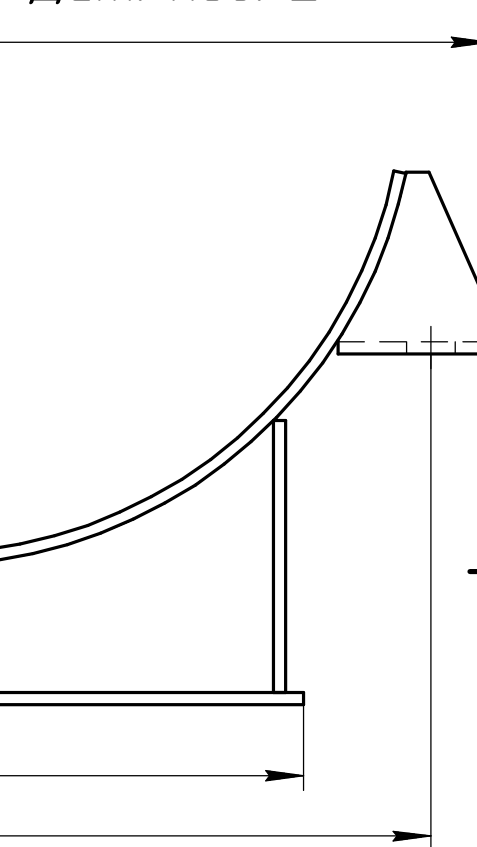

Det. poz. 2

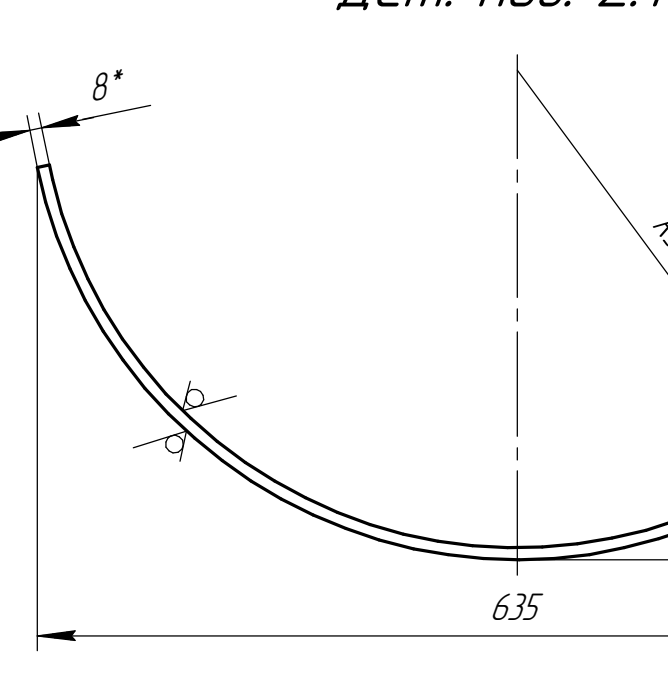


Det. poz. 2




Det. poz. 2



Det. poz. 2

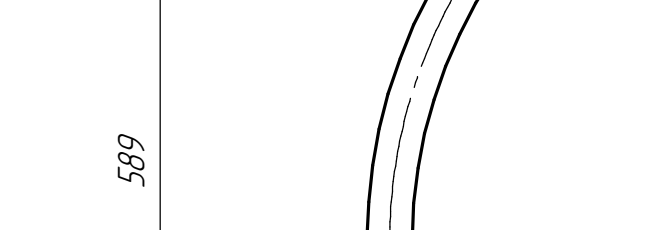


Det. poz. 2

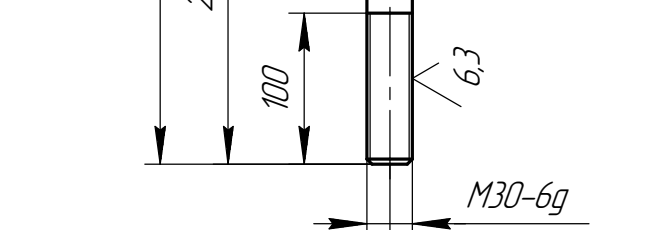


Det. poz. 2

Det. poz. 2

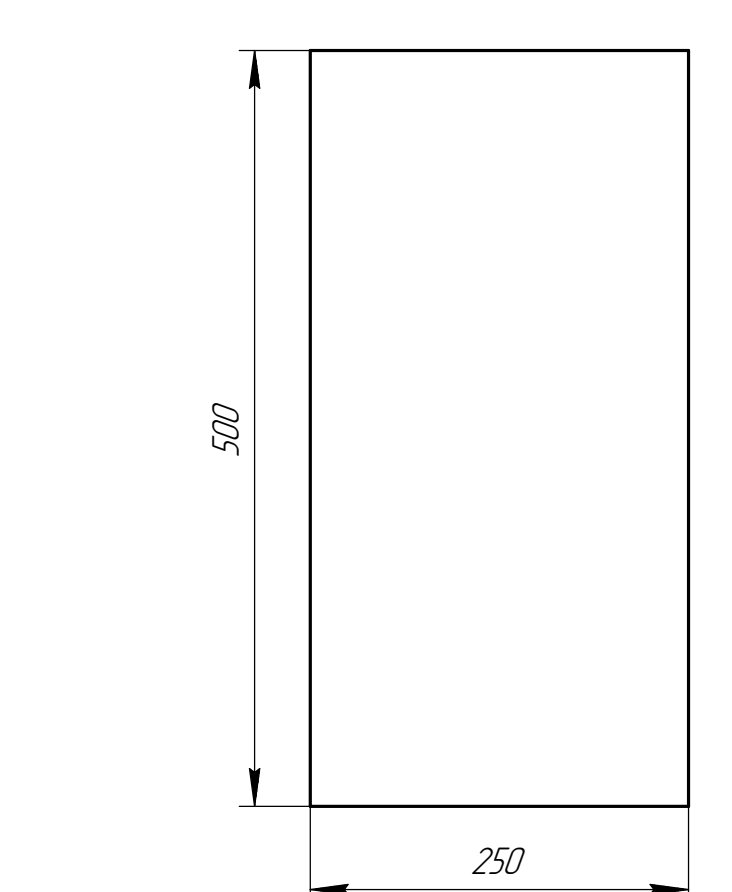

Det. poz. 2

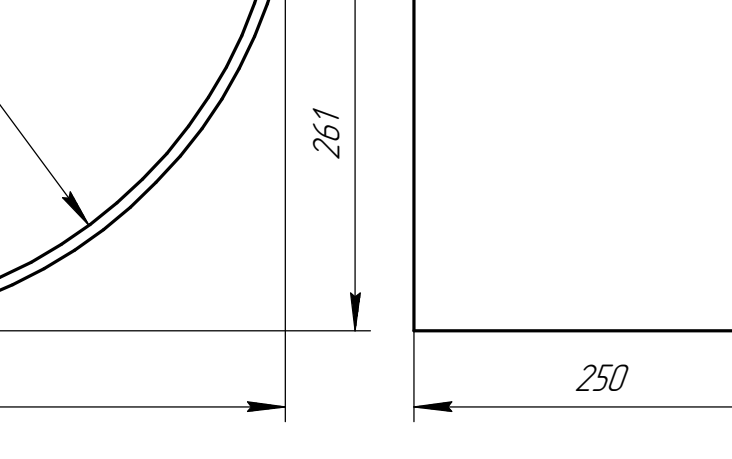


Det. poz. 2



Det. poz. 2



Det. poz. 2

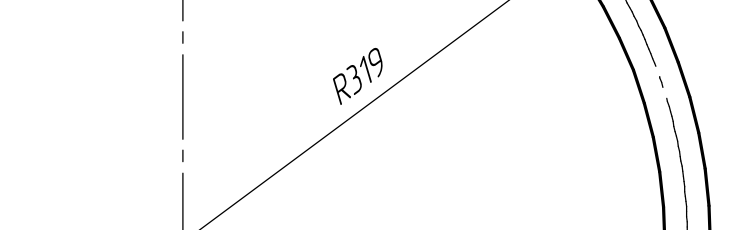


Det. poz. 2




Det. poz. 2


Det. poz. 2.3 (1:10)

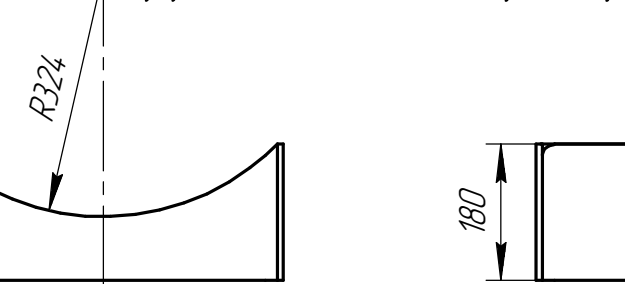


Det. poz. 2.3 (1:10)

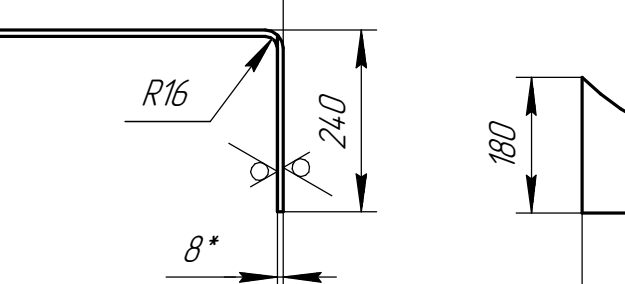


Det. poz. 2.3 (1:10)

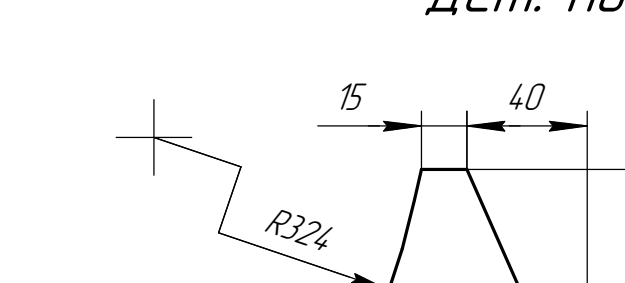


Det. poz. 2.3 (1:10)

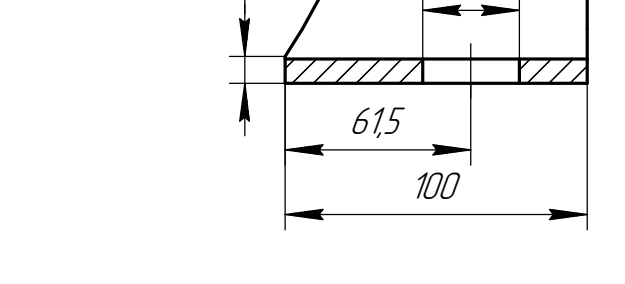


Det. poz. 2.3 (1:10)

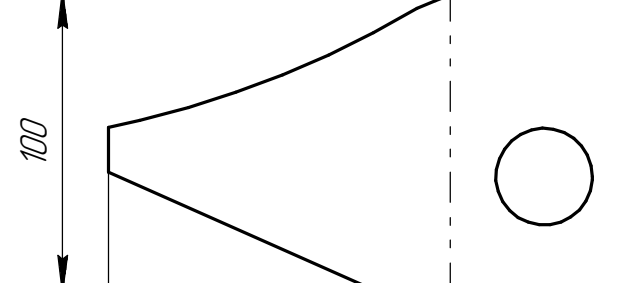


Det. poz. 2.3 (1:10)

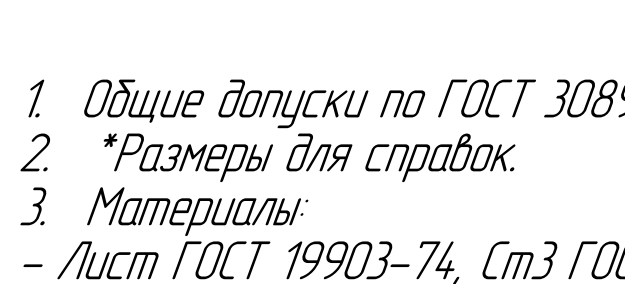


Det. poz. 2.3 (1:10)

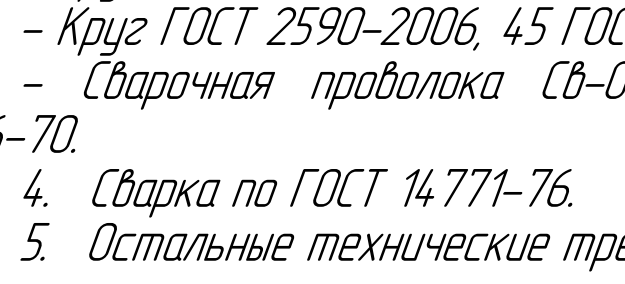


Det. poz. 2.3 (1:10)

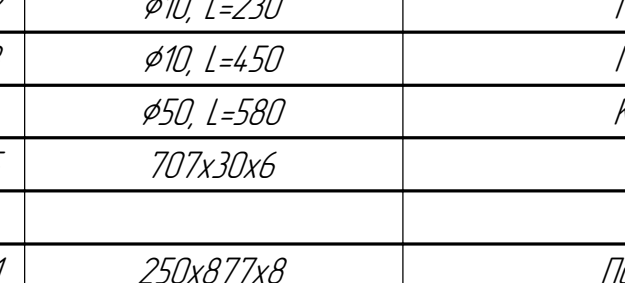


Det. poz. 2.3 (1:10)

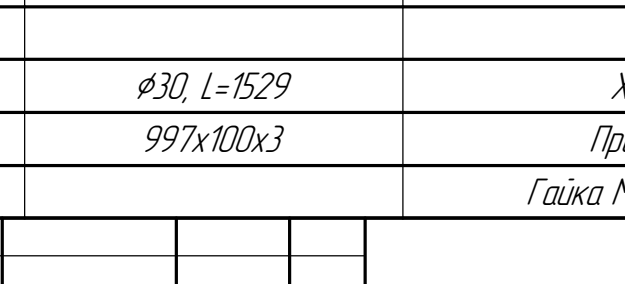


Det. poz. 2.3 (1:10)

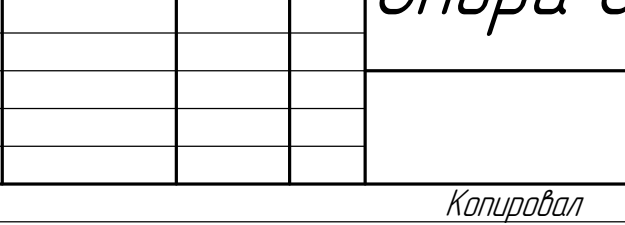


Det. poz. 2.4 (1:2,5)

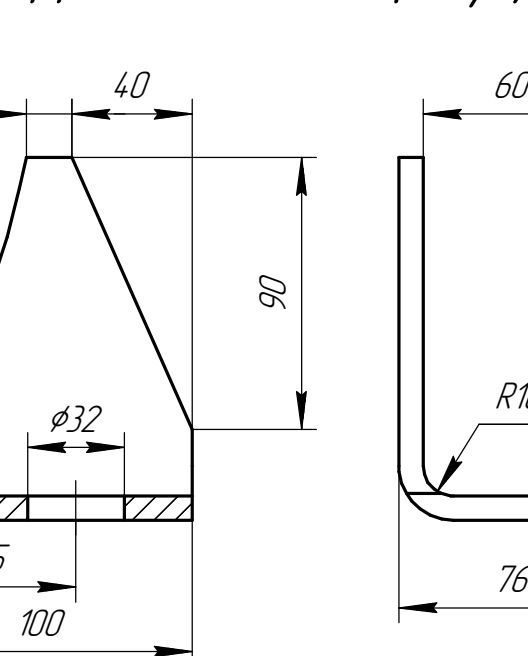

Det. poz. 2.4 (1:2,5)

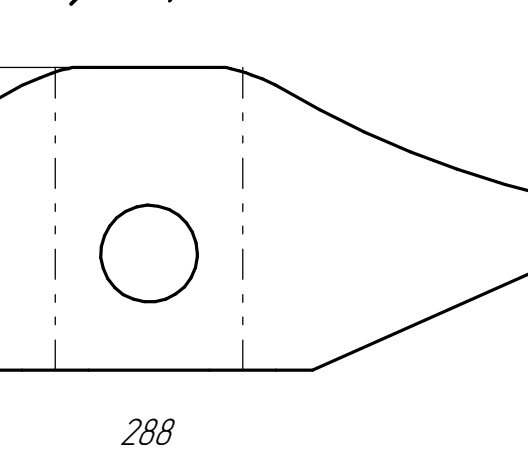


Det. poz. 2.4 (1:2,5)

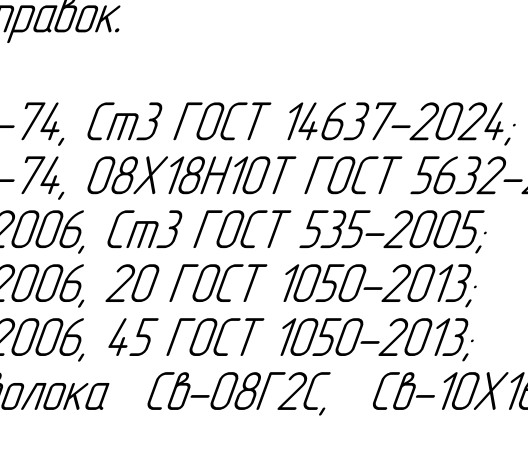


Det. poz. 2.4 (1:2,5)



Det. poz. 2.4 (1:2,5)

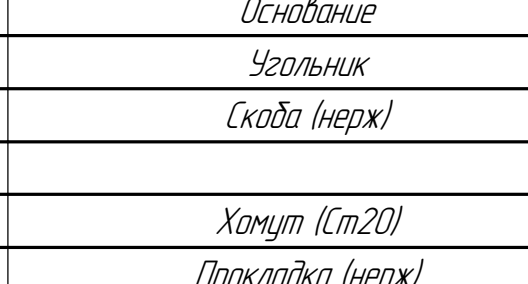

Det. poz. 2.4 (1:2,5)

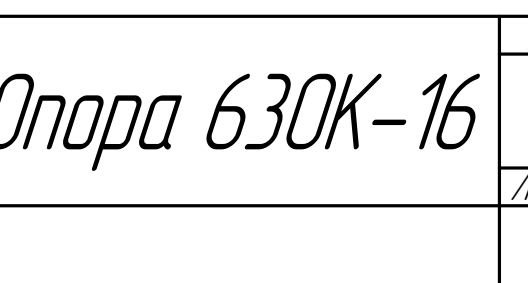

Det. poz. 2.4 (1:2,5)

- Общие допуски по ГОСТ 30893.1: Н17, h17, ±IT17/2.
- *Размеры для справок.
- Материалы:
 - Лист ГОСТ 19903-74, Ст3 ГОСТ 14637-2024;
 - Лист ГОСТ 19903-74, 08Х18Н10Т ГОСТ 5632-2014;
 - Круг ГОСТ 2590-2006, Ст3 ГОСТ 535-2005;
 - Круг ГОСТ 2590-2006, 20 ГОСТ 1050-2013;
 - Круг ГОСТ 2590-2006, 45 ГОСТ 1050-2013;
 - Сварочная проволока СВ-08Г2С, СВ-10Х16Н25АМ6 ГОСТ 2246-70.
- Сварка по ГОСТ 14771-76.
- Остальные технические требования по ОСТ 34-10-617.

Поз.	Обозначение	Наименование	Кол.	Прим.
1.1	560х300х10	Основание	1	13,19 кг
1.2	φ10, L=230	Пруток (Ст3)	2	0,14 кг
1.3	φ10, L=450	Пруток (Ст3)	2	0,28 кг
1.4	φ50, L=580	Каток (Ст45)	2	8,34 кг
1.5	707х30х6	Угольник	2	0,98 кг
2.1	250х877х8	Подушка (нерж.)	1	13,78 кг
2.2	250х500х8	Основание	1	7,85 кг
2.3	691х180х8	Угольник	2	5,91 кг
2.4	288х100х8	Скоба (нерж.)	4	1,16 кг
3	φ30, L=1529	Хомут (Ст20)	2	8,49 кг
4	997х100х3	Прокладка (нерж.)	2	2,35 кг
5		Гайка М30.8 ГОСТ 5915-70	8	0,243 кг
ОСТ 34-10-619				
Опора 630К-16				
Изм.	Лист	№ док.	Подп.	Дата
Разраб.				
Проб.				
Т.контр.				
Н.контр.				
Утв.				
Лит.			Масса	Масштаб
			95,44	15
Лист			Листов	1