

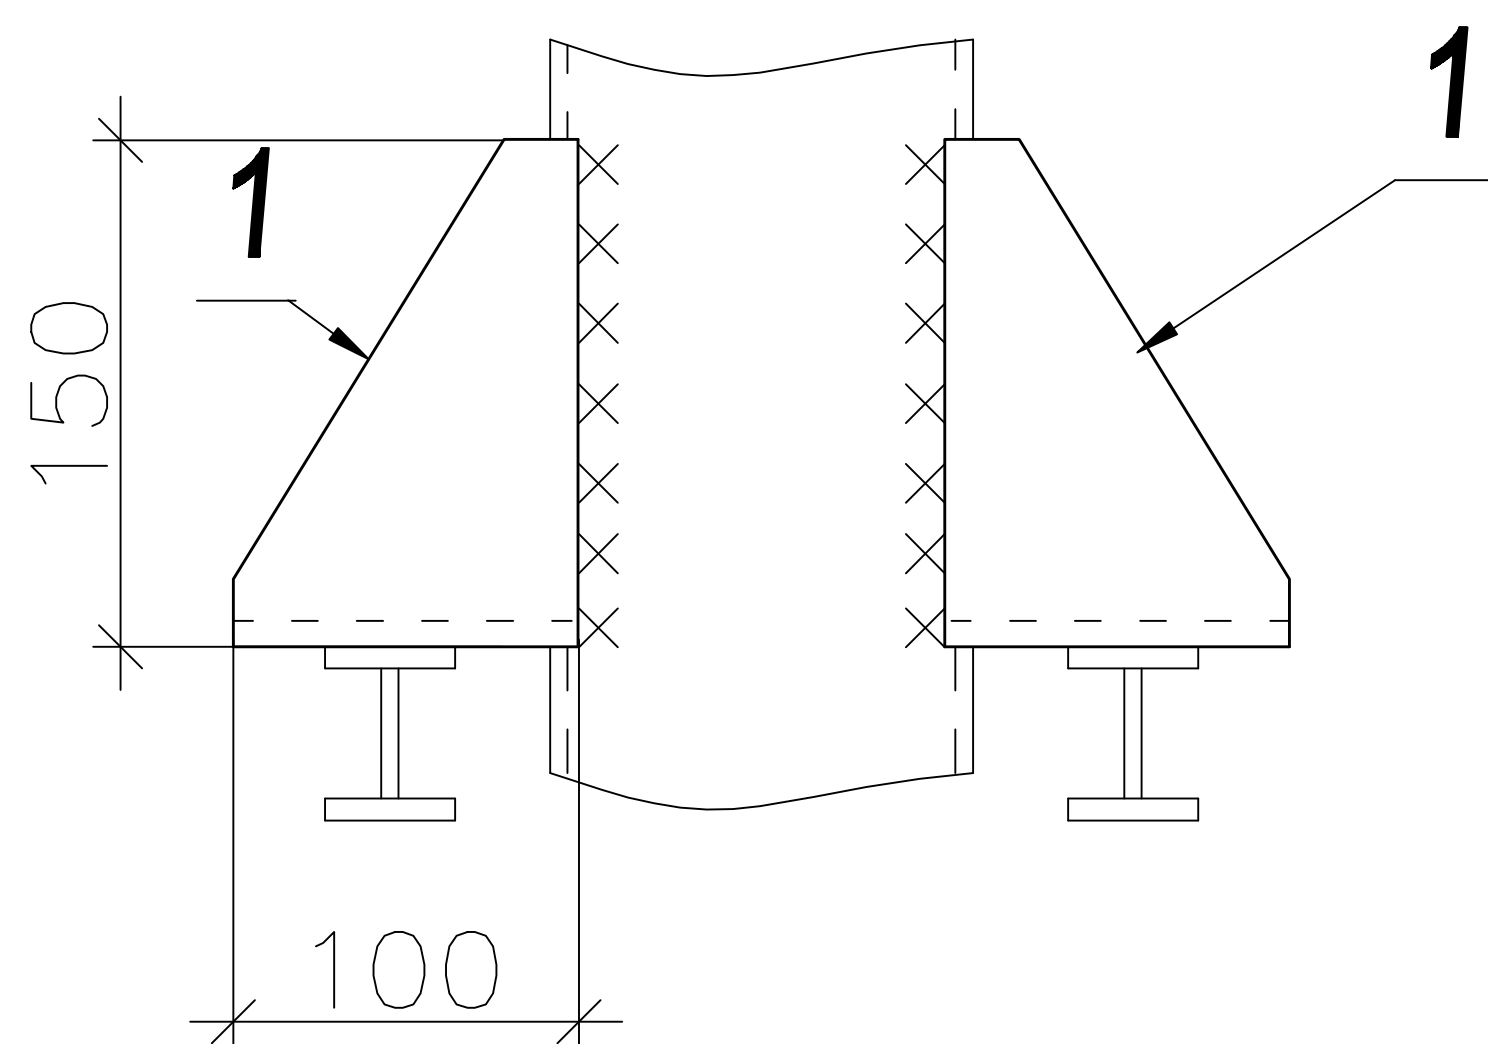


159-ВП-А1

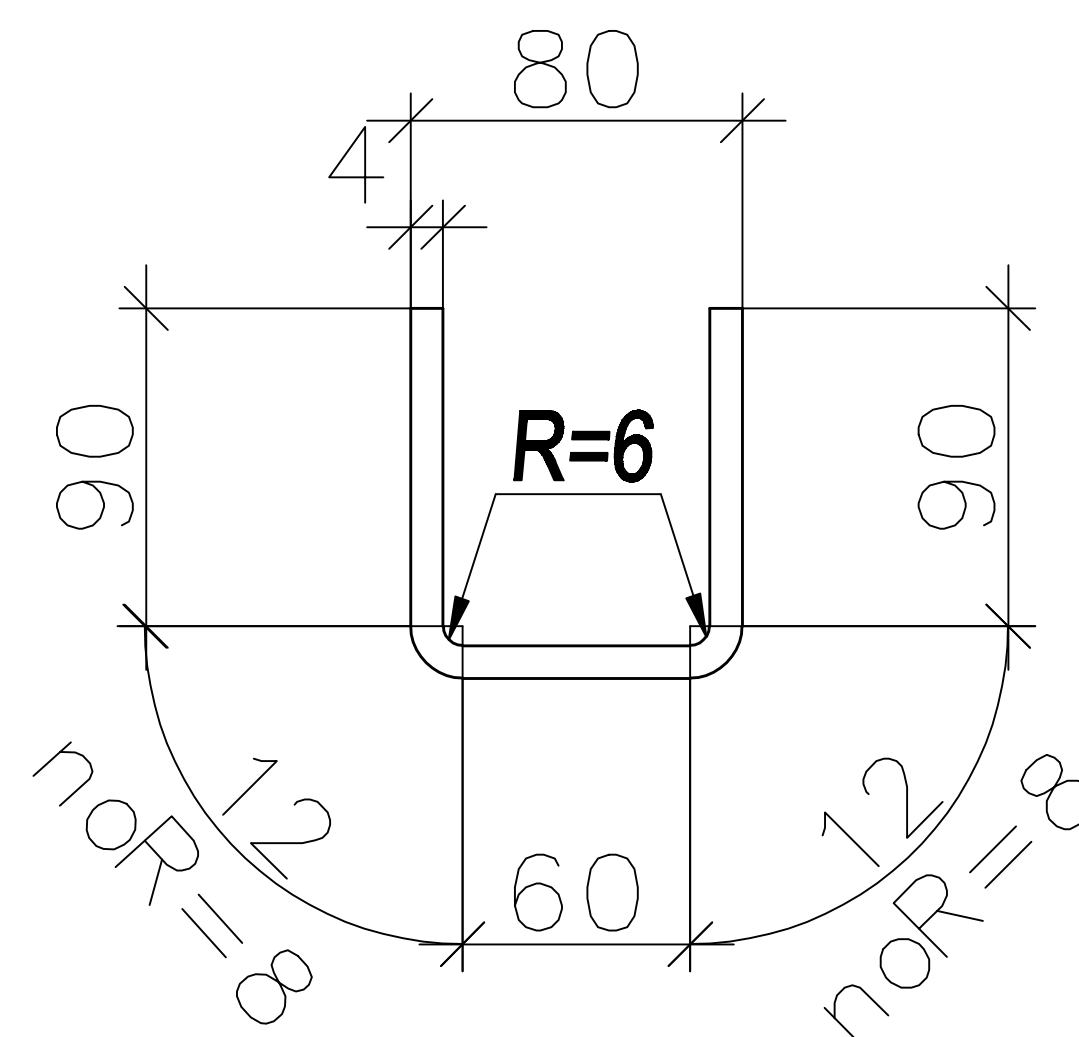

Развертка поз.1

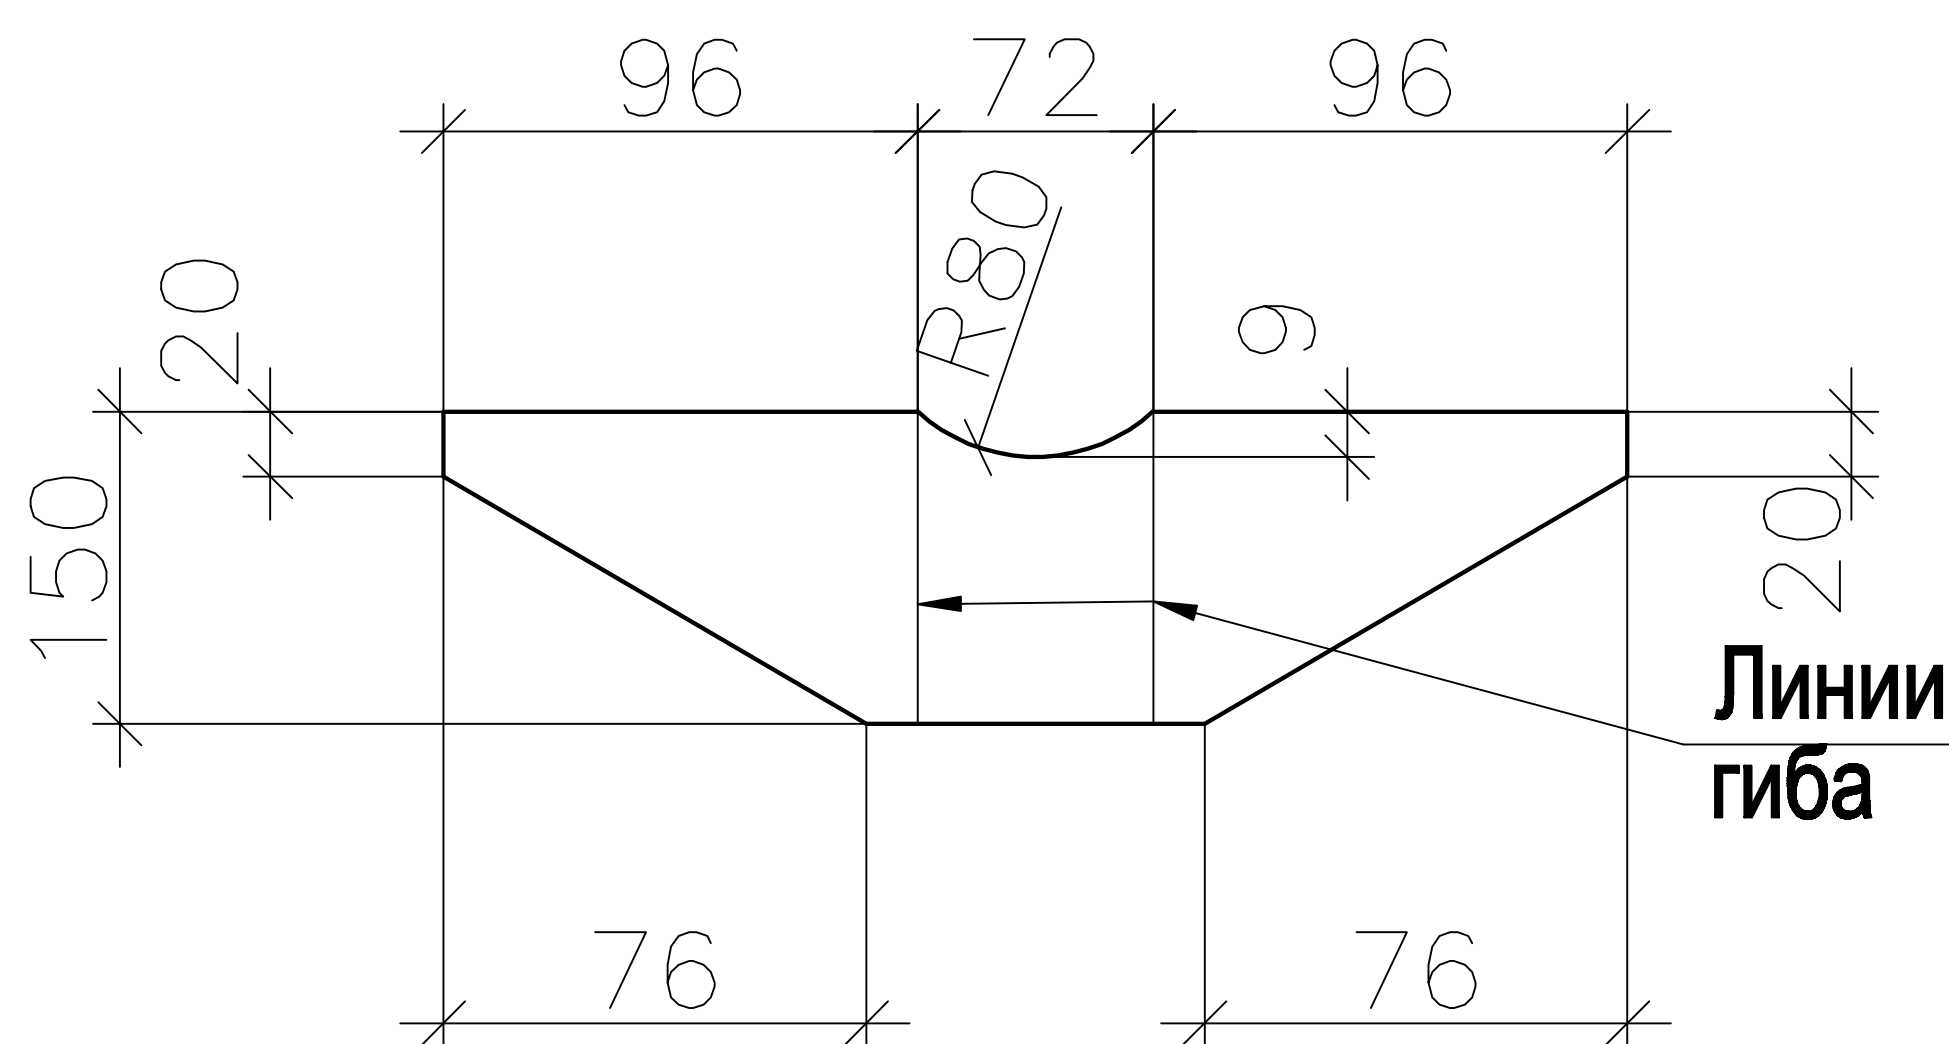

Выборка металла

Материал		Сечение	Масса в кг	ГОСТ
ГОСТ 19281-89	09Г2С	лист 4	2,48	19903-74
Итого			2,48	кг

Поз.1

Примечания:

1. На заводе окрасить грунтом ГФ-021 по ГОСТ 25129-82 в два слоя.
2. Значения предельных отклонений размеров по Н14, h14, ±IT14/2.
3. Острые кромки притупить радиусом 0,5 мм.
4. Опору маркировать 159-ВП-А1.

								1,8		
	1	2		- 150 x 4	264	0,9	1,8			ф.л.гнуть
ОТПР.		Т.	Н.			ШТ.	ОБЩ.	ЭЛЕМ.	МАРКА	
ЭЛЕМ.	ДЕТ.	КОЛ-ВО		СЕЧЕНИЕ	ДЛИНА	МАССА В КГ			СТАЛИ	ПРИМЕЧАНИЯ

СПЕЦИФИКАЦИЯ СТАЛИ 09Г2С ГОСТ 19281-89

007.OC.159.ВП.000.1236.00

Исполнил				Опора 159-ВП-А1	Стадия	Лист	Листов
Проверил					Р	1	1
Рук.груп.							
Гл.конст.				ОСТ 36-146-88	ООО НПП "Строительные технологии"		
Гл.техн.							
Гл.инж.	Немиров						