


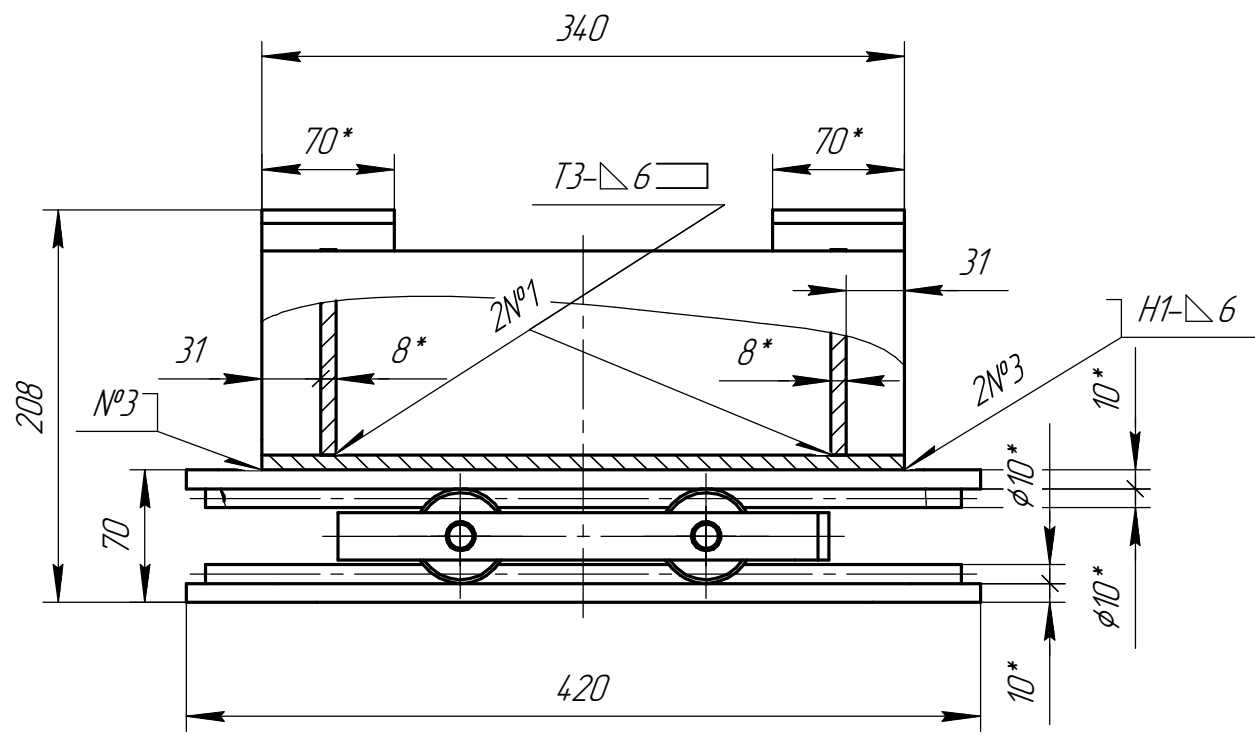


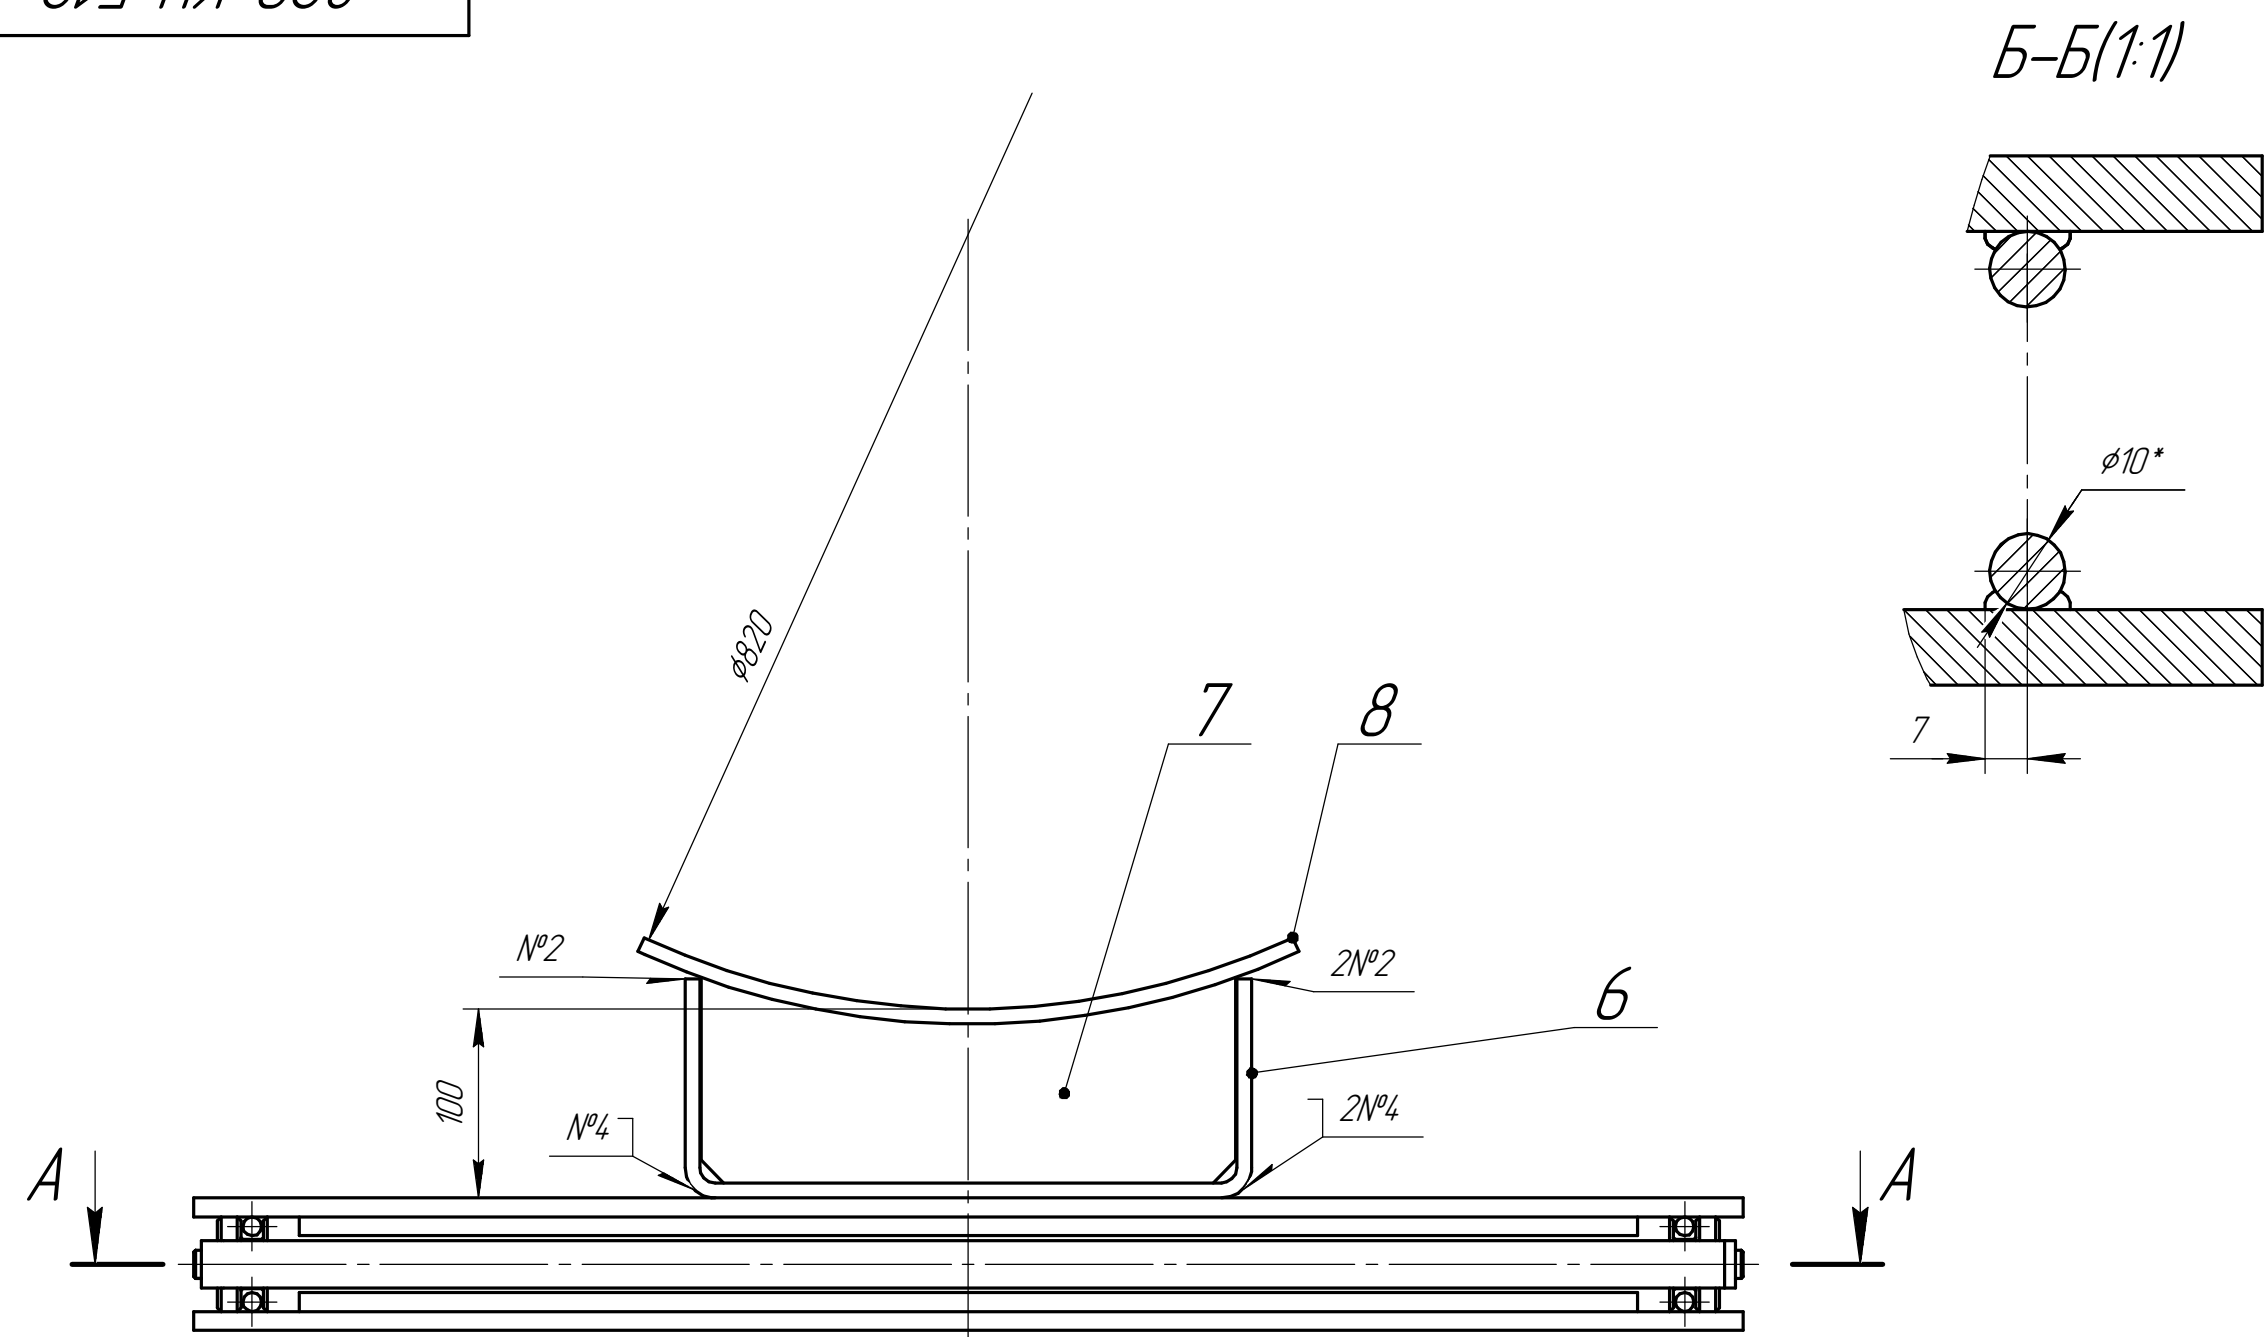


Q₃(1:2,5)

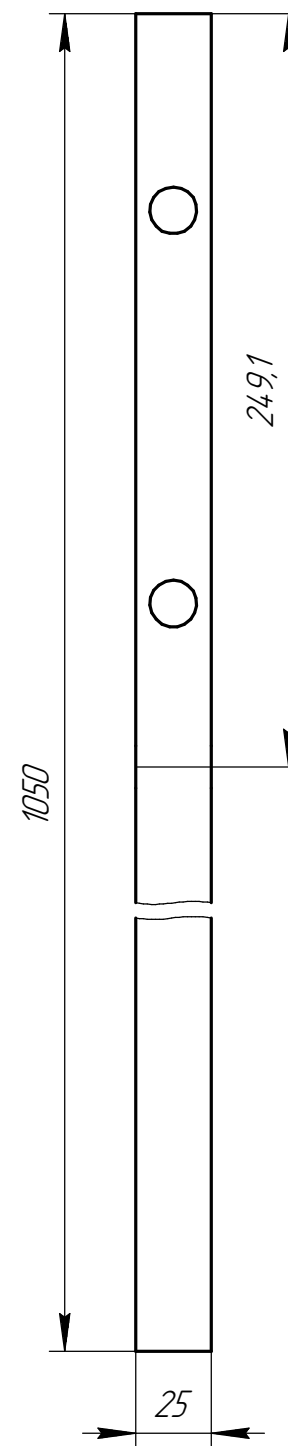


Дет. поз. 3 (1:5)

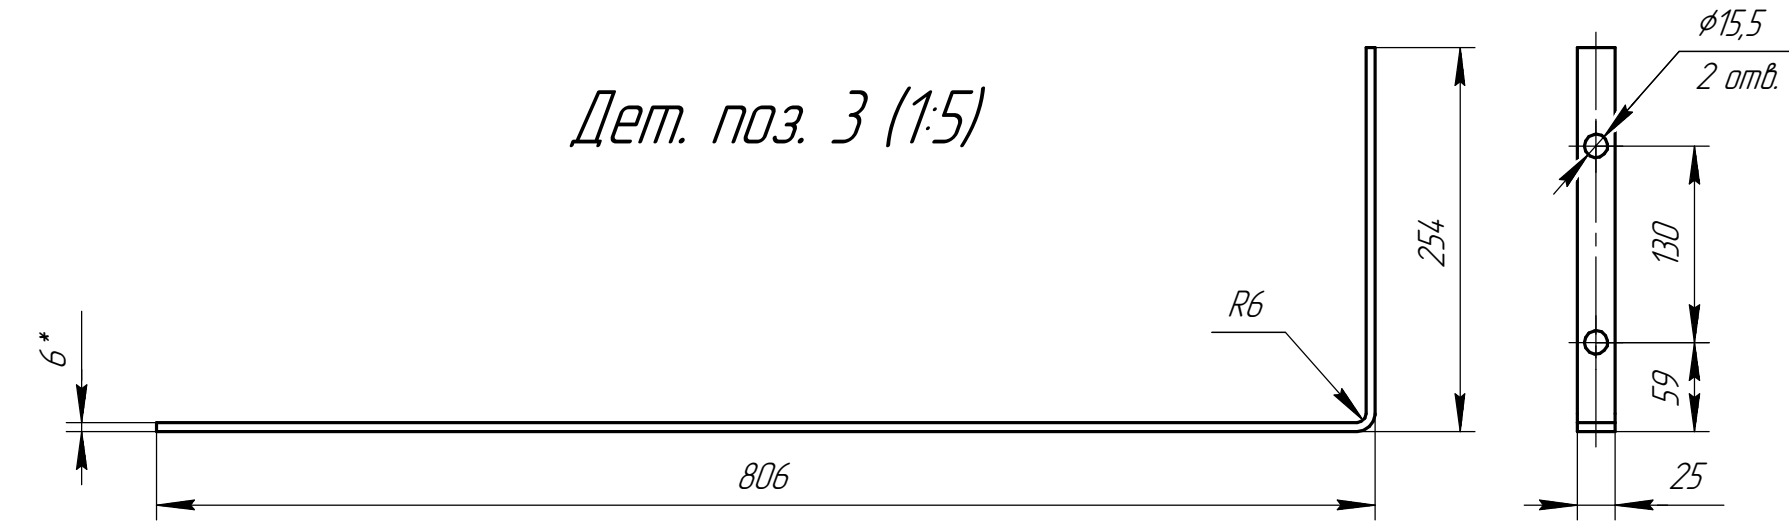


Дет. поз. 8

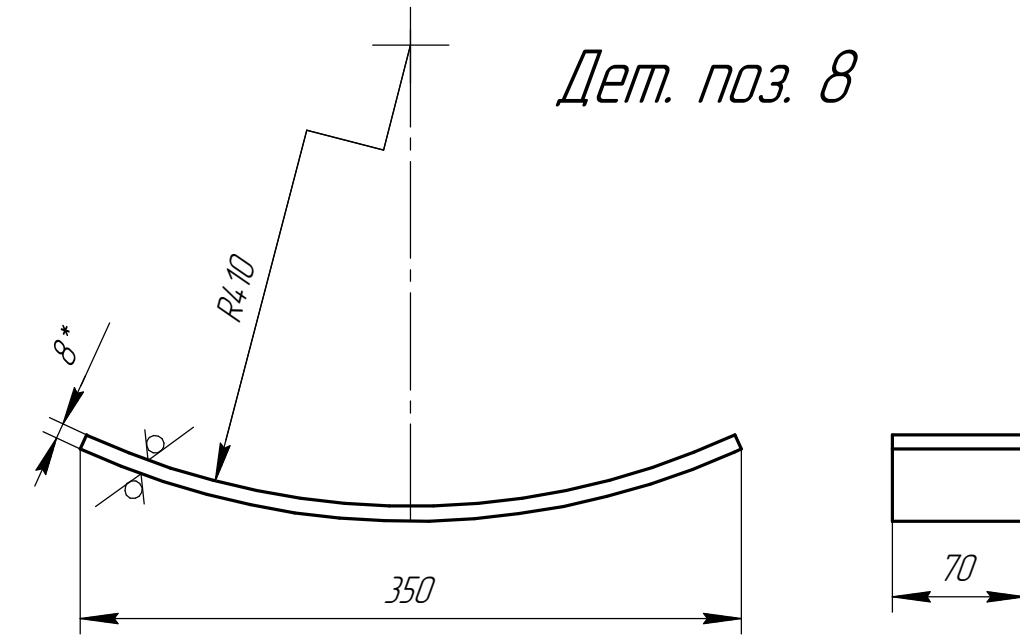


Q₃

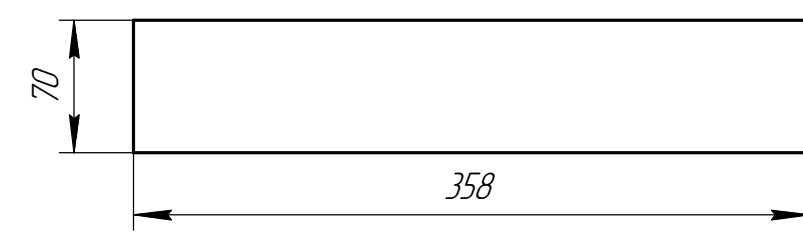


Дет. поз. 7

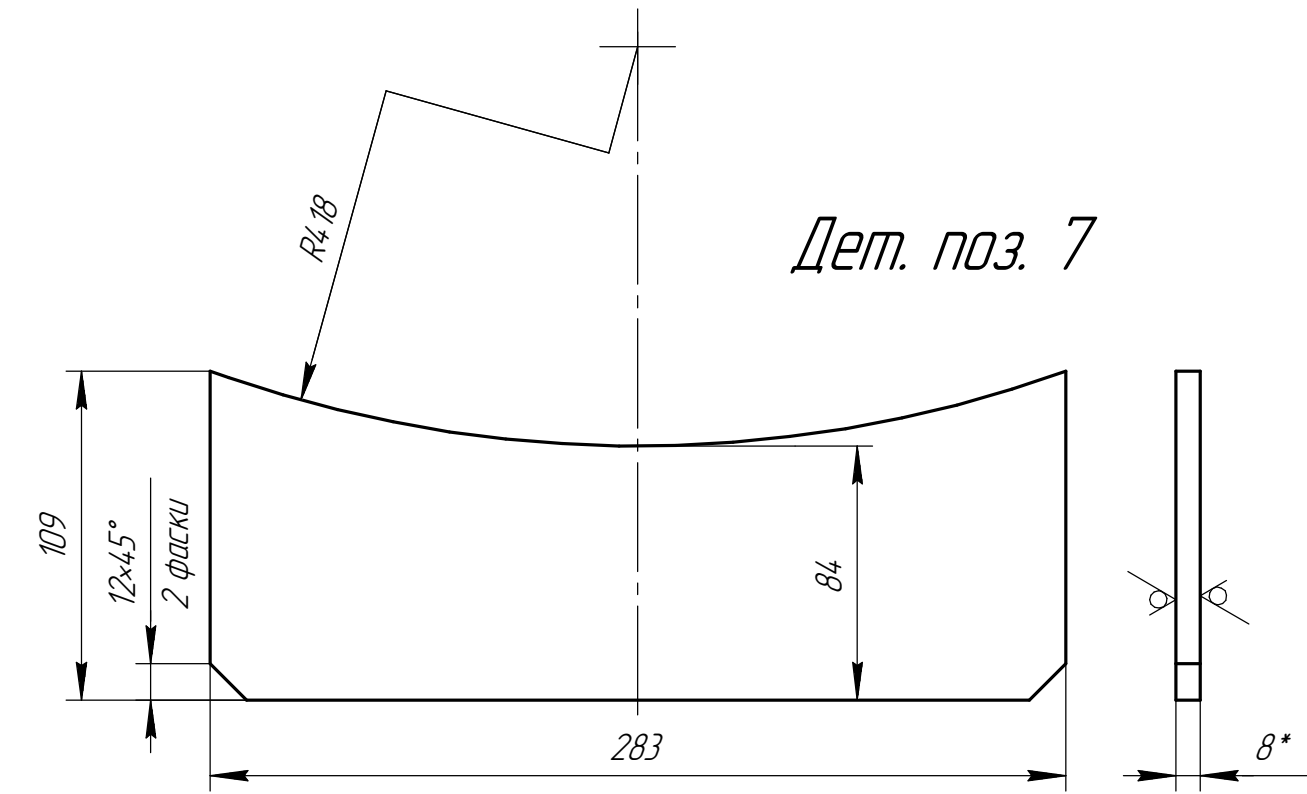

Дет. поз. 6 (1:5)

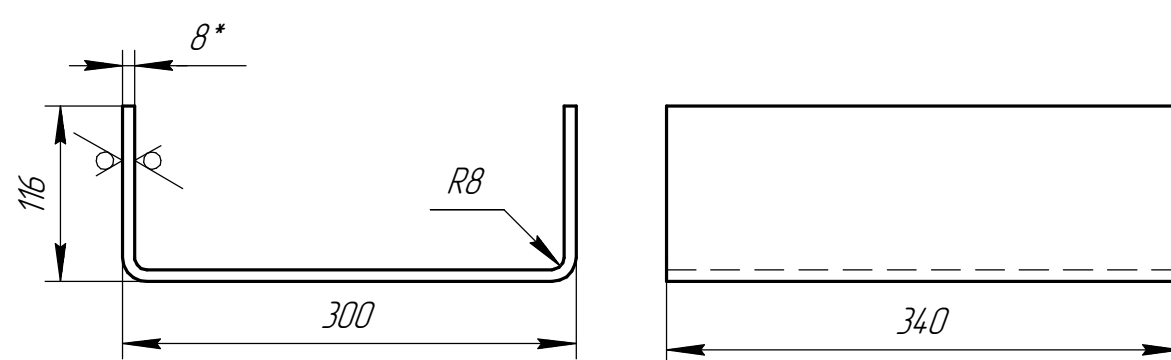






Q₃(1:5)

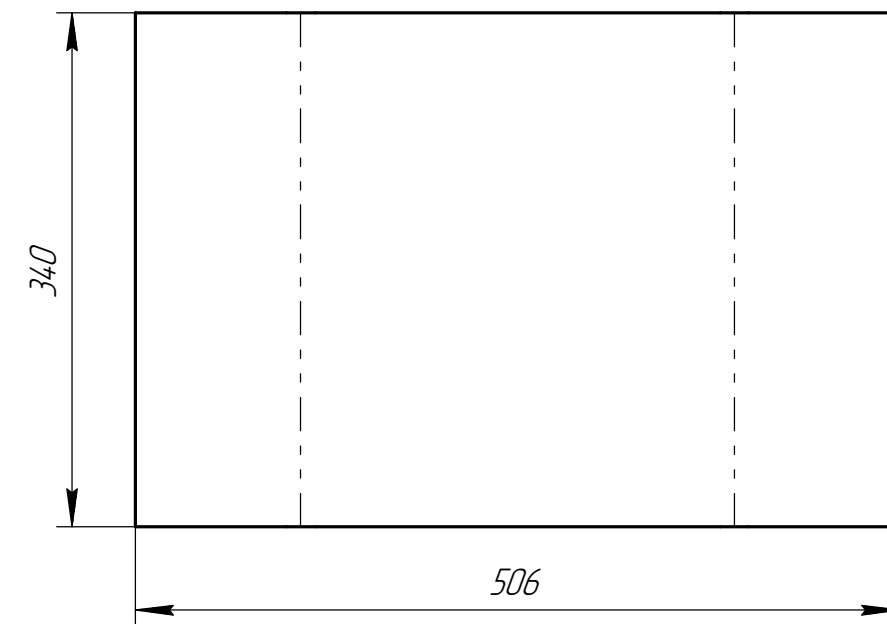


Дет. поз. 5 (1:1)

Дет. поз. 1 (1:5)

Дет. поз. 4 (1:1)

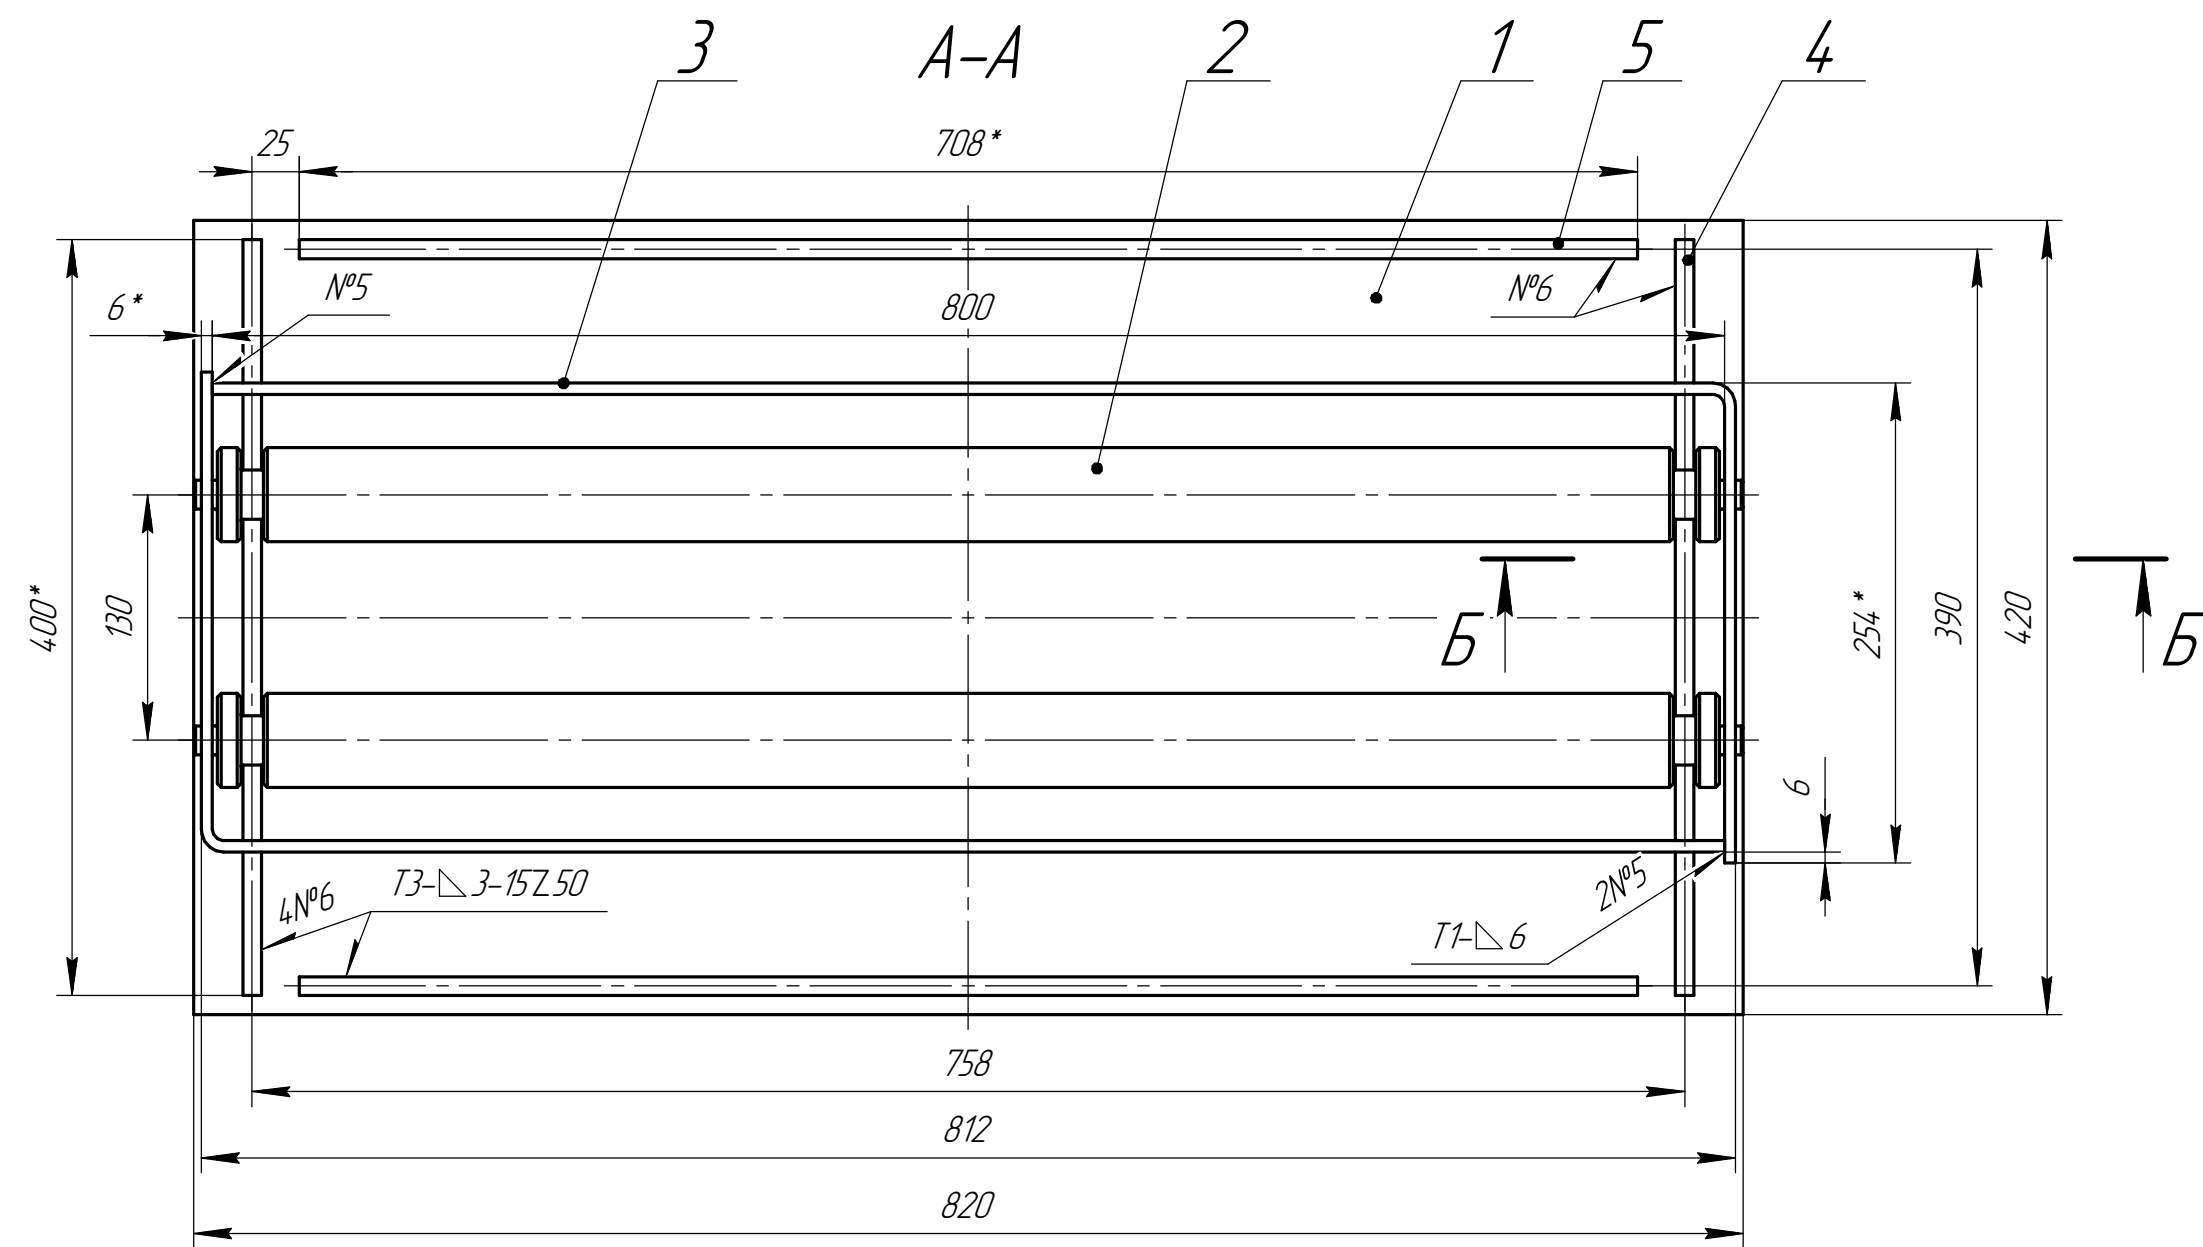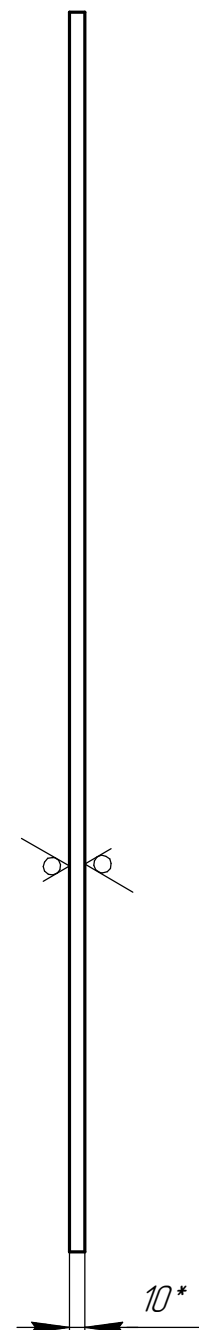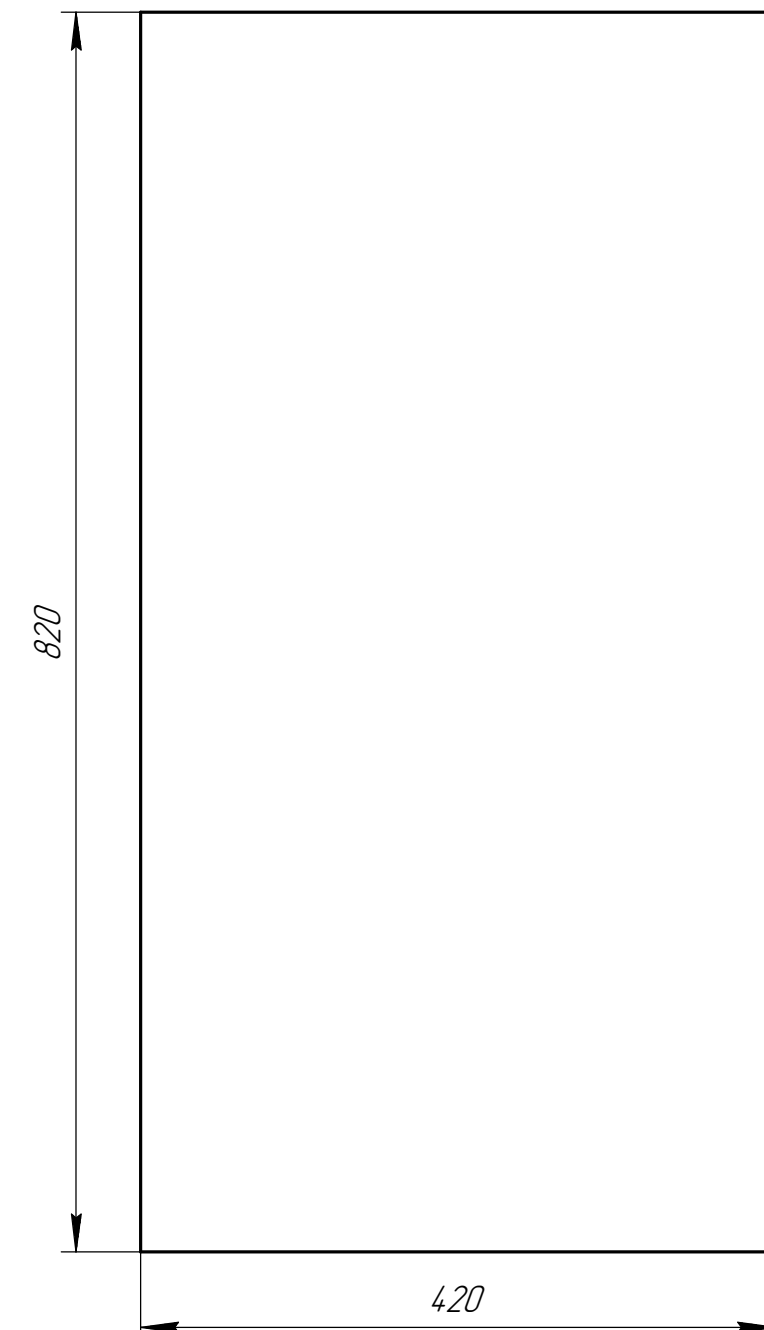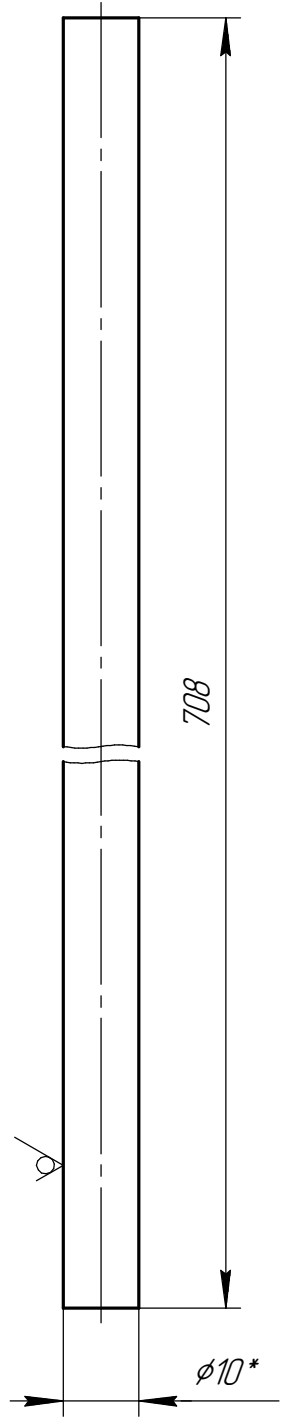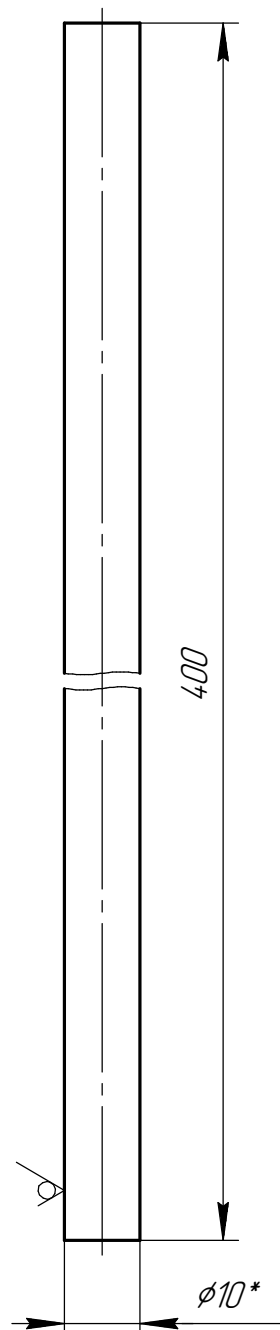

Дет. поз. 2 (1:2)

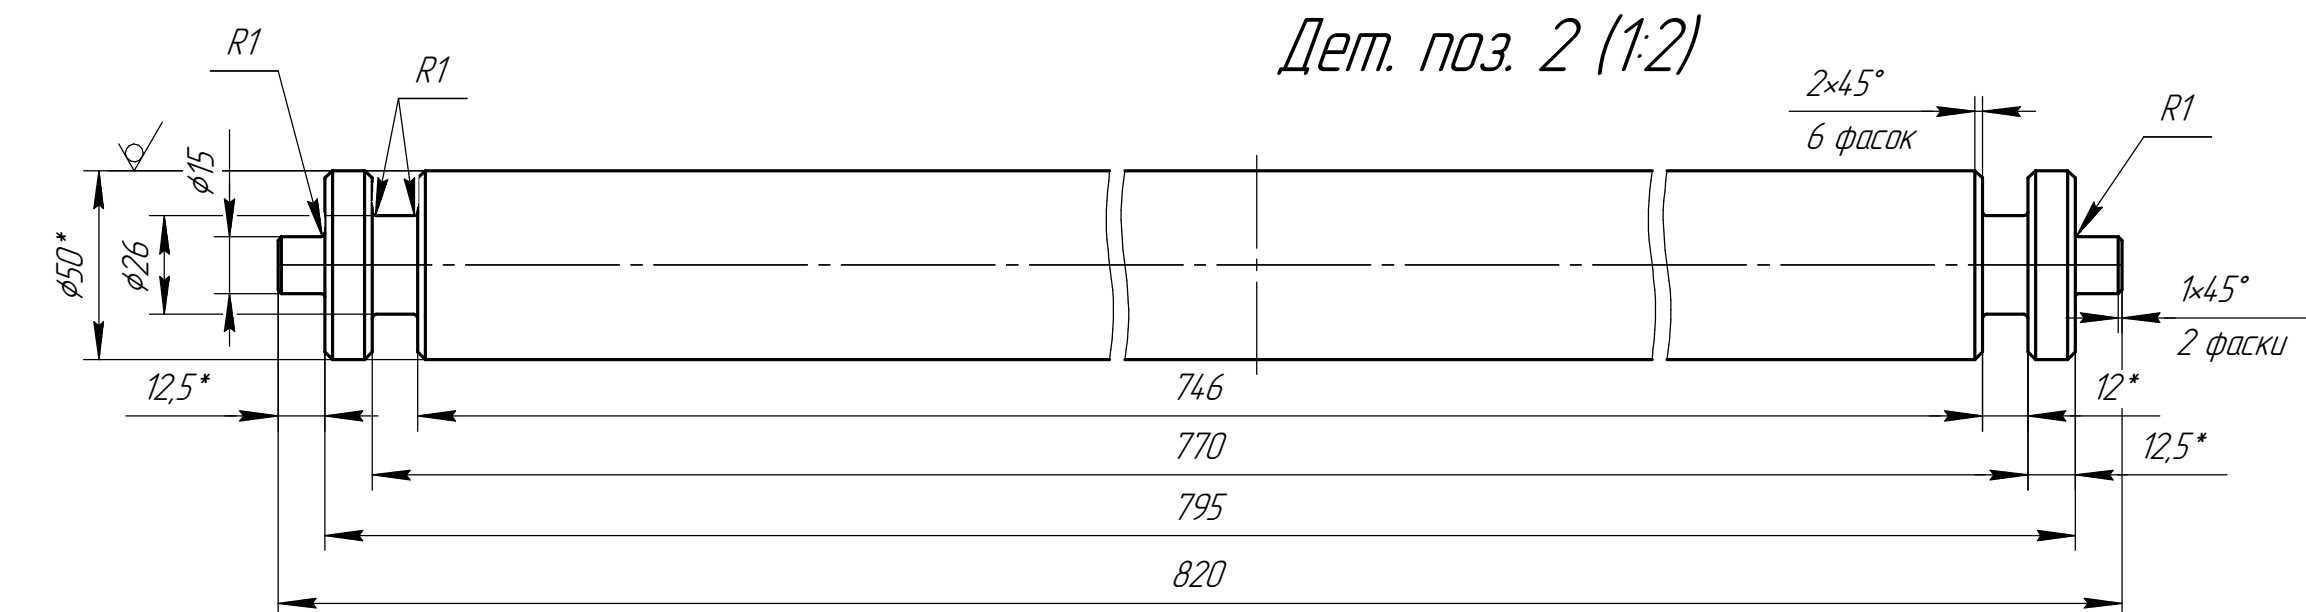

- Общие допуски по ГОСТ 30893.1: Н17, н17, ±IT17/2.
- *Размеры для справок.
- Сварка дуговая в защитном газе по ГОСТ 14 771-76.
- Материалы:
 - Лист ГОСТ 19903-2015, 09Г2С ГОСТ 19281-2014;
 - Круг ГОСТ 2590-2006, 09Г2С ГОСТ 19281-2014;
 - Проволока Св-08Г2С ГОСТ 2246-70.
- Площадь покрытия 2,55 м².
- Основные технические требования по ОСТ 36-146-88.

Поз.	Обозначение	Наименование	Кол.	Прим.
1	420x820x10	Плита опорная	1	27,04 кг
2	φ50, L=820	Каток	2	12 кг
3	1050x25x6	Угольник	2	1,22 кг
4	φ10, L=400	Круг	2	0,25 кг
5	φ10, L=708	Круг	2	0,44 кг
6	506x340x8	Основание	1	10,79 кг
7	283x109x8	Ребра	2	1,22 кг
8	358x70x8	Подушка	2	1,57 кг

820-КН-Б12				Опора катковая направляющая		
Изм.	Лист	№ докум.	Подп.	Дата	Лист	Масса
Разраб.					100,45	14
Проб.					Лист	Листов
Т.контр.					1	
Н.контр.						
Утв.						