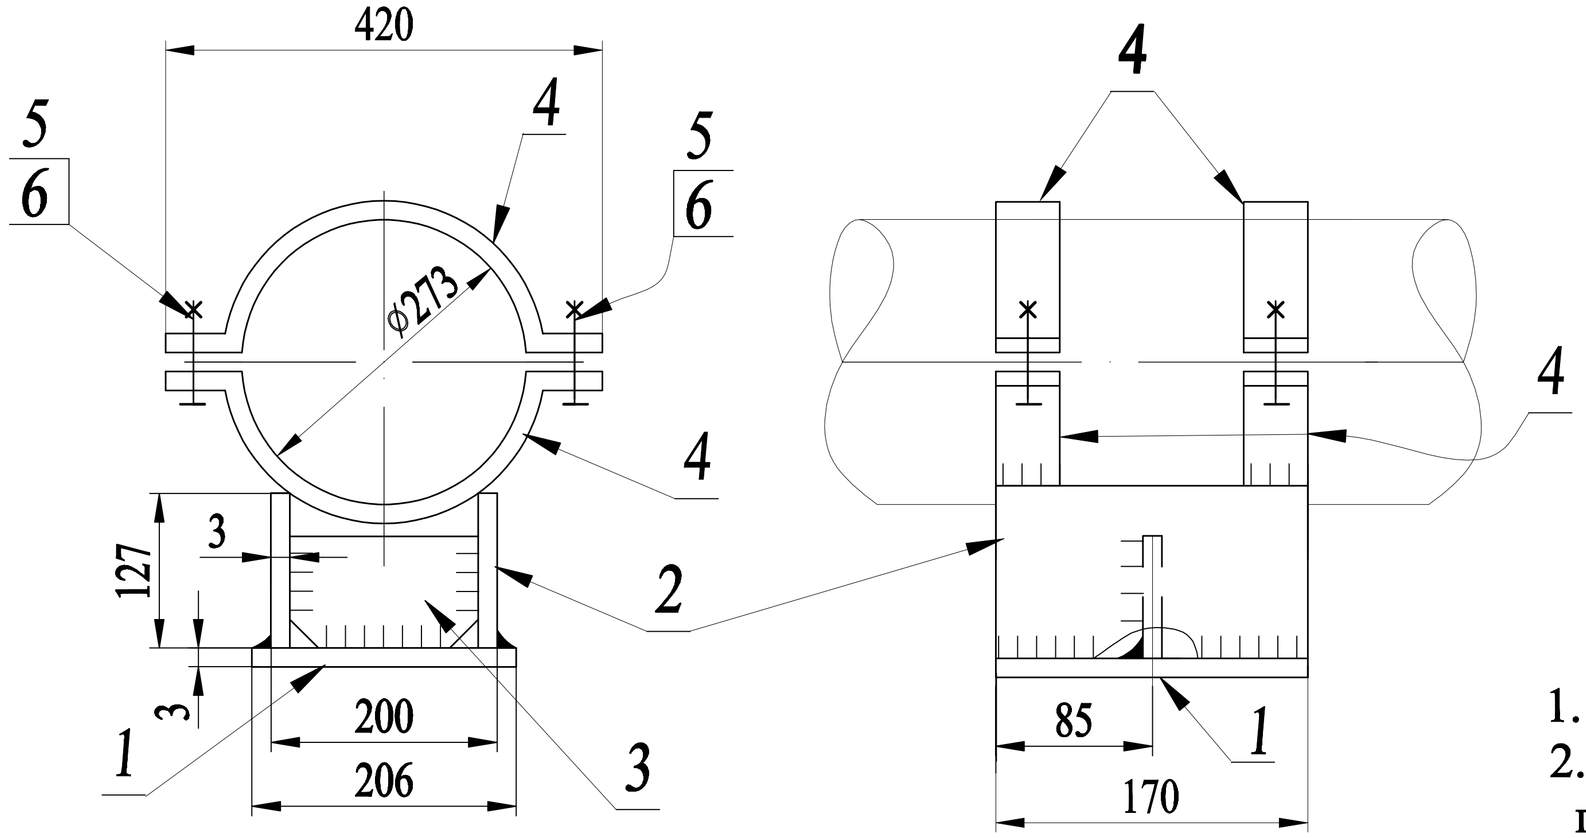

Корпус

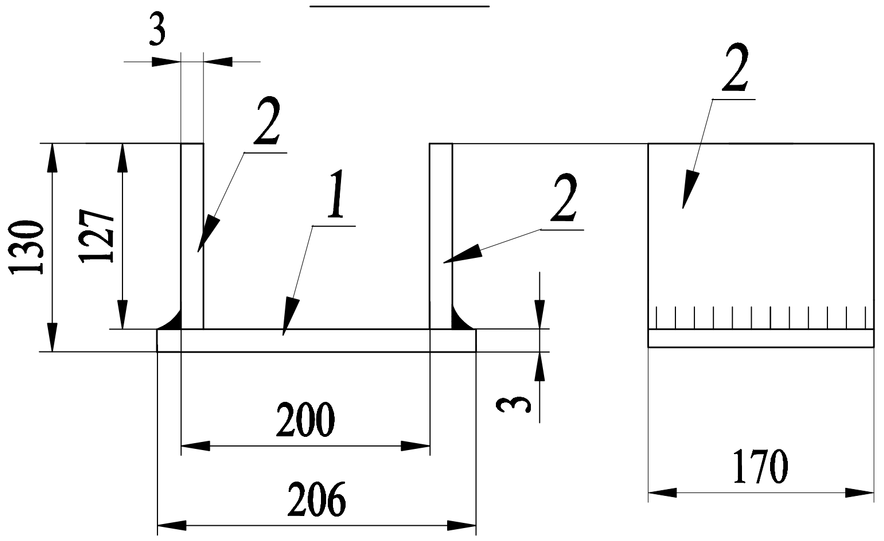

Поз.4

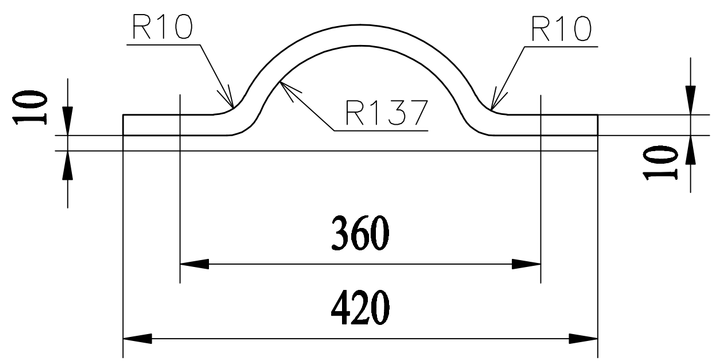

Развертка поз.4

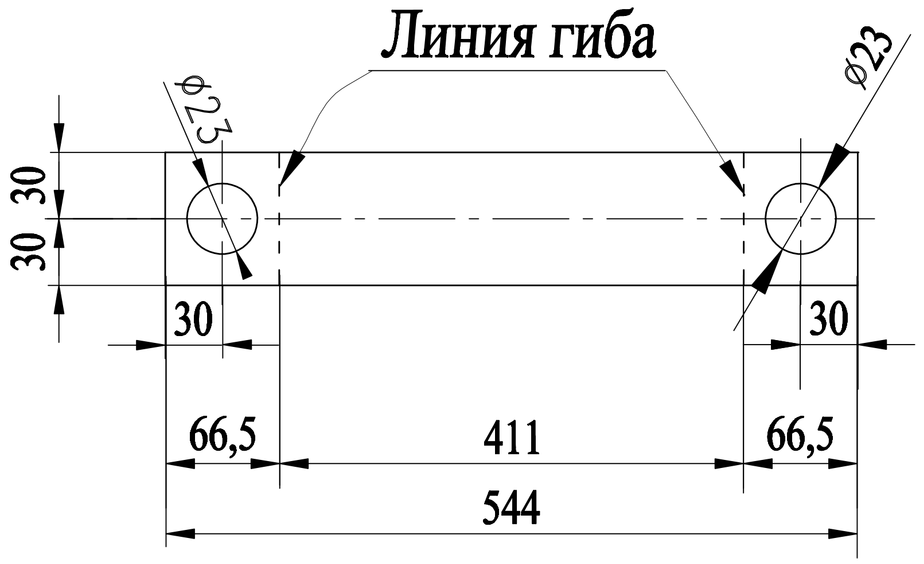

Поз.3

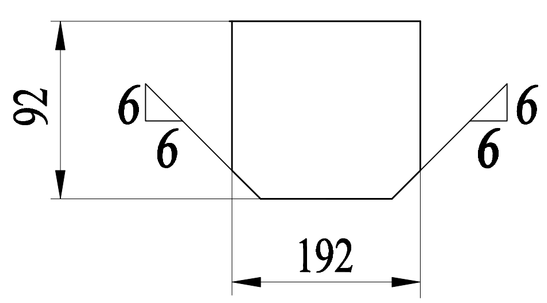

Выборка металла

Материал		Сечение	Масса в кг	ГОСТ
ГОСТ 19281-88	09Г2С	лист 3	2,22	
		лист 10	10,0	
		Гайка М20	0,28	
		болт М20х60	0,87	
Итого			13,37	кг

Примечания:

1. Сварные швы - 3 мм
2. Сварка полуавтоматическая по ГОСТ 14771-76 в среде СО2. Сварочная проволока Св-08Г2С по ГОСТ2246-70 диаметром 1,4-2,0 мм.
3. На заводе окрасить грунтом ГФ-021 по ГОСТ 25129-82 в два слоя.
4. Не указанные предельные отклонения размеров по H 14. h 14. ± IT 14/2
5. Опору маркировать: 273-КХ-АС11

				на сварные швы			0,1	13,47			
	6	4		Гайка М20-7Н.6ГОСТ5915-70*		0,071	0,28				
	5	4		болт М 20	60	0,219	0,87				
	4	4		- 60 х 10	544	2,5	10,0				
	3	1		- 92 х 3	192	0,4	0,4				ср.угл.
	2	2		- 127 х 3	170	0,5	1,0				гнуть отв.
	1	1		- 170 х 3	206	0,82	0,82				гнуть
ОТПР. ЭЛЕМ.	ДЕТ.	Т. КОЛ-ВО	Н.	СЕЧЕНИЕ	ДЛИНА	ШТ.	ОБЩ.	ЭЛЕМ.	МАРКА СТАЛИ		ПРИМЕЧАНИЯ
						МАССА В КГ					

СПЕЦИФИКАЦИЯ СТАЛИ 09Г2С ГОСТ 19281-88

				007.ОС.273.КХ.103.0889.01
Исполнил				Опора 273-КХ-АС11
Проверил				
Рук.груп.				
Гл.конст.				
Гл.техн.				
Гл.инж.	Немиров			

Стадия	Лист	Листов
Р	1	1

ООО НПП "Строительные технологии"