


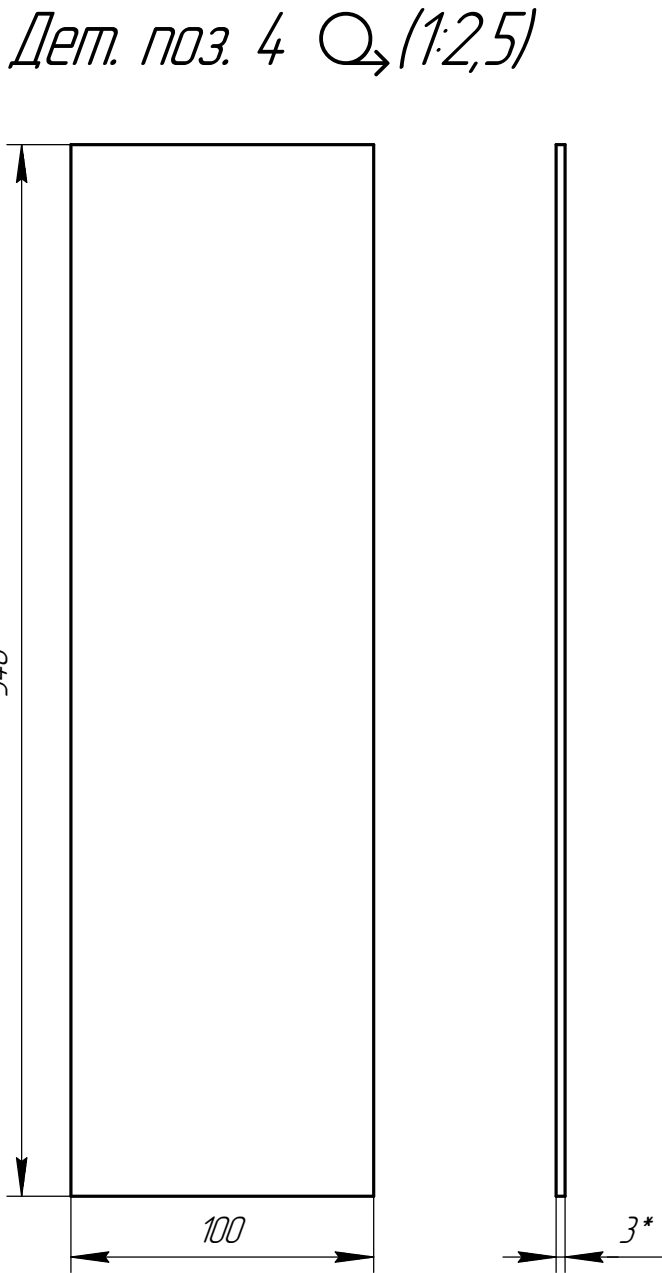
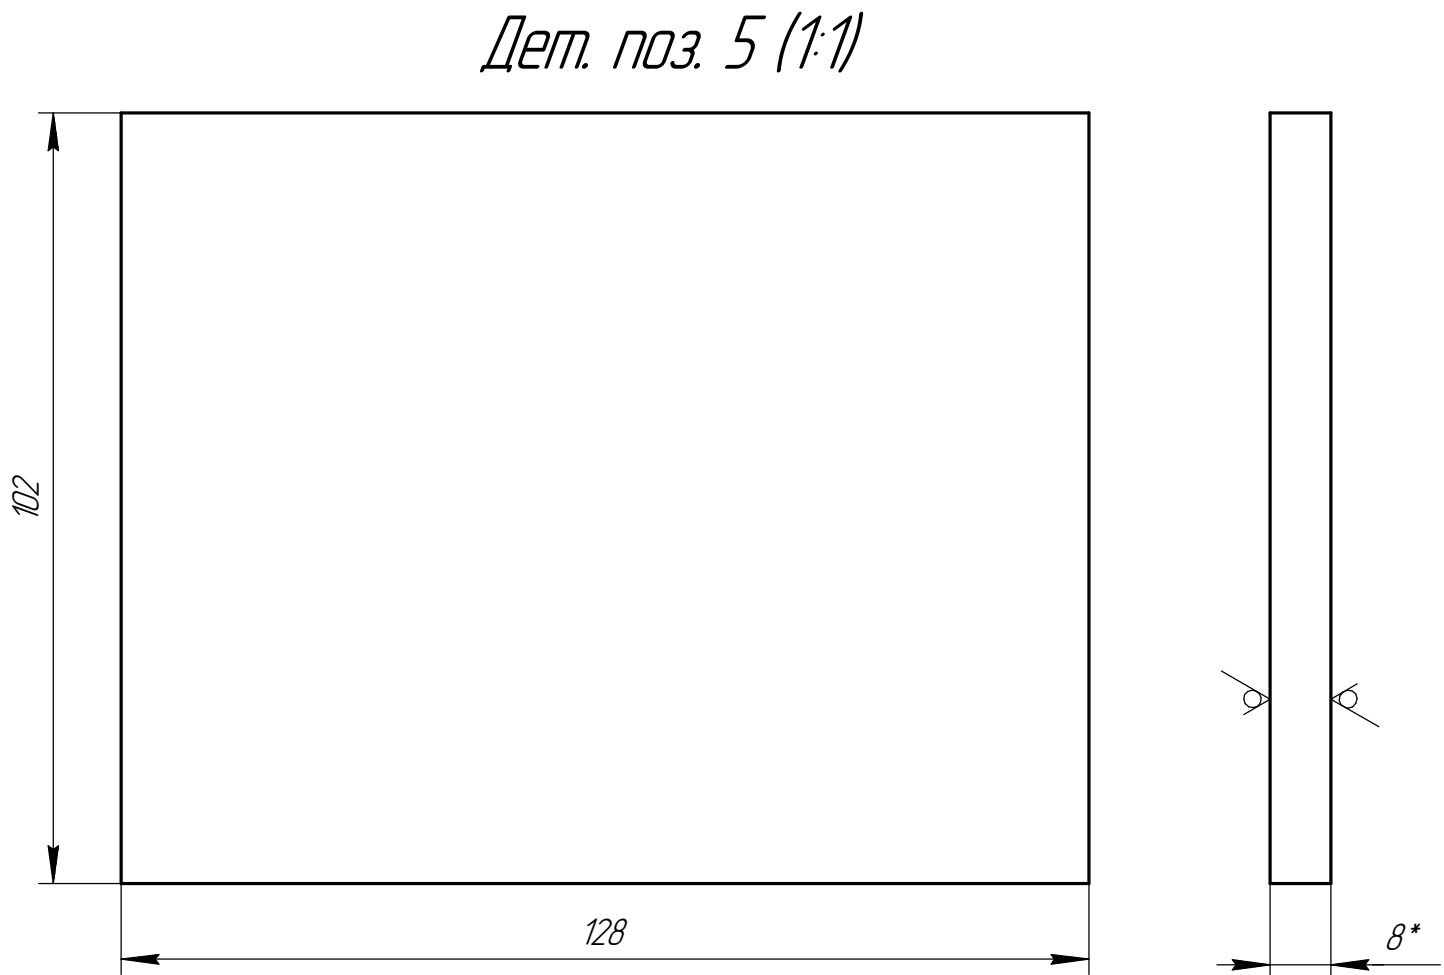
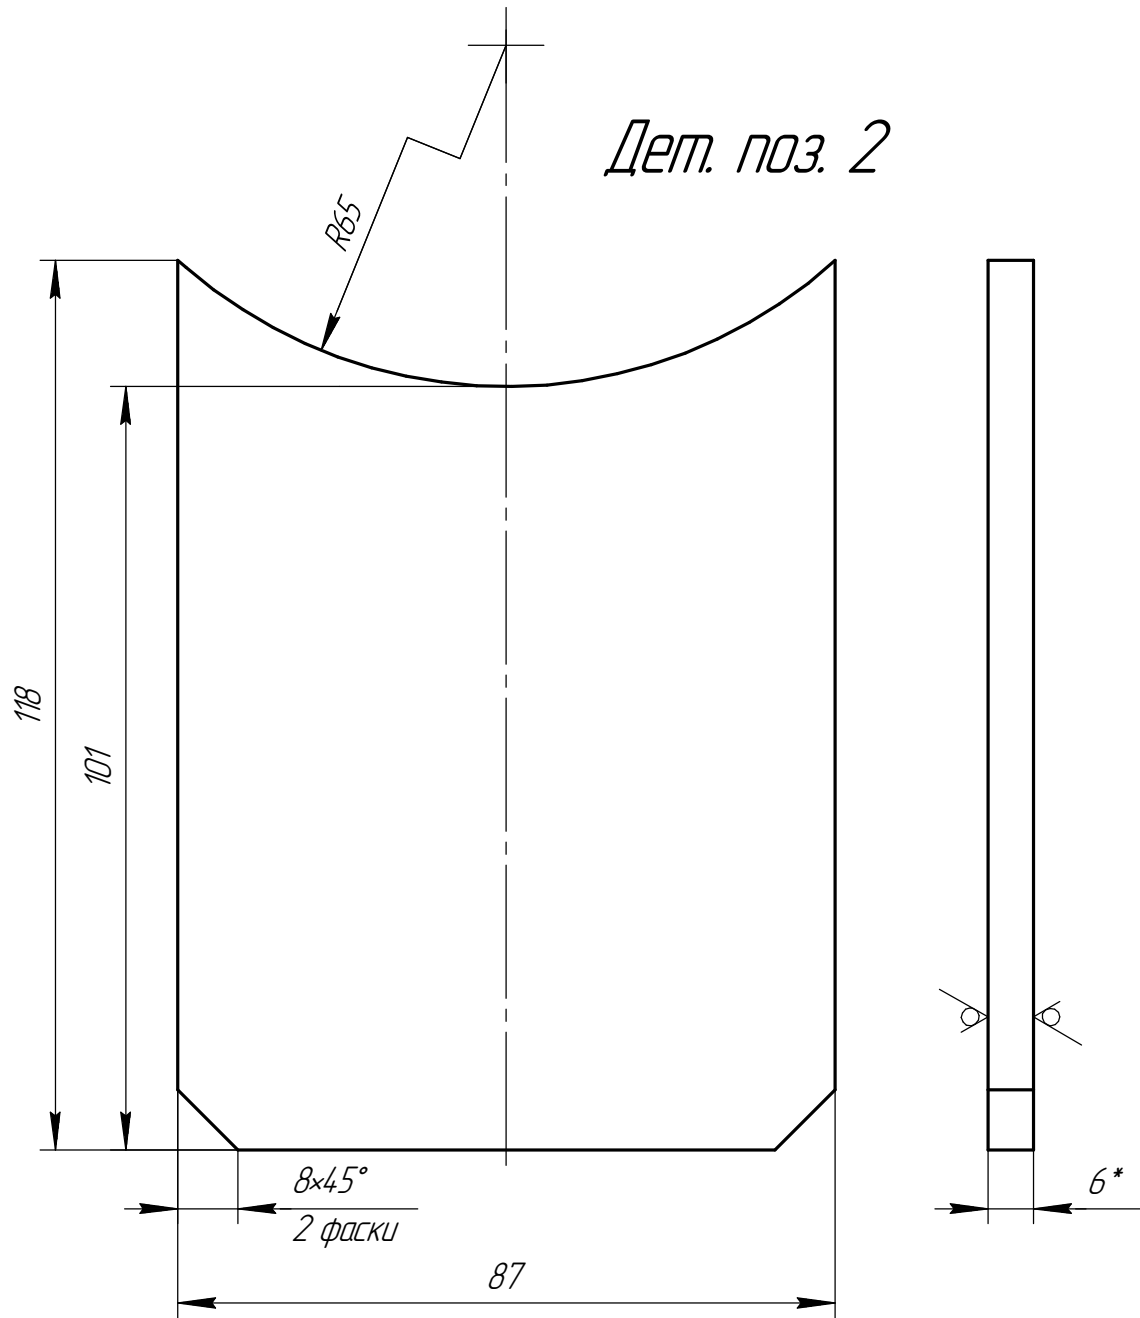
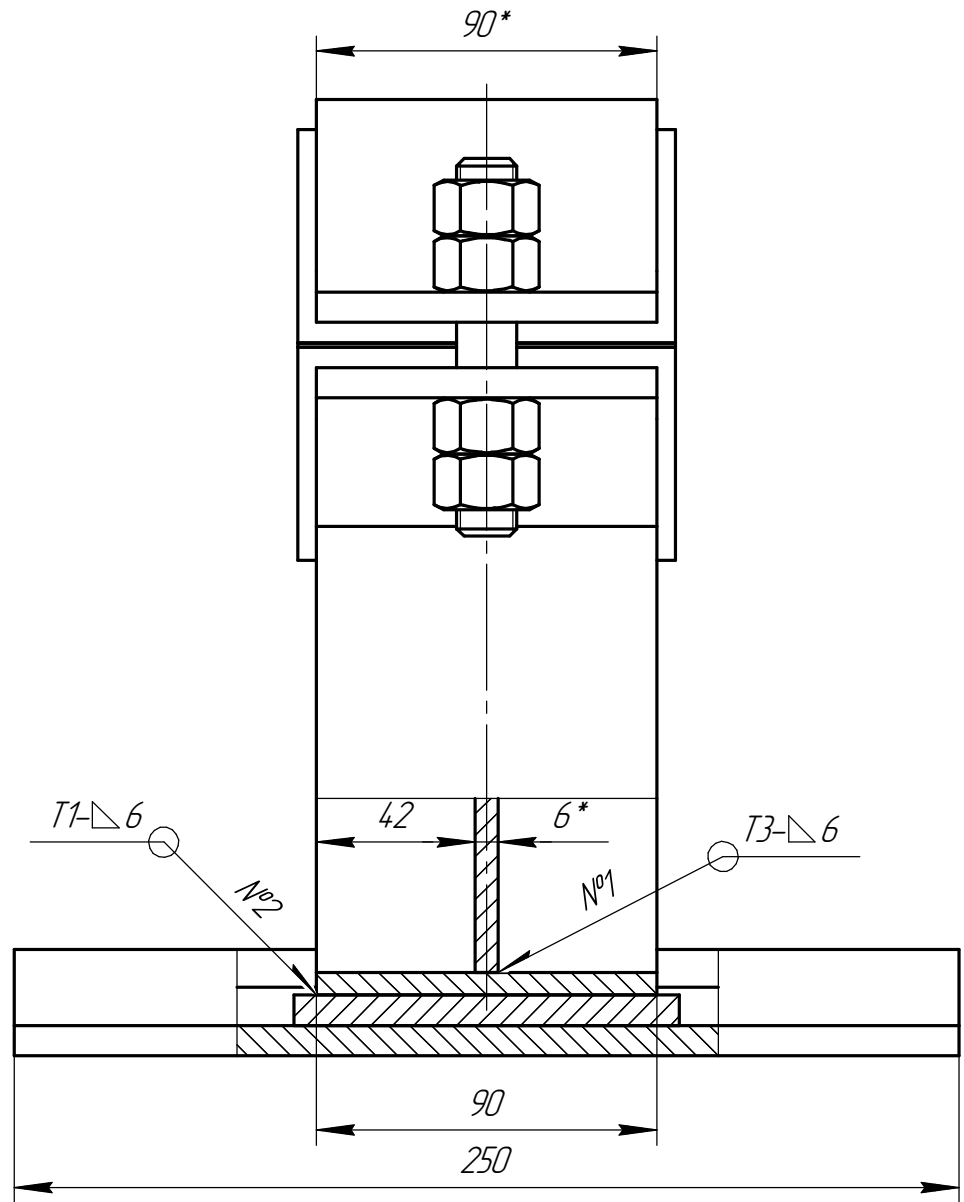
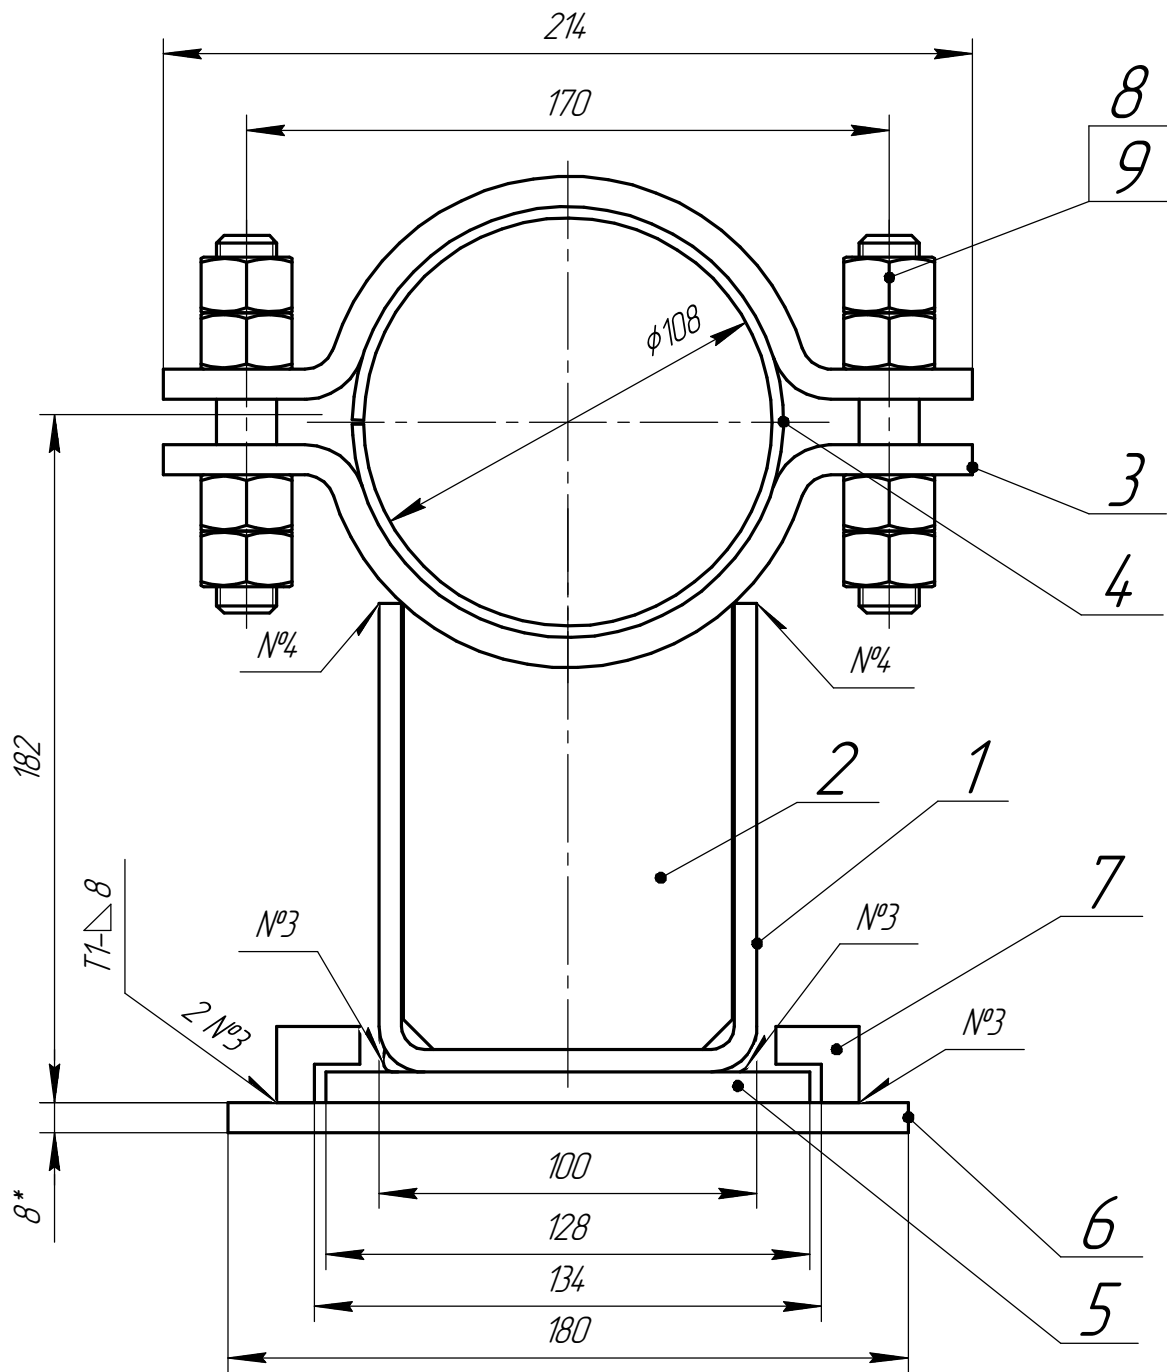
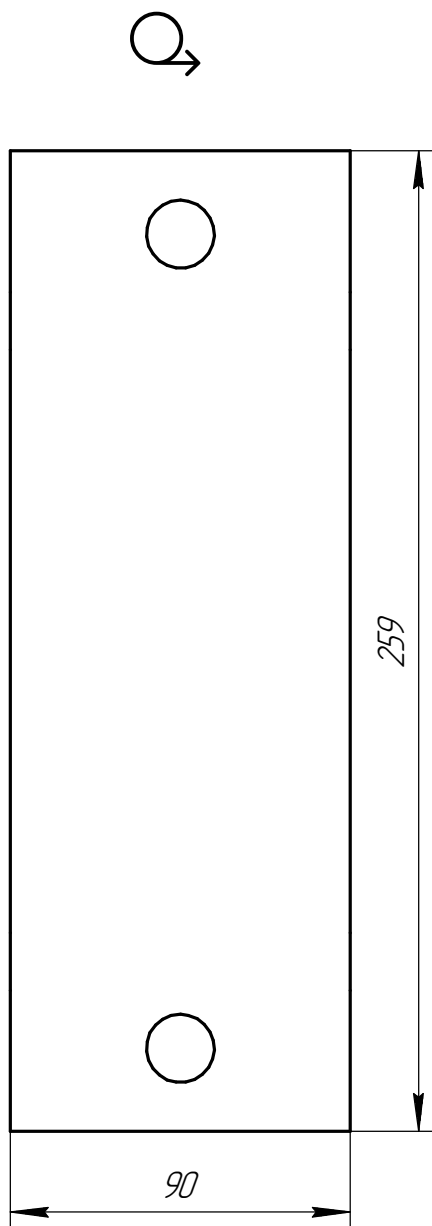


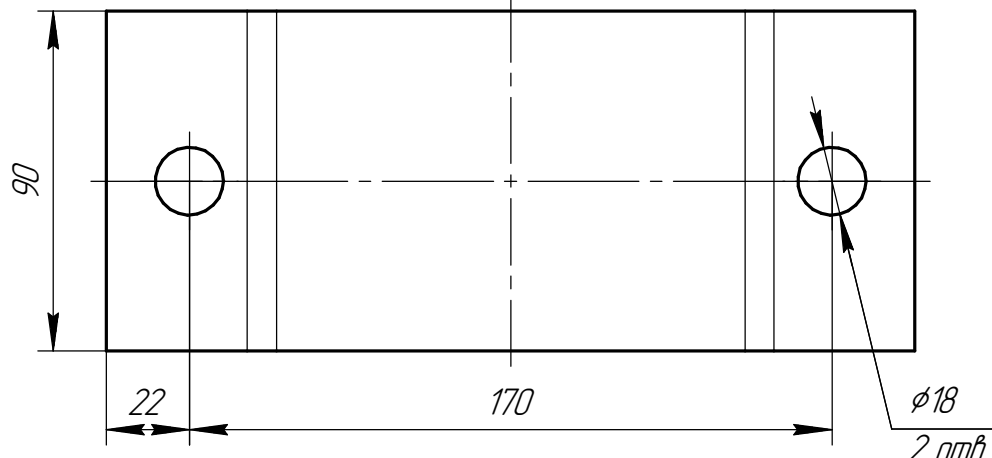


Det. poz. 3

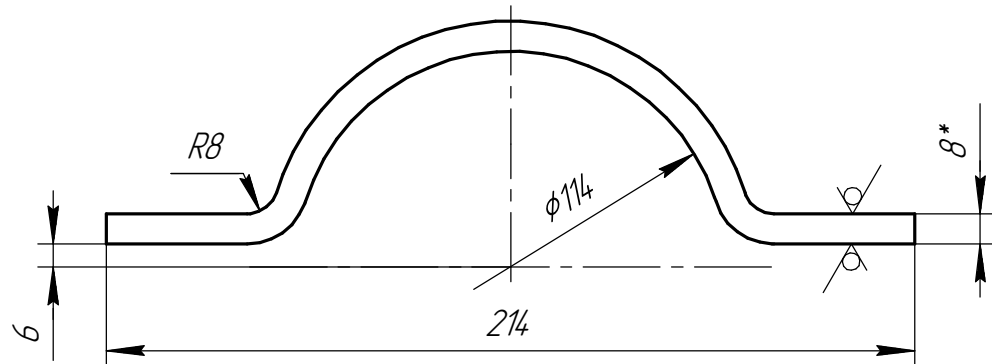



Det. poz. 1

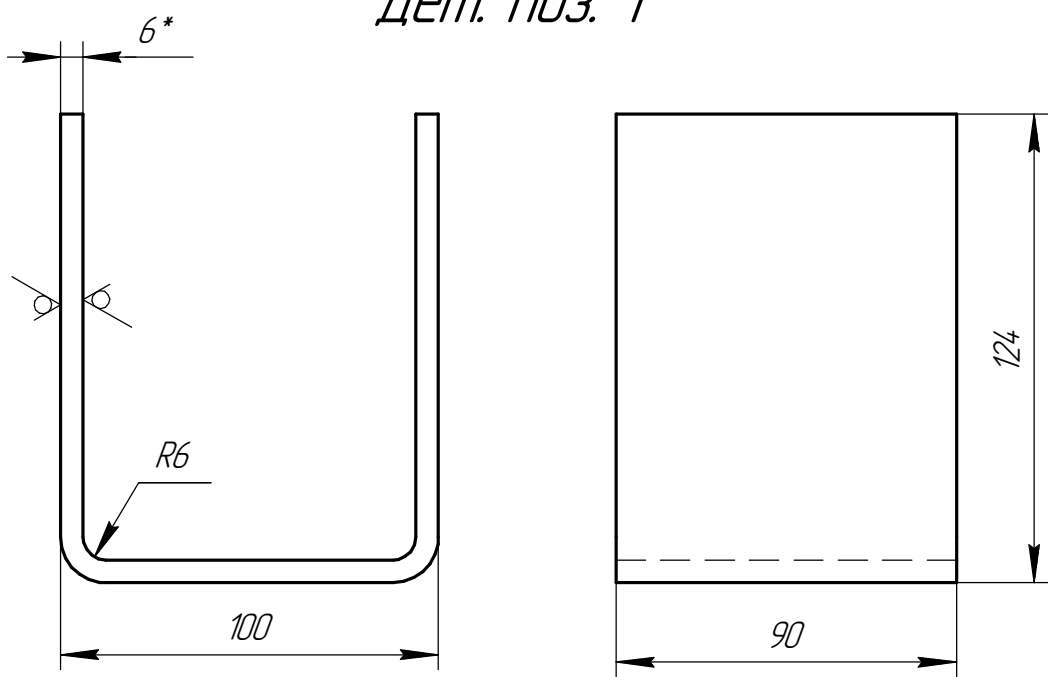


Det. poz. 1

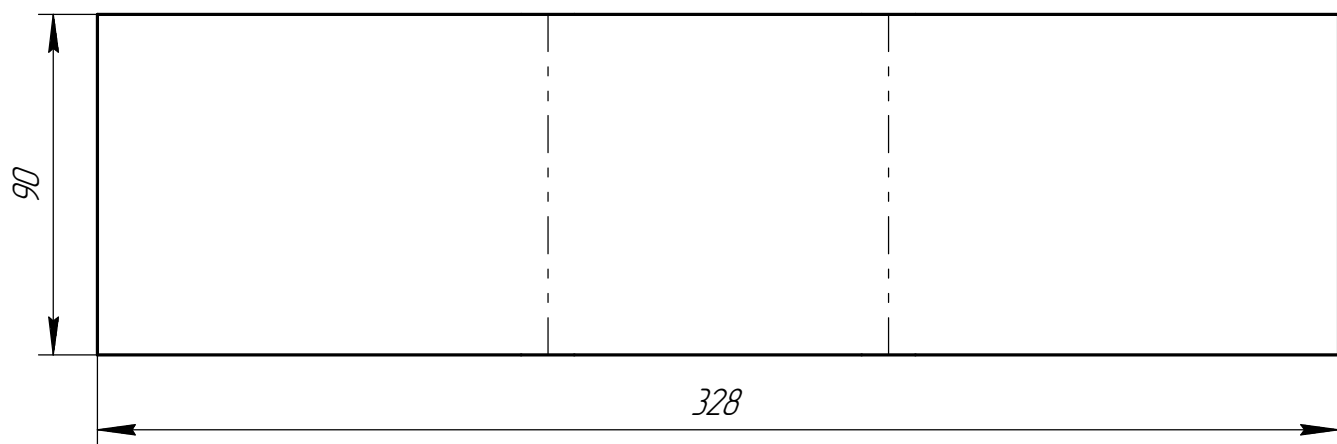

Det. poz. 7 (2:1)

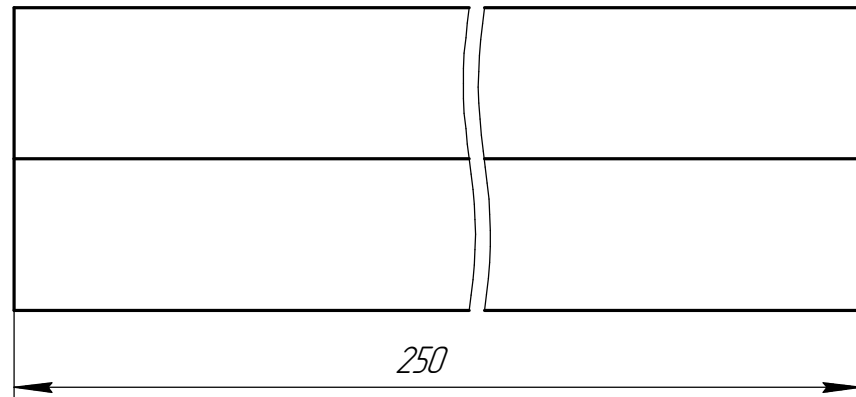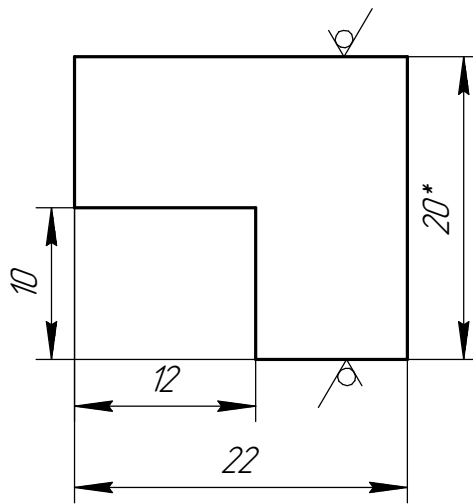

Det. poz. 5 (1:1)

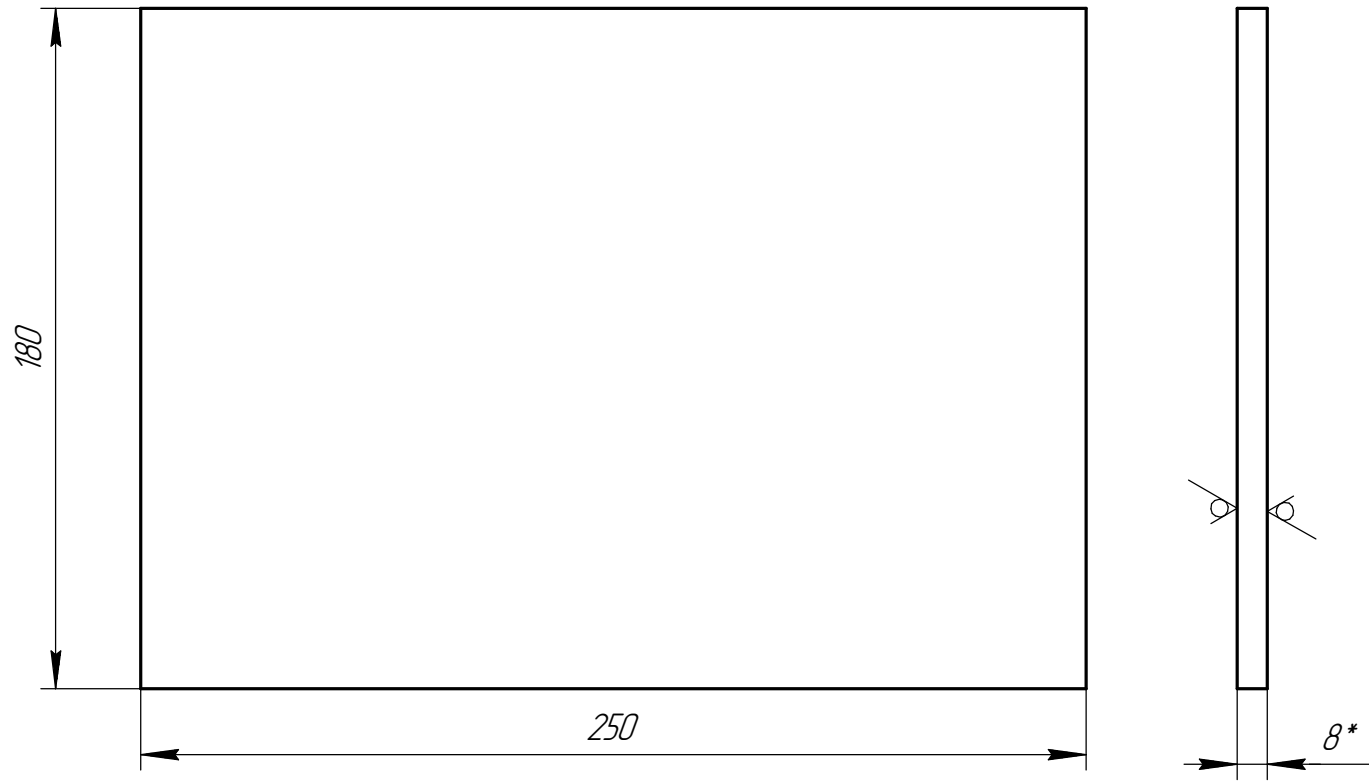

Det. poz. 4 Q, (1:2,5)

1. Общие допуски по ГОСТ 30893.1: Н17, h17, ±IT17/2.
2. *Размеры для справок.
3. Материалы:
 - Лист ГОСТ 19903-2015, 09Г2С ГОСТ 19281-2014;
 - Паронит ПОН ГОСТ 481-80;
 - Сварочная проволока Св-08Г2С ГОСТ 2246-70.
4. Сварка по ГОСТ 14 771-76.
5. Основные технические требования по СТО 79814.898 131-2009.
6. Площадь покрытия 0,45 м².

Поз.	Обозначение	Наименование	Кол.	Прим.
1	328x90x6	Корпус	1	1,39 кг
2	118x87x6	Редра	1	0,43 кг
3	259x90x8	Полухомут	2	1,43 кг
4	348x100x3	Прокладка (паронит)	1	0,21 кг
5	128x102x8	Основание	1	0,72 кг
6	250x180x8	Плита направляющая	1	2,83 кг
7	250x22x20	Направляющая	2	0,63 кг
8	Шпилька М16-6дх100.88.40Х ГОСТ 22042-76		2	0,139 кг
9	Гайка М16-6Н.8.35 ГОСТ 5915-70		8	0,038 кг

Опора 114 СТО 79814.898 131-2009

Изм./Лист	№ докум.	Подп.	Дата	Лит.	Масса	Масштаб
Разраб.					10,38	1:2
Пров.				Лист	Листов	1
Т.контр.						
Н.контр.						
Утв.						