




Перв. примен.
Справ. №

Подп. и дата
Инд. № дудл.
Инд. № инв.
Взам. инв. №
Подп. и дата
Инд. № подл.

Дет. поз. 5 (1:1)

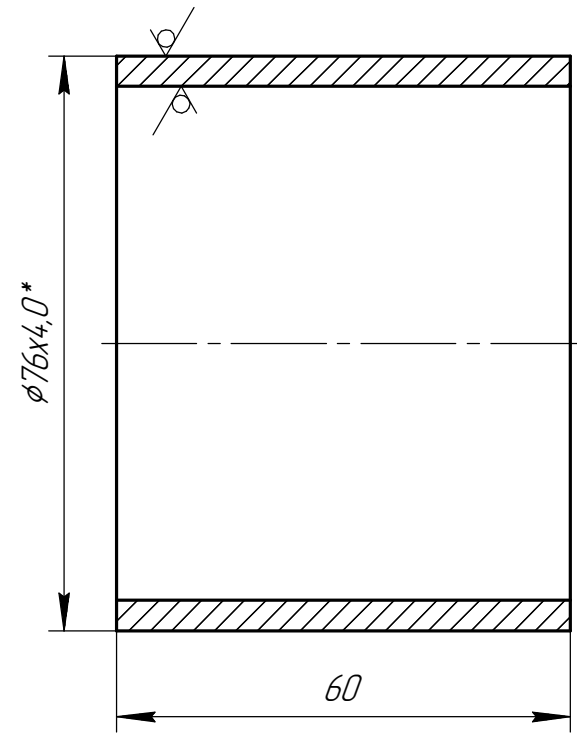


Дет. поз. 4

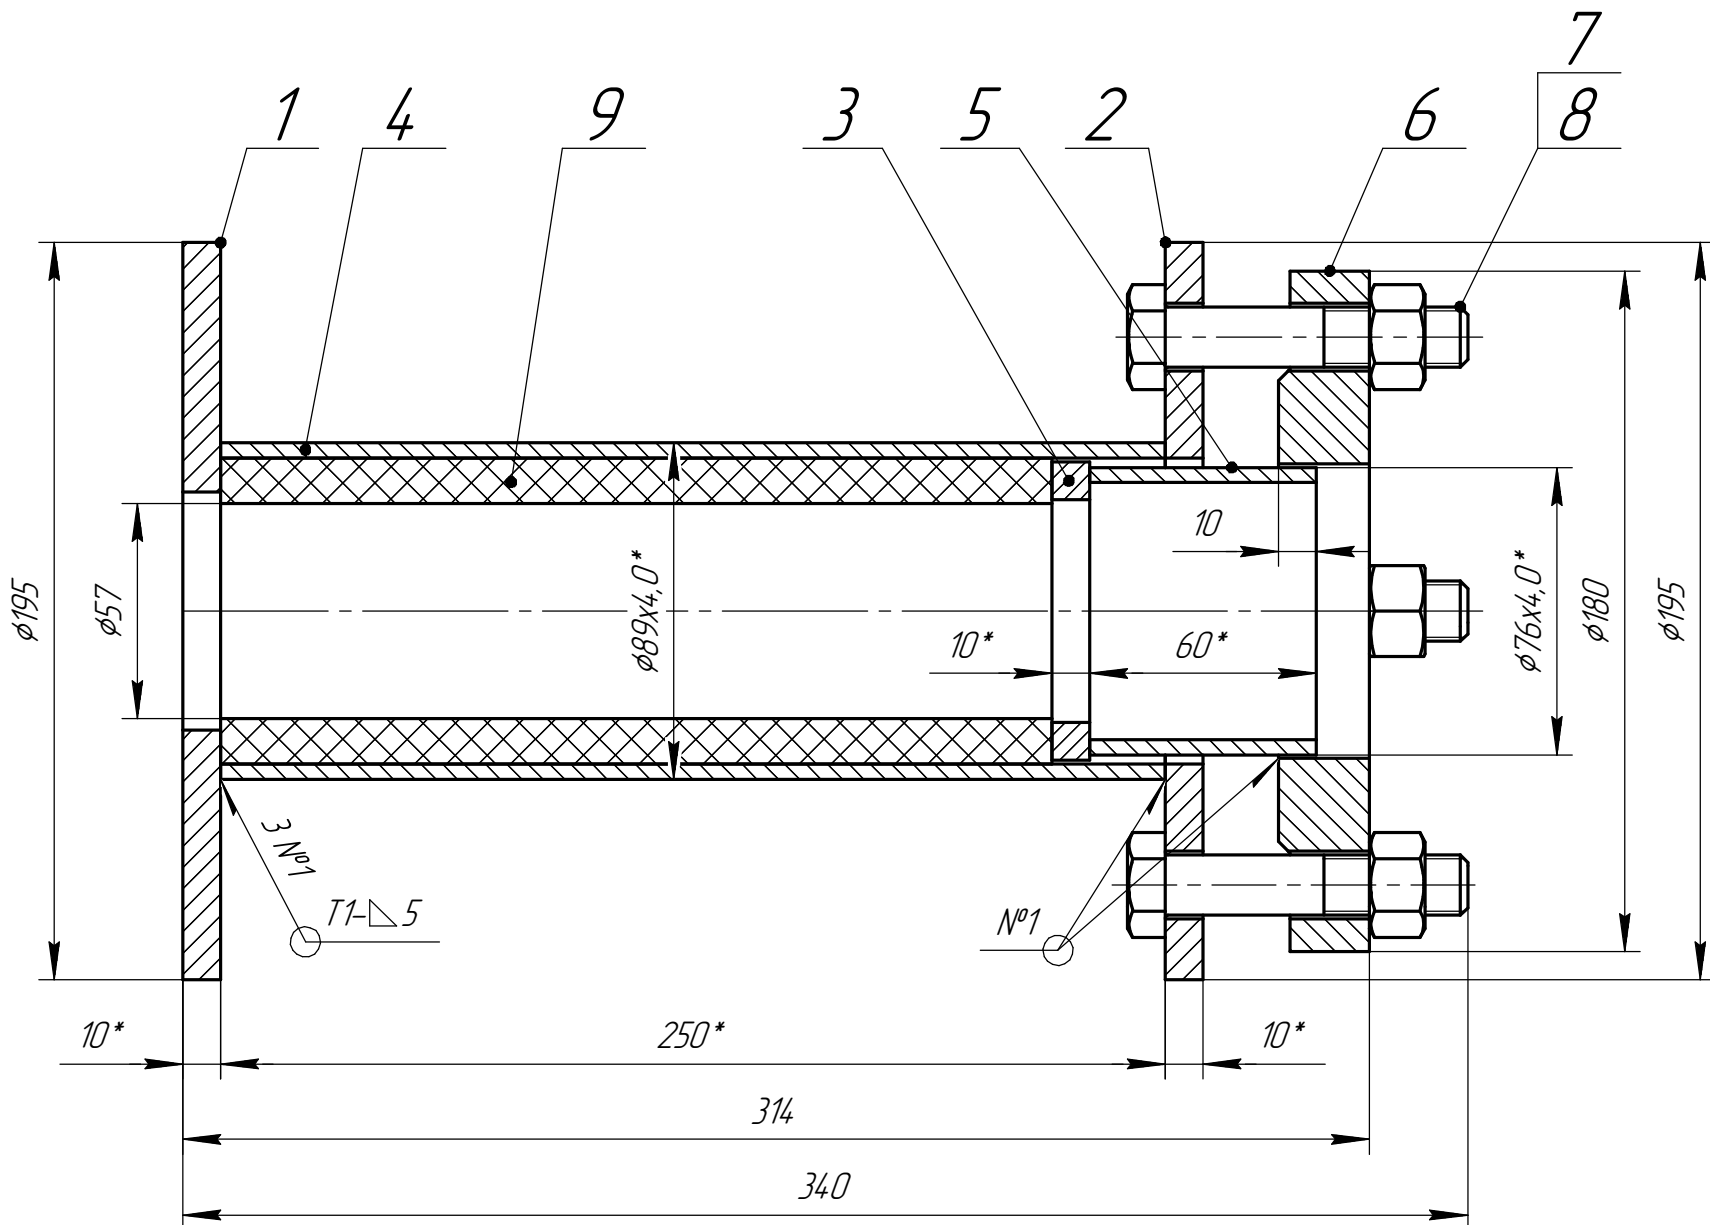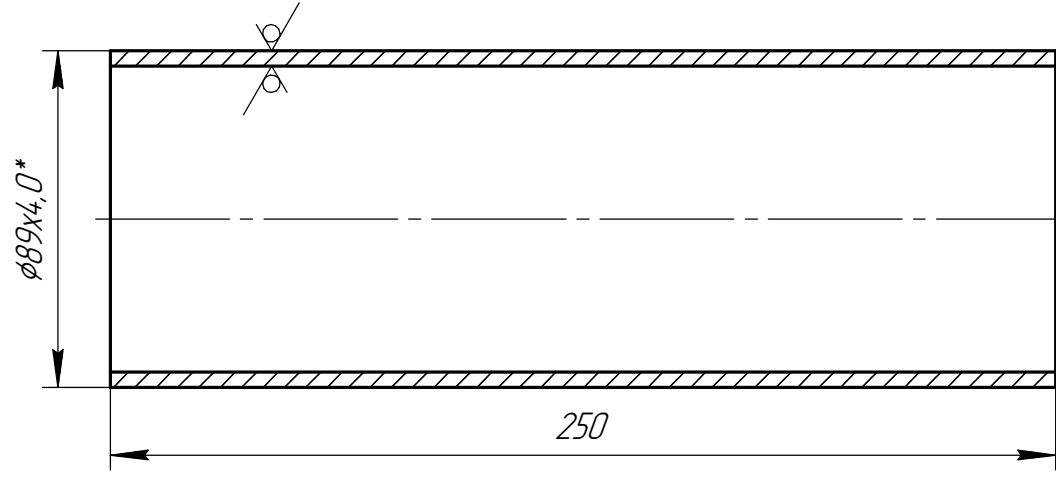


- 1. Общие допуски по ГОСТ 30893.1: H17, h17, ±IT17/2.
- 2. *Размеры для справок.
- 3. Материалы:
 - Лист ГОСТ 19903-2015, Ст3 ГОСТ 14637-89;
 - Труба ГОСТ 10704-91, Ст3 ГОСТ 10705-80;
 - Сварочная проволока Св-08Г2С ГОСТ 2246-70.
- 4. Сварка по ГОСТ 14771-76.
- 5. Дет. поз. 10 условно не показана. На монтаже определить размеры и приварить.


Дет. поз. 1 (1:2,5)

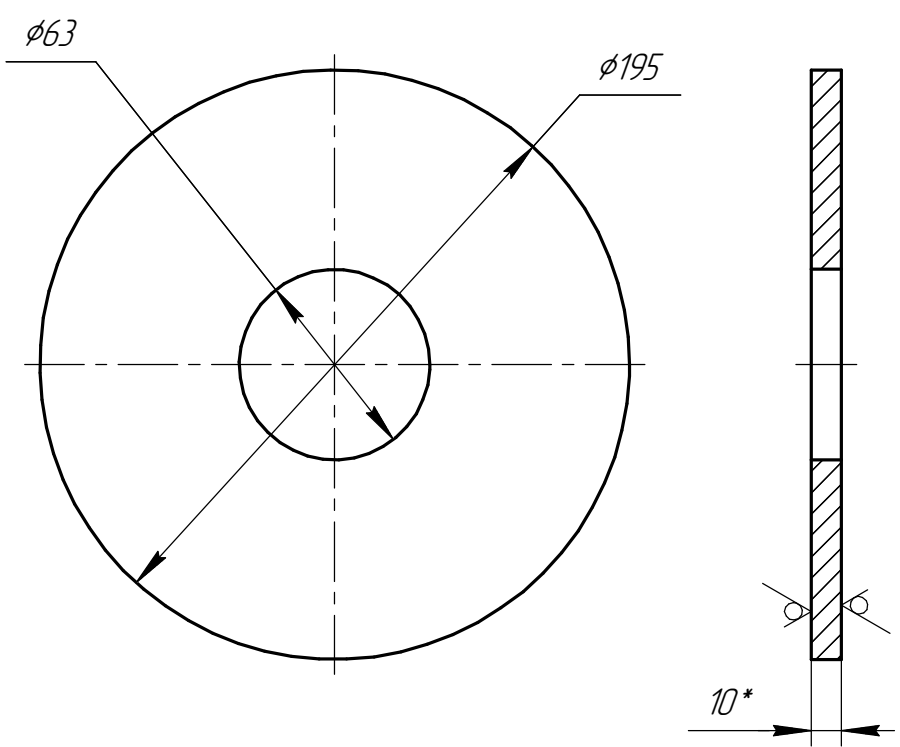

Дет. поз. 2 (1:2,5)

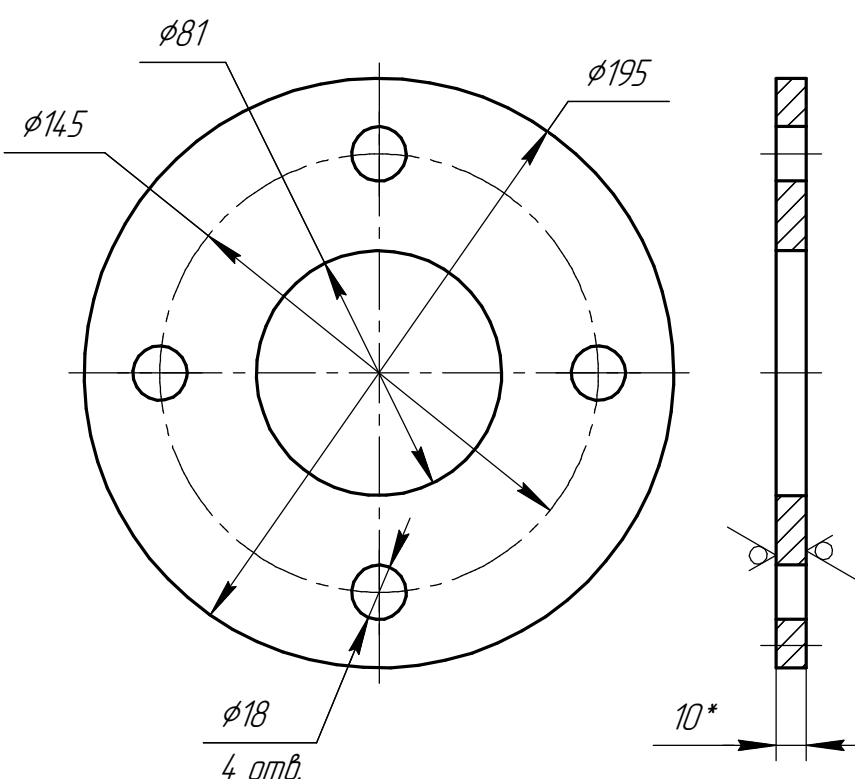

Дет. поз. 3 (1:1)

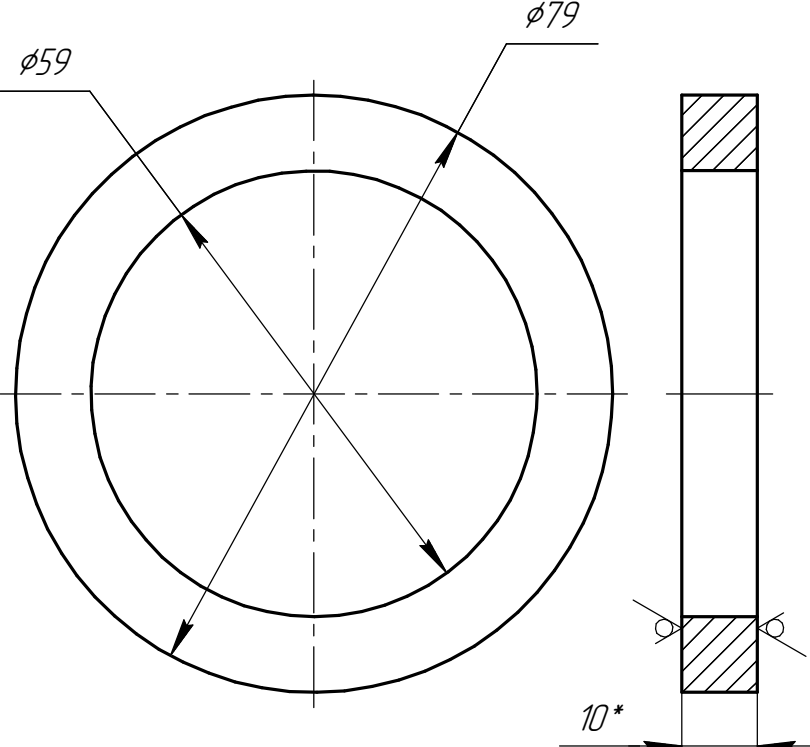

Поз.	Обозначение	Наименование	Кол.	Прим.
1	φ195x10	Кольцо	1	кг
2	φ195x10	Кольцо	1	кг
3	φ79x10	Кольцо	1	кг
4	φ89x4,0 L=250	Труба	1	кг
5	φ76x4,0 L=60	Труба	1	кг
6		Фланец 1-65-16 Ст3сп ГОСТ 12820-80	1	кг
7		Болт М16-6gx80.58.019 ГОСТ 7798-70	4	0,161 кг
8		Гайка М16-6H.5.019 ГОСТ 5915-70	4	0,038 кг
Прочие материалы				
9		Набивка сальниковая прографиченная φ12 мм ГОСТ 5152-84	7	м.п.
10		Арматура φ8	2,7м.п.	1,07 кг
24-001-БСК-032/01-24-1-ТС				
Сальник газонепроницаемый Ду50			Лит.	Масса
			11,53	1:2
			Лист	Листов 1
Копировал				
Формат А2				