

Рис. 1


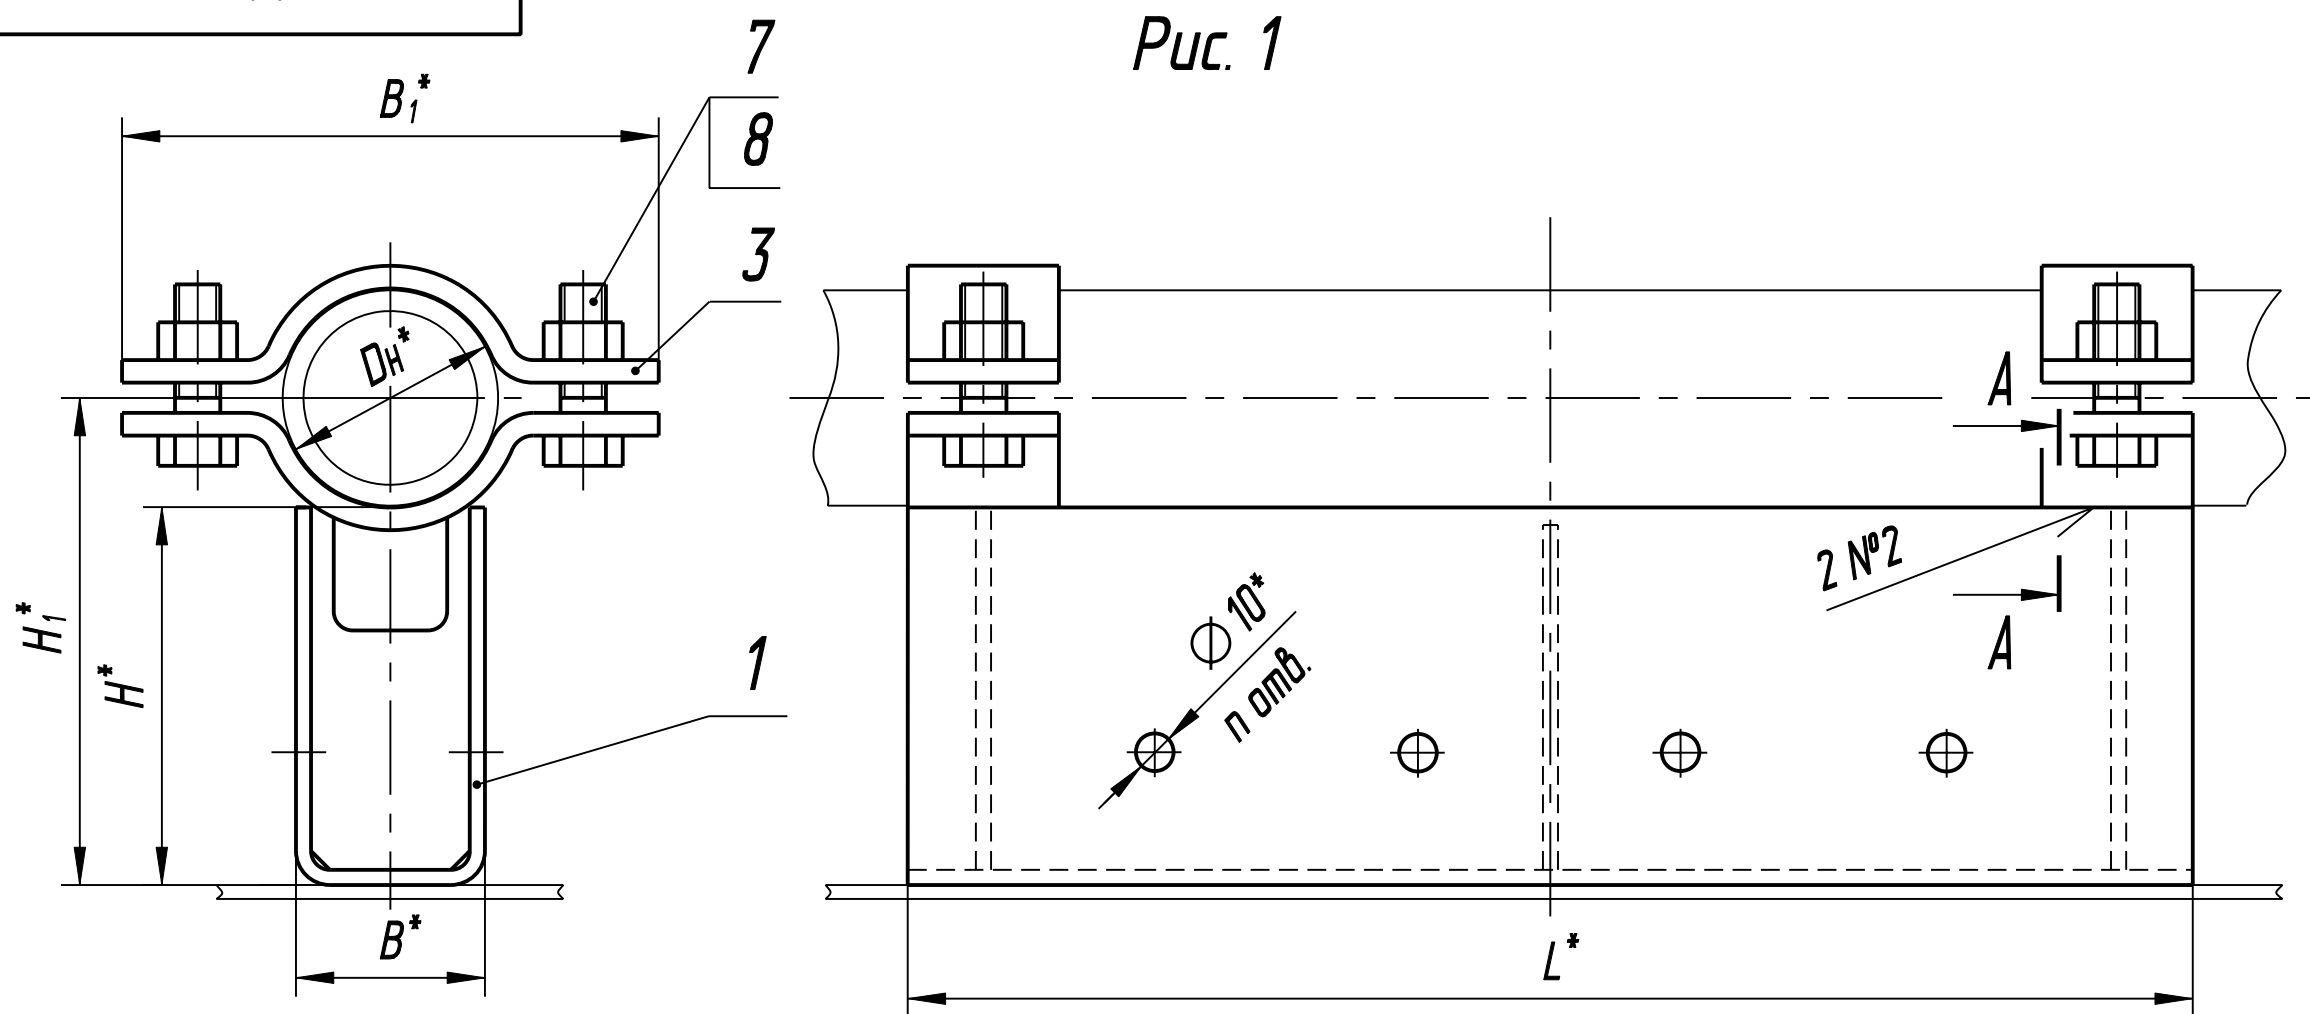


Рис. 2
Остальное-см. рис. 1

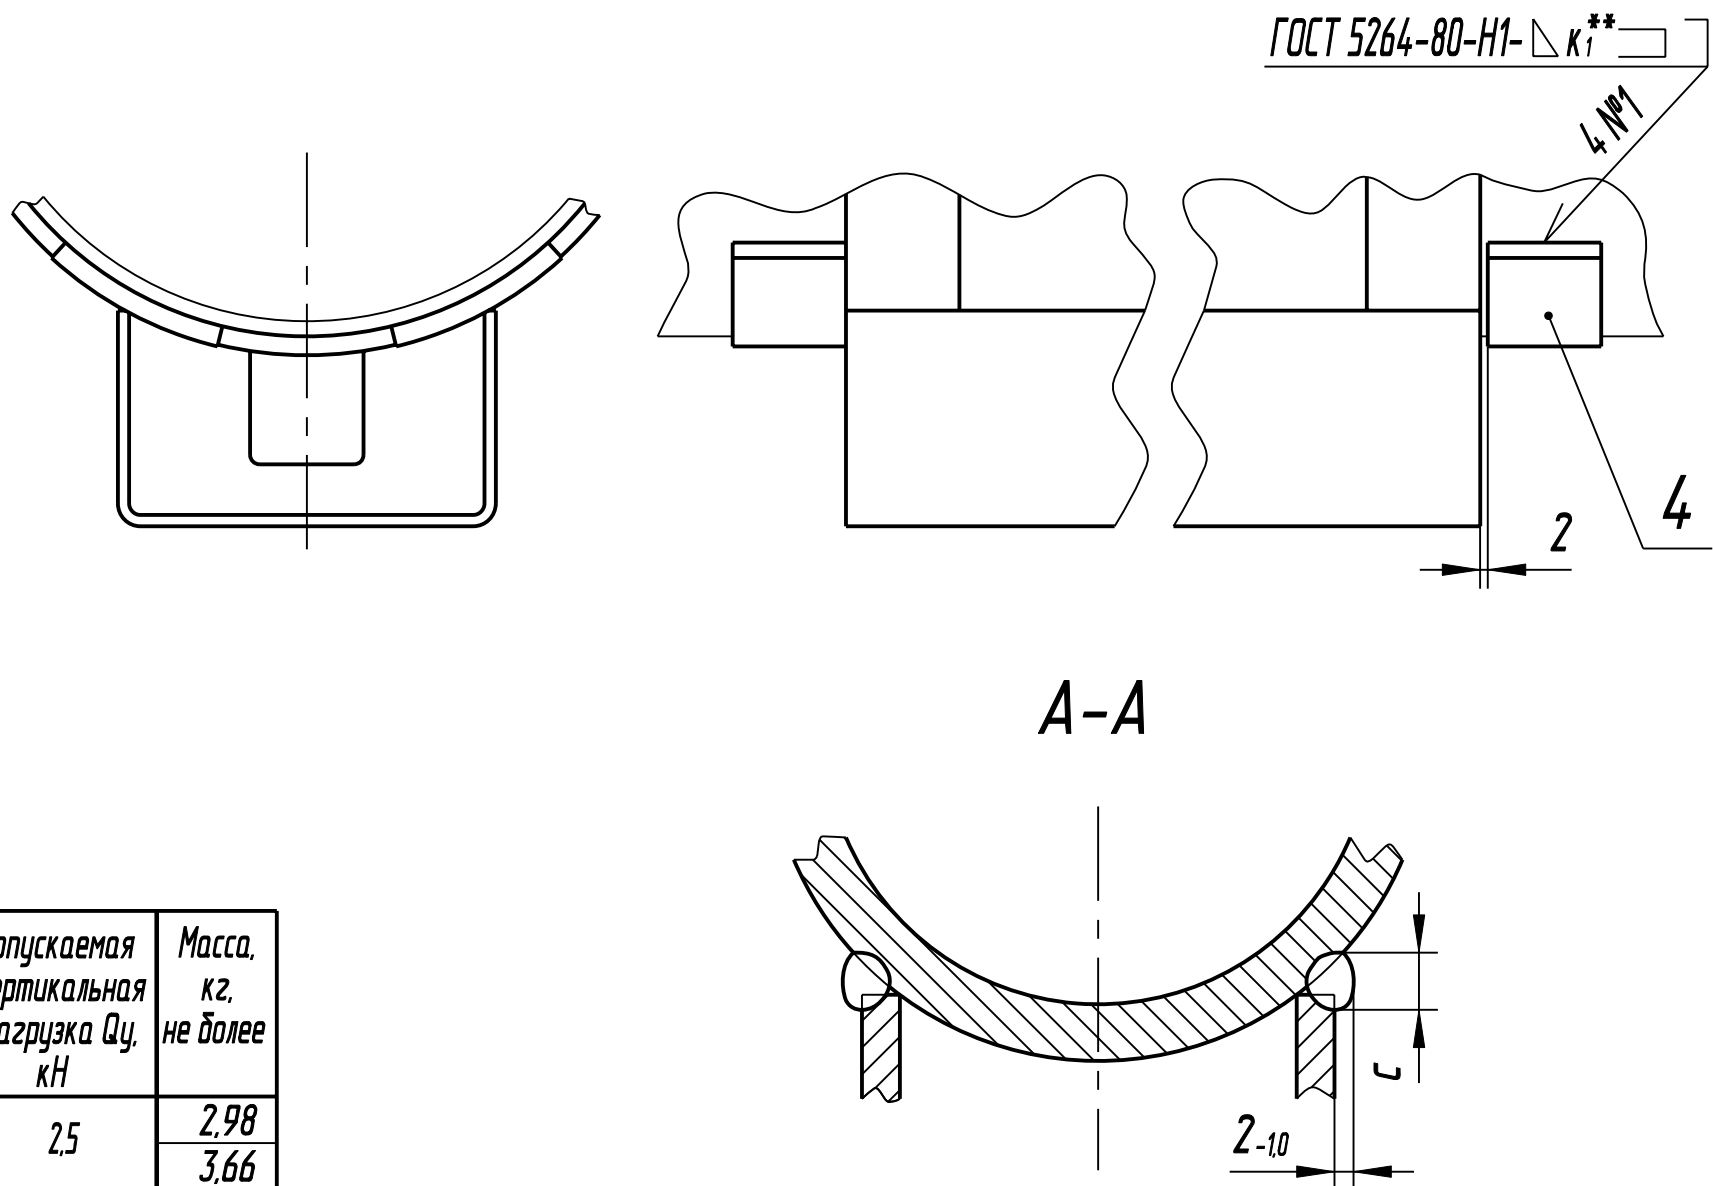

Обозначение	Рис.	Наружный диаметр трубопровода Dн*, мм	Размеры, мм						Осевое перемещение трубопровода, мм, не более	Допускаемая вертикальная нагрузка Qy, кН	Масса, кг, не более	Обозначение	Рис.	Наружный диаметр трубопровода Dн, мм	Размеры, мм						Осевое перемещение трубопровода, мм, не более	Допускаемая вертикальная нагрузка Qy, кН	Масса, кг, не более
			H*	H1*	B*	B1*	c	L*	n						H*	H1*	B*	B1*	c	L*	n		
ТПР.05.11(2).00.000			100	128								ТПР.05.11(2).00.000-28			100	128							
-01		57	150	178						2.5	4.39	-29		57	150	178							5.70
-02		76	100	138	50	160				3.0	4.54	-30		76	100	138	50	160					5.86
-03			150	188							4.67	-31		89	100	145		179					6.01
-04		89	150	195						5.0	6.01	-32			150	195							7.41
-05			100	154							8.72	-33		108	100	154		200					8.02
-06		108	150	204						6.0	8.72	-34			150	204							9.52
-07			100	167	90	250				8.0	9.52	-35		133	100	167	90	250					8.53
-08		133	150	217							10.05	-36			150	217							10.05
-09			100	180						10	16.59	-37		159	100	180		275					18.66
-10		159	150	230							20.84	-38			150	230							23.90
-11			100	210	365					25	21.46	-39		219	100	210		365					24.97
-12		219	150	260							25.69	-40			150	260							28.73
-13			100	237						40	32.68	-41		273	100	237		420					36.70
-14		273	150	287							49.25	-42			150	287							54.23
-15			100	263	200	470					53.09	-43		325	100	263	200	470					58.09
-16		325	150	313						70	62.06	-44			150	313							78.44
-17			100	289								-45		377	100	289		525					
-18		377	150	339								-46			150	339							
-19			100	313						80		-47		426	100	313		575					
-20		426	150	363								-48			150	363							
-21			100	365								-49		530	100	365		706					
-22		530	150	415	300	706				120		-50			150	415	300	706					
-23			100	415								-51		630	100	415		805					
-24		630	150	465								-52			150	465							
-25			100	460								-53		720	100	460		895					
-26		720	150	510	400	895				160		-54			150	510	400	895					
-27												-55		114	100	157		210					
												-56			150	207							
												-57		168	100	184		285					
												-58			150	234							
												-59											

Техническая характеристика

1. Опоры предназначены для крепления труб из углеродистой и низколегированной стали при строительстве технологических трубопроводов с наружным диаметром от 57 до 720 мм, транспортирующих вещества с температурой от минус 60 °С до 450 °С и условным давлением Ру до 25 МПа при температуре окружающей среды до минус 70 °С.
2. Осевое перемещение трубопровода, мм, не более см. табл.

Технические требования

1. Сварной шов №2 -сварка дуговая в защитном газе, сварочная проволока Св-08Г2С ГОСТ 2246-70.
2. Сварной шов №1 производить электродом типа Э50А ГОСТ 9467-75.
3. * Размеры для справок.
4. Н16, ± IT16/2.
5. Покрытие: грунтовка АК-070 ГОСТ 25718-83 в один слой; эмаль ХВ-16 ТУ 6-10-1301-83 в два слоя.
- Допускаются другие виды антикоррозионного покрытия согласно проекту.
6. Маркировать любым способом, обеспечивающим сохранность маркировки на весь срок эксплуатации, шрифтом не менее 5: обозначение по чертежу и товарный знак завода-изготовителя.

ТПР.05.11(2).00.000 СБ						Опора подвижная хомутовая			Лит.	Масса	Масштаб
Изм.	Лист	№ докум.	Подп.	Дата		Сборочный чертеж				См. табл.	—
Разраб.	Воронков			04.09					Лист	Листов 1	
Пров.									ОАО		
Т. контр.									ТИПРОТЮМЕННЕФТЕГАЗ		
Н. контр.	Воронков			04.09							
Утв.	Шмыговский			04.09							