


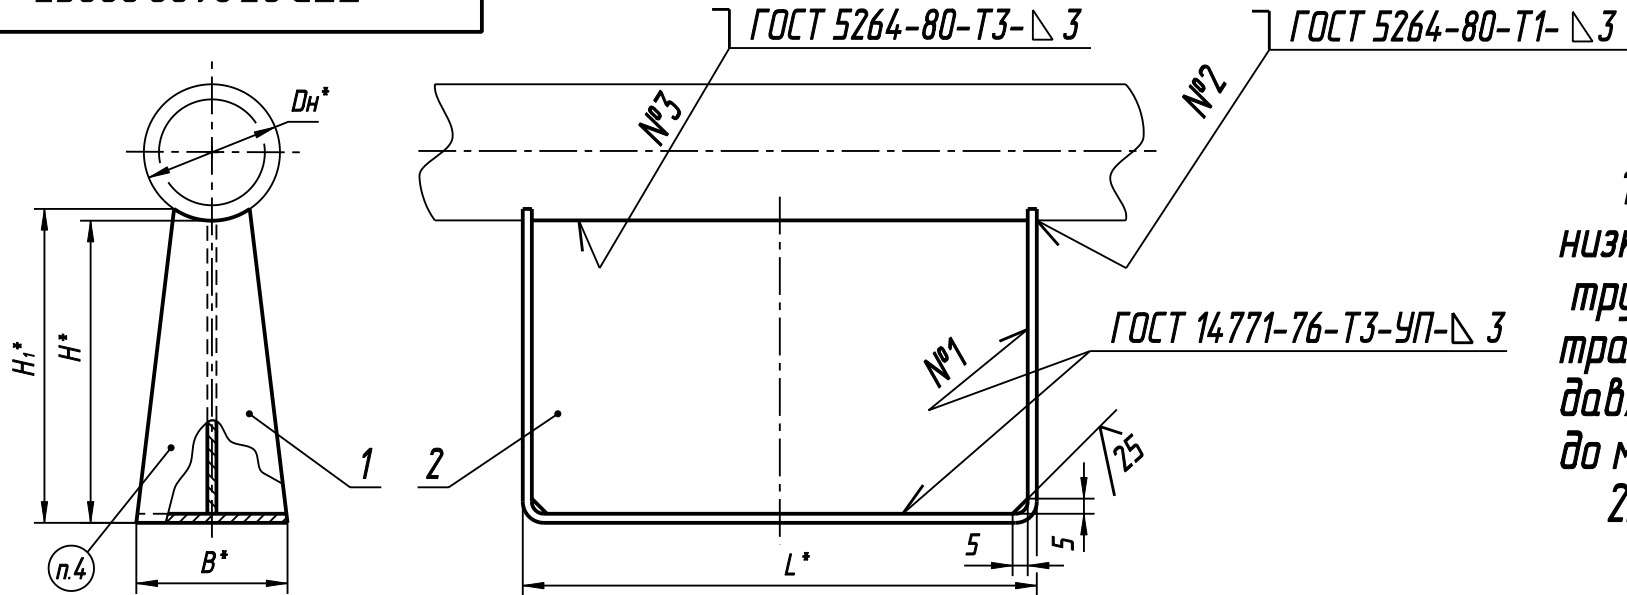

Техническая характеристика

1. Опоры предназначены для крепления труб из углеродистой и низколегированной стали при строительстве технологических трубопроводов с наружным диаметром от 32 до 168 мм, транспортирующих вещества с температурой от 0 до 450 °С и условным давлением Р_у до 25 МПа при температуре окружающей среды до минус 70 °С.
2. Осевое перемещение трубопровода не более L₁ (см. табл.).

Технические требования

1. Сварку швов №1 производить проволокой СВ-08Г2С ГОСТ 2246-70, швов №2 и №3 – электродом типа Э50А ГОСТ 9467-75.
- 2.* Размеры для справок.
3. Шерох. обраб. поверхн. дет. БЧ- $\sqrt{Ra\ 25}$, ∇ , (∇).
4. Покрытие: грунтовка АК-070 ГОСТ 25718-83 в один слой; эмаль ХВ-16 ТУ 6-10-1301-83 в два слоя.
5. Маркировать любым способом, обеспечивающим сохранность маркировки на весь срок эксплуатации, шрифтом не менее 5: товарный знак завода-изготовителя, обозначение по чертежу, заводской номер изделия.

Обозначение	Наружный диаметр трубопровода D _н *, мм	Размеры, мм					Допускаемая вертикальная нагрузка, кН	Масса, кг, не более
		H*	H ₁ *	B*	L*	L ₁		
ТПР.05.21.00.000		100	104					0,70
-01	32; 38; 45	150	154	50			1,2	0,92
-02		200	204					1,23
-03		100	108					0,89
-04	57; 76	150	158	70			2,2	1,19
-05		200	208					1,50
-06		100	113					1,10
-07	89; 108	150	163	90			4,0	1,46
-08		200	213					1,86
-09		100	118					1,34
-10	133; 159	150	168	120			8,0	1,83
-11		200	218					2,26
-12		100	104					1,28
-13	32; 38; 45	150	154	50			1,2	1,74
-14		200	204					2,20
-15		100	108					1,55
-16	57; 76	150	158	70			2,2	2,06
-17		200	208					2,54
-18		100	113					1,84
-19	89; 108	150	163	90			4,0	2,39
-20		200	213					2,98
-21		100	118					2,25
-22	133; 159	150	168	120			8,0	2,89
-23		200	218					3,54
-24		100	116					1,22
-25	114	150	166	100			4,0	1,53
-26		200	216					1,84
-27		100	120					1,97
-28	168	150	170	130			10,0	2,87
-29		200	220					3,77

ТПР.05.21.00.000СБ					Опора скользящая D _н 32-168 мм Сборочный чертеж		
Изм.	Лист	№ докум.	Подп.	Дата	Лит.	Масса	Масштаб
Разраб.	Воронков			11.05		См. табл.	-
Пров.							
Т.контр.					Лист	Листов 1	
Н.контр.	Воронков			11.05	ОАО ТИПРОТЮМЕННЕФТЕГАЗ		
Утв.	Щербинин			11.05			