




Инв. № подл.

Взам. инв. №

Инв. № дубл.

Подпись и дата

ТПР.05.27(1).00.000СБ

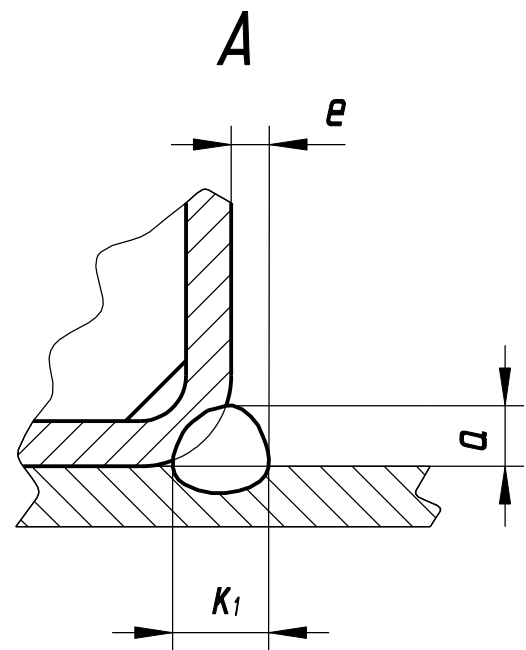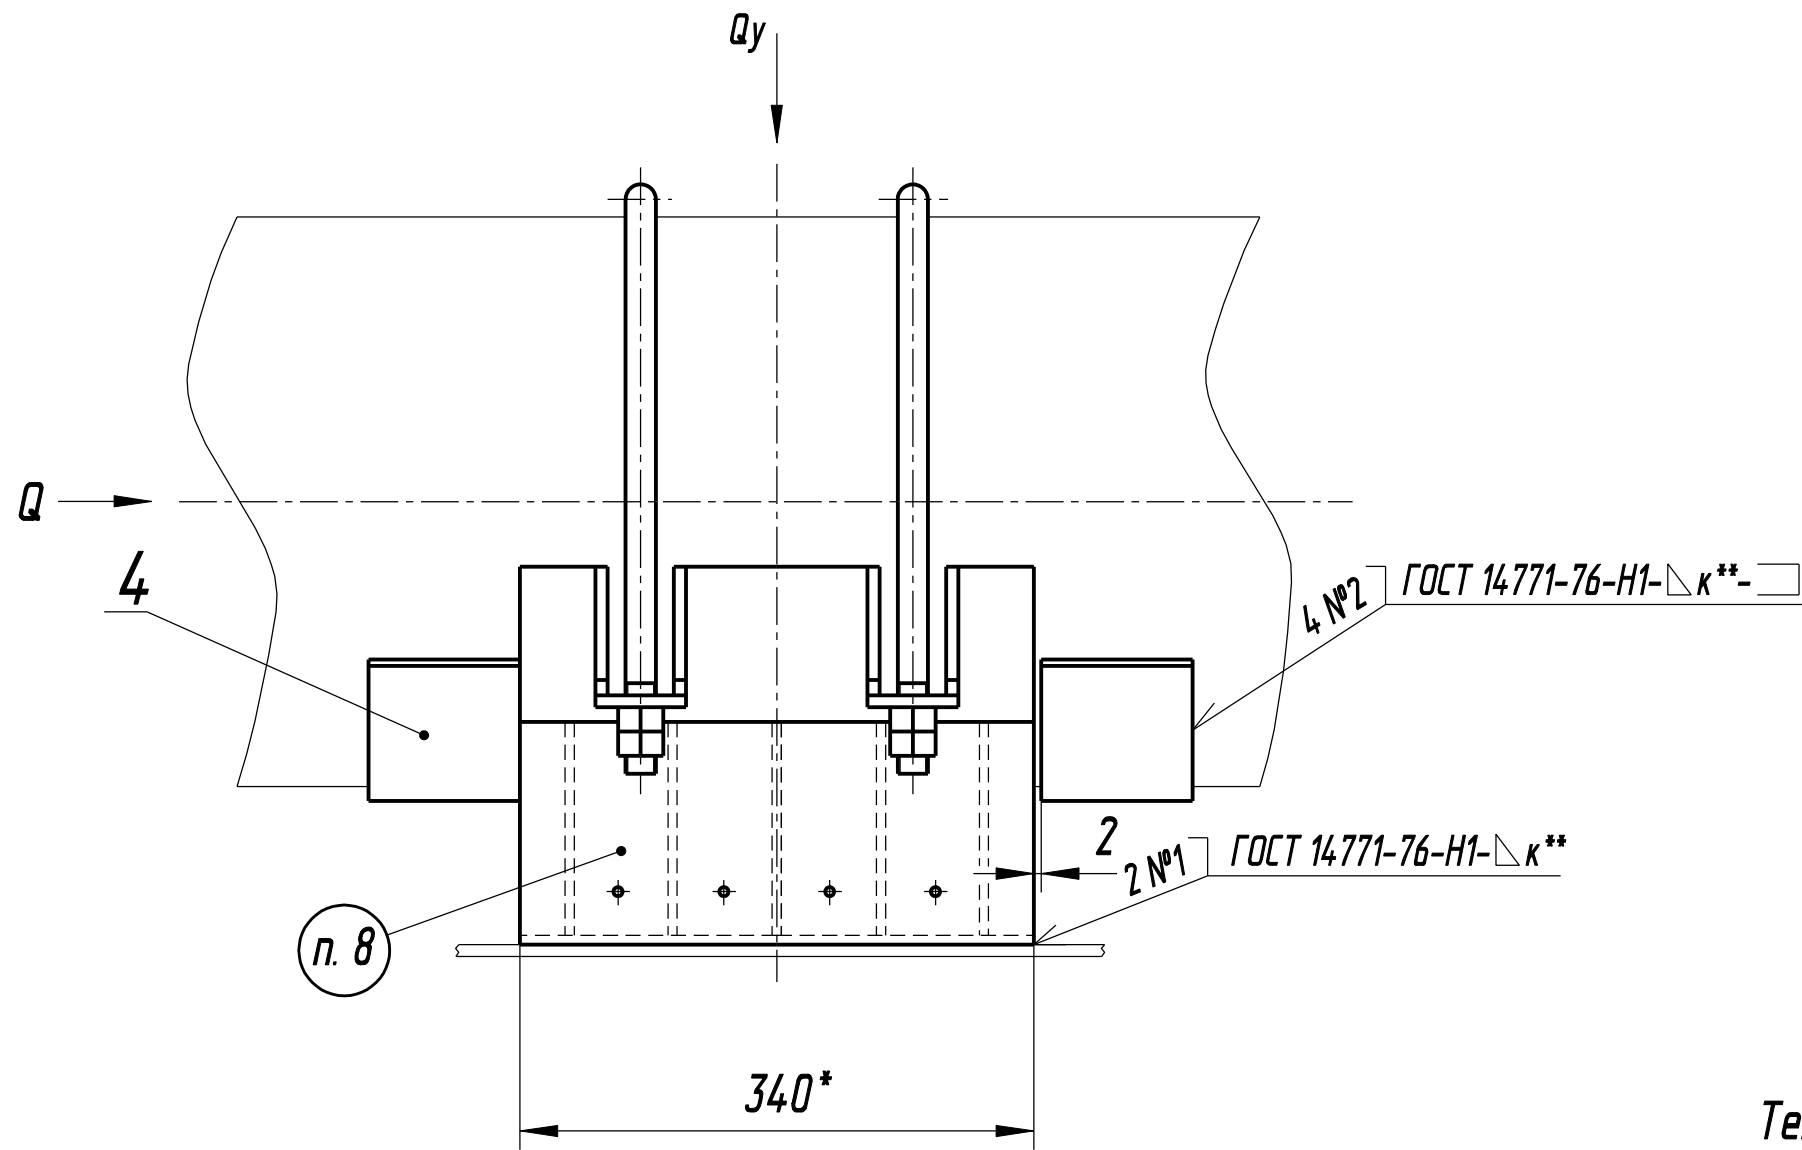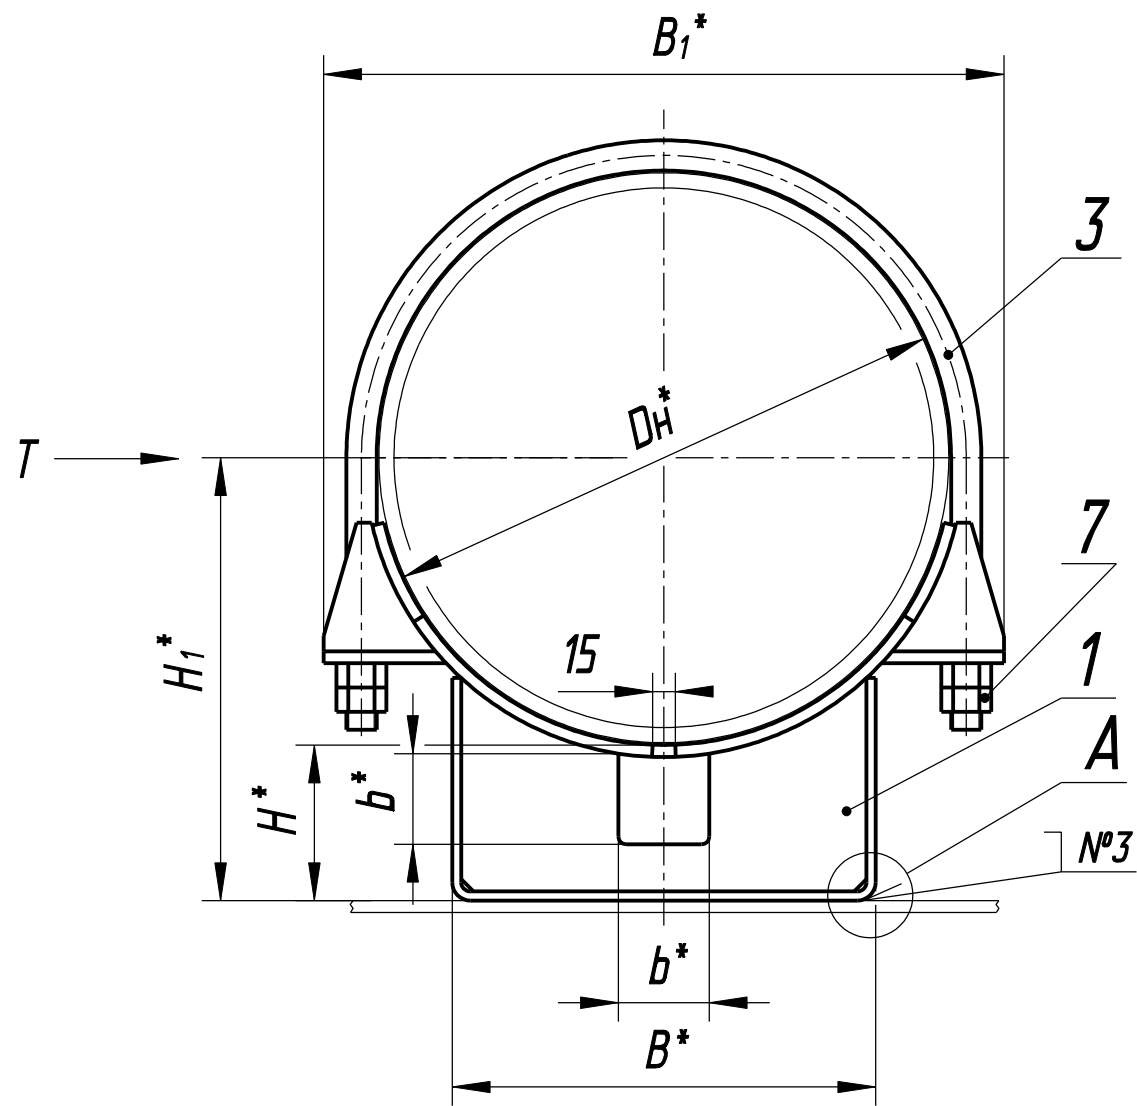

Техническая характеристика

1. Опора предназначена для крепления труб из углеродистой и низколегированной стали при строительстве технологических трубопроводов с наружным диаметром от 57 до 377 мм, транспортирующих вещества с температурой от минус 30 до 300 °С и номинальным давлением PN до 50 МПа при температуре окружающей среды до минус 70 °С.
2. Величины осевых и боковых допускаемых расчётных нагрузок заданы при условии отсутствия внешних изгибающих моментов.

Технические требования

1. * Размеры для справок.
2. ** к – по наименьшей толщине свариваемых деталей.
3. Н16, ±IT16/2.
4. Сварочная проволока Св-08Г2С ГОСТ 2246-70.
5. Шов N°3- сварка дуговая в защитном газе.
6. Допускается применение сварки ручной дуговой электродом типа Э50А ГОСТ 9467-75.
7. Покрытие: грунтровка АК-070 ГОСТ 25718-83 в один слой; эмаль ХВ-16 ТУ 6-10-1301-83, VI. ХЛ1 в два слоя.
- Допускаются другие виды антикоррозионного покрытия согласно проекту.
8. Маркировать любым способом, обеспечивающим сохранность маркировки на весь срок эксплуатации, шрифтом не менее 5: обозначение по чертежу и товарный знак завода-изготовителя.

Обозначение	Наружный диаметр трубопровода Dн*, мм	Размеры, мм								Допускаемые нагрузки, кН			Масса, кг, не более
		H*	H1*	B*	B1*	b*	κ1	a	e	Вертикаль-ная, Qy	Осевая, Q	Боковая, T	
ТПР.05.27(1).00.000	57	100	130	50	90	30	7 ^{+2,0} _{-1,0}	6 ^{+2,0} _{-1,0}	3 ^{+1,0} _{-0,5}	2,5	15	5	4,96
-01		150	180										6,28
-02		200	230										7,74
-03	76	100	138	50	108	30	7 ^{+2,0} _{-1,0}	6 ^{+2,0} _{-1,0}	3 ^{+1,0} _{-0,5}	3,0	20	8	5,29
-04		150	188										6,71
-05		200	238										8,07
-06	89	100	145	50	128	30	7 ^{+2,0} _{-1,0}	6 ^{+2,0} _{-1,0}	3 ^{+1,0} _{-0,5}	5,0	20	8	5,61
-07		150	195										7,0
-08		200	245										8,40
-09	108	100	154	50	150	30	7 ^{+2,0} _{-1,0}	6 ^{+2,0} _{-1,0}	3 ^{+1,0} _{-0,5}	6,0	50	20	10,26
-10		150	204										12,13
-11		200	254										14,19
-12	133	100	165	50	170	30	7 ^{+2,0} _{-1,0}	6 ^{+2,0} _{-1,0}	3 ^{+1,0} _{-0,5}	8,0	60	20	11,10
-13		150	215										12,76
-14		200	265										14,73
-15	159	100	180	50	200	30	7 ^{+2,0} _{-1,0}	6 ^{+2,0} _{-1,0}	3 ^{+1,0} _{-0,5}	10	60	20	12,27
-16		150	230										13,93
-17		200	280										14,73
-18	194	100	197	50	250	30	7 ^{+2,0} _{-1,0}	6 ^{+2,0} _{-1,0}	3 ^{+1,0} _{-0,5}	20	120	50	25,54
-19		150	247										32,15
-20		200	297										36,88
-21	219	100	210	50	275	30	7 ^{+2,0} _{-1,0}	6 ^{+2,0} _{-1,0}	3 ^{+1,0} _{-0,5}	25	160	100	27,76
-22		150	260										32,57
-23		200	310										37,35
-24	273	100	237	50	340	30	7 ^{+2,0} _{-1,0}	6 ^{+2,0} _{-1,0}	3 ^{+1,0} _{-0,5}	40	240	150	30,28
-25		150	287										37,41
-26		200	337										42,20
-27	325	100	263	50	395	30	7 ^{+2,0} _{-1,0}	6 ^{+2,0} _{-1,0}	3 ^{+1,0} _{-0,5}	50	300	200	36,05
-28		150	313										39,38
-29		200	363										43,87
-30	377	100	289	50	450	30	7 ^{+2,0} _{-1,0}	6 ^{+2,0} _{-1,0}	3 ^{+1,0} _{-0,5}	70	380	200	40,45
-31		150	339										44,18
-32		200	389										48,32

					ТПР.05.27(1).00.000СБ						
					Опора неподвижная хомутовая трубопроводов Dн 57-377мм, PN 50 МПа Сборочный чертеж			Лит.	Масса	Масштаб	
Изм.	Лист	№ докум.	Подп.	Дата						См. табл.	-
Разраб.	Воронков			06.14							
Пров.											
Т. контр.							Лист	Листов 1			
Н. контр.	Воронков			06.14				ОАО "ТИПРОТЮМЕННЕФТЕГАЗ"			
Утв.	Уржумова			06.14							