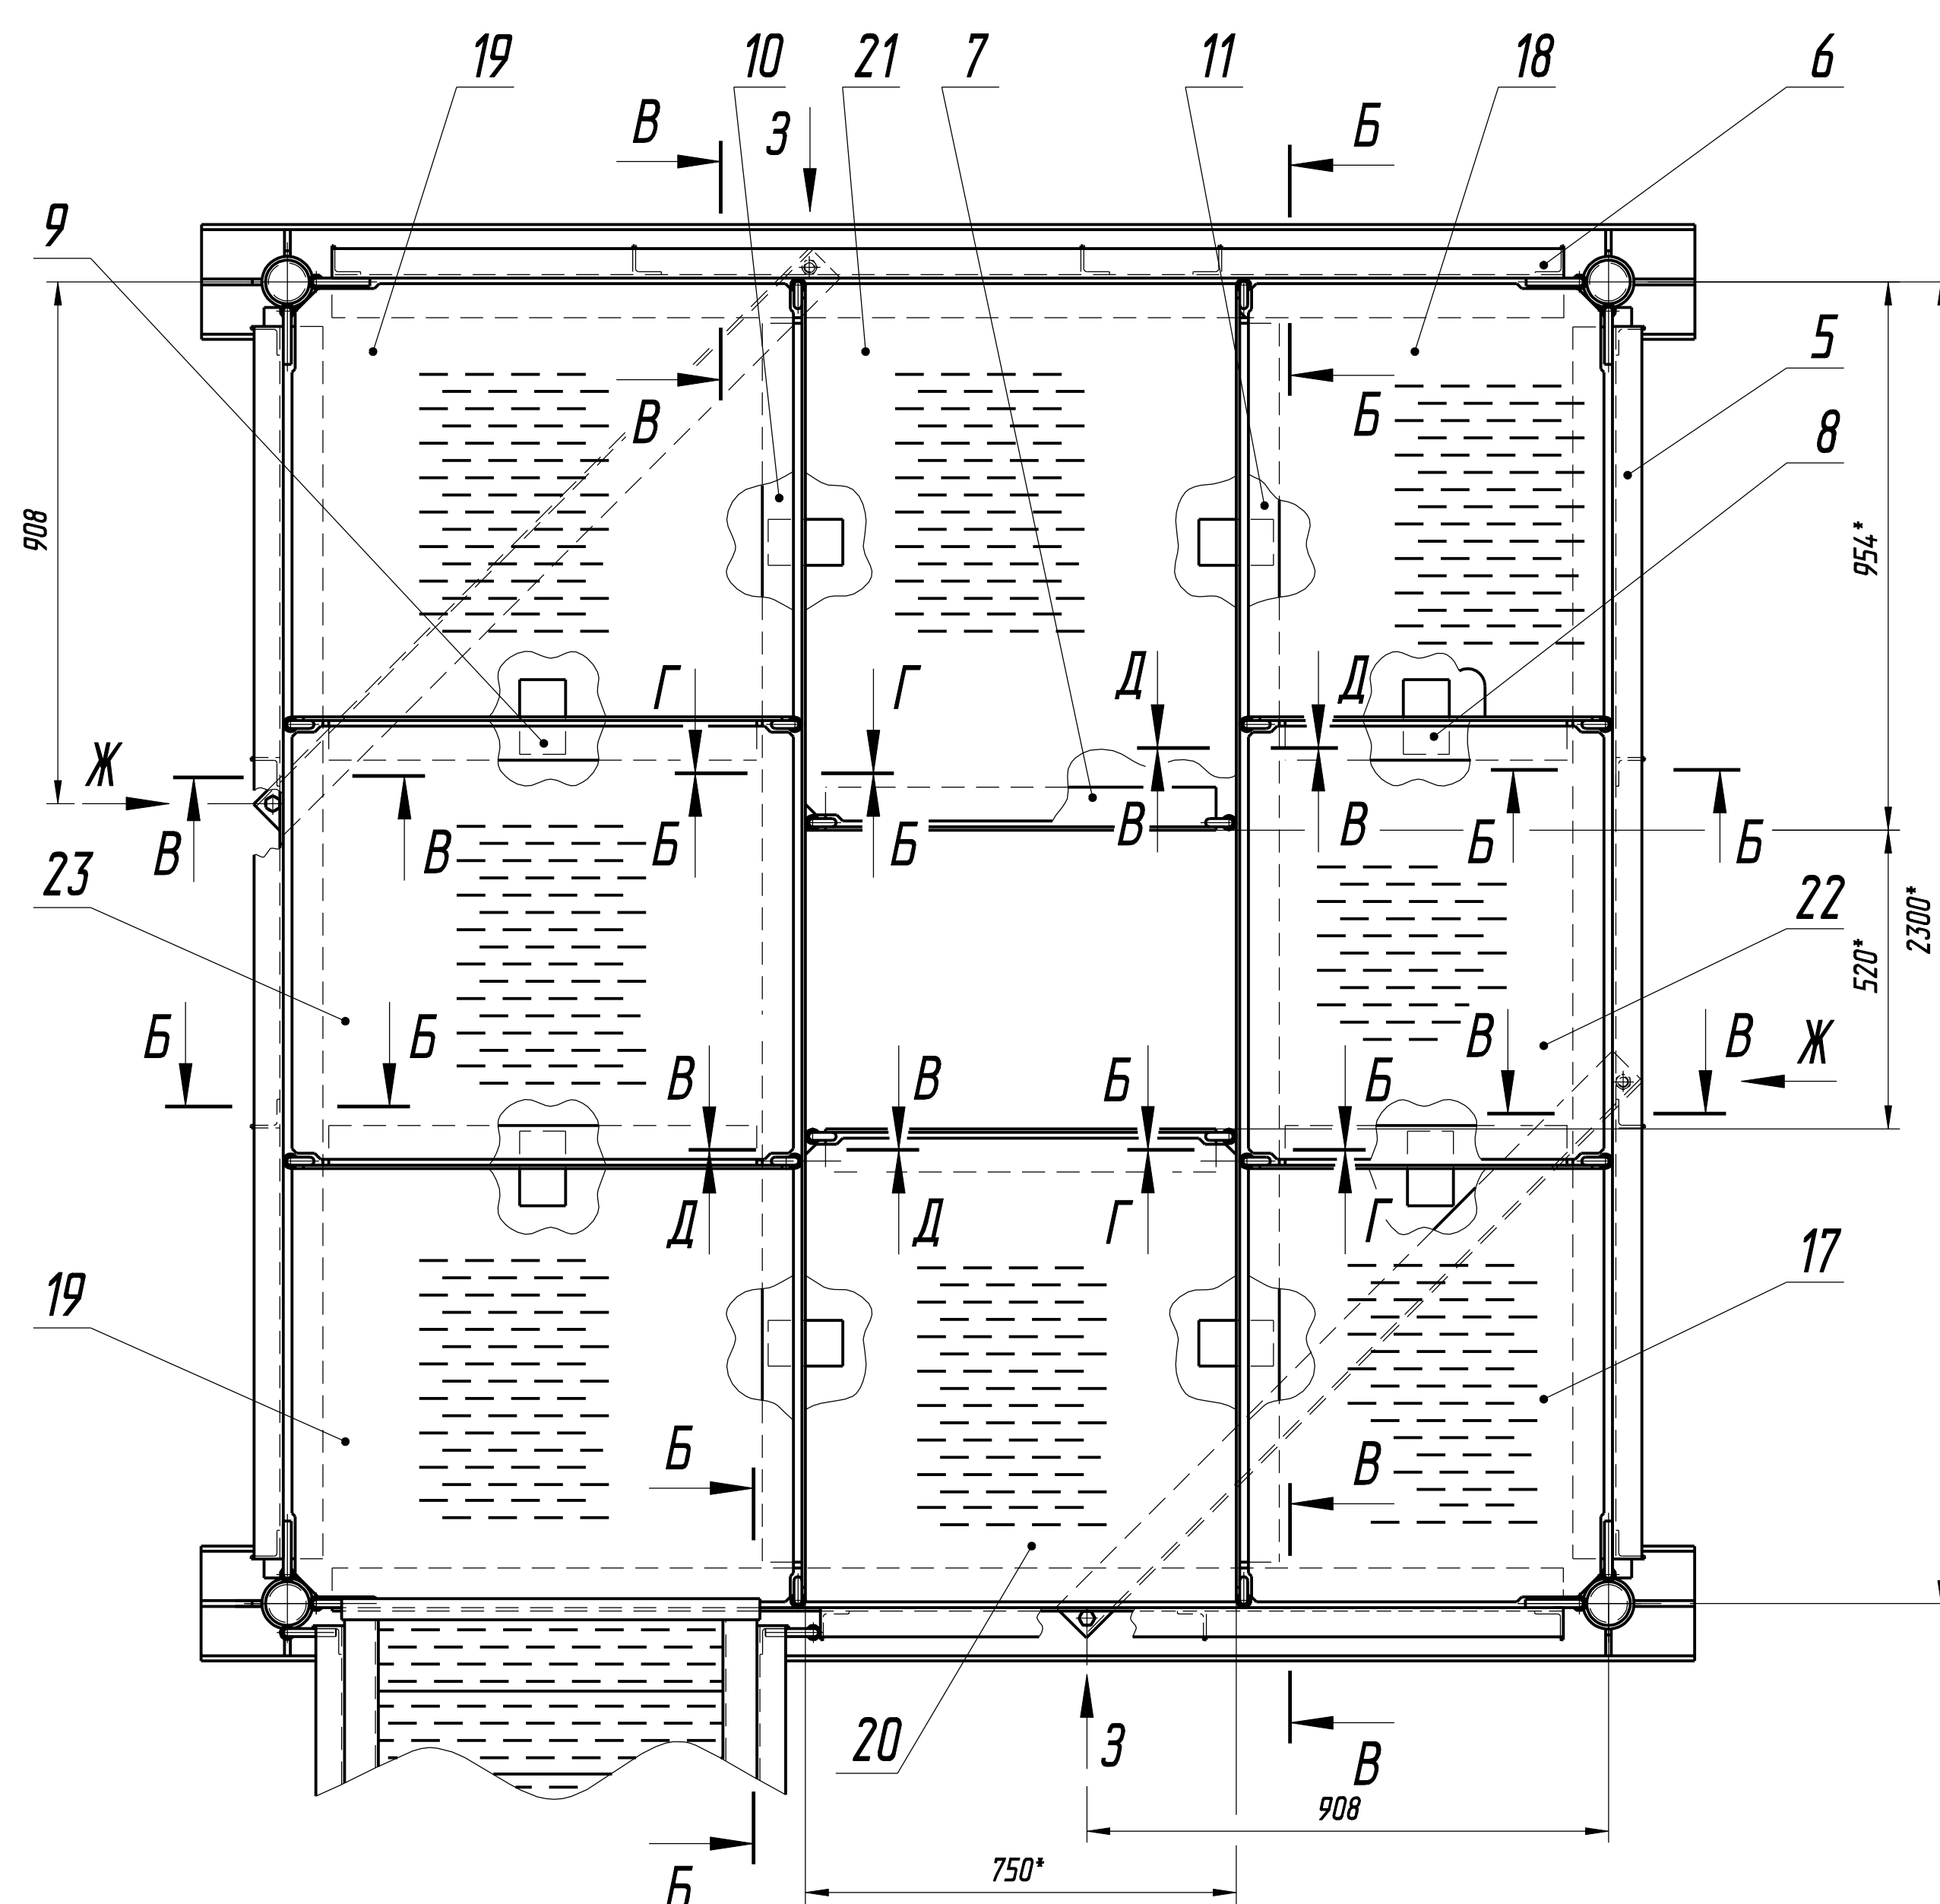
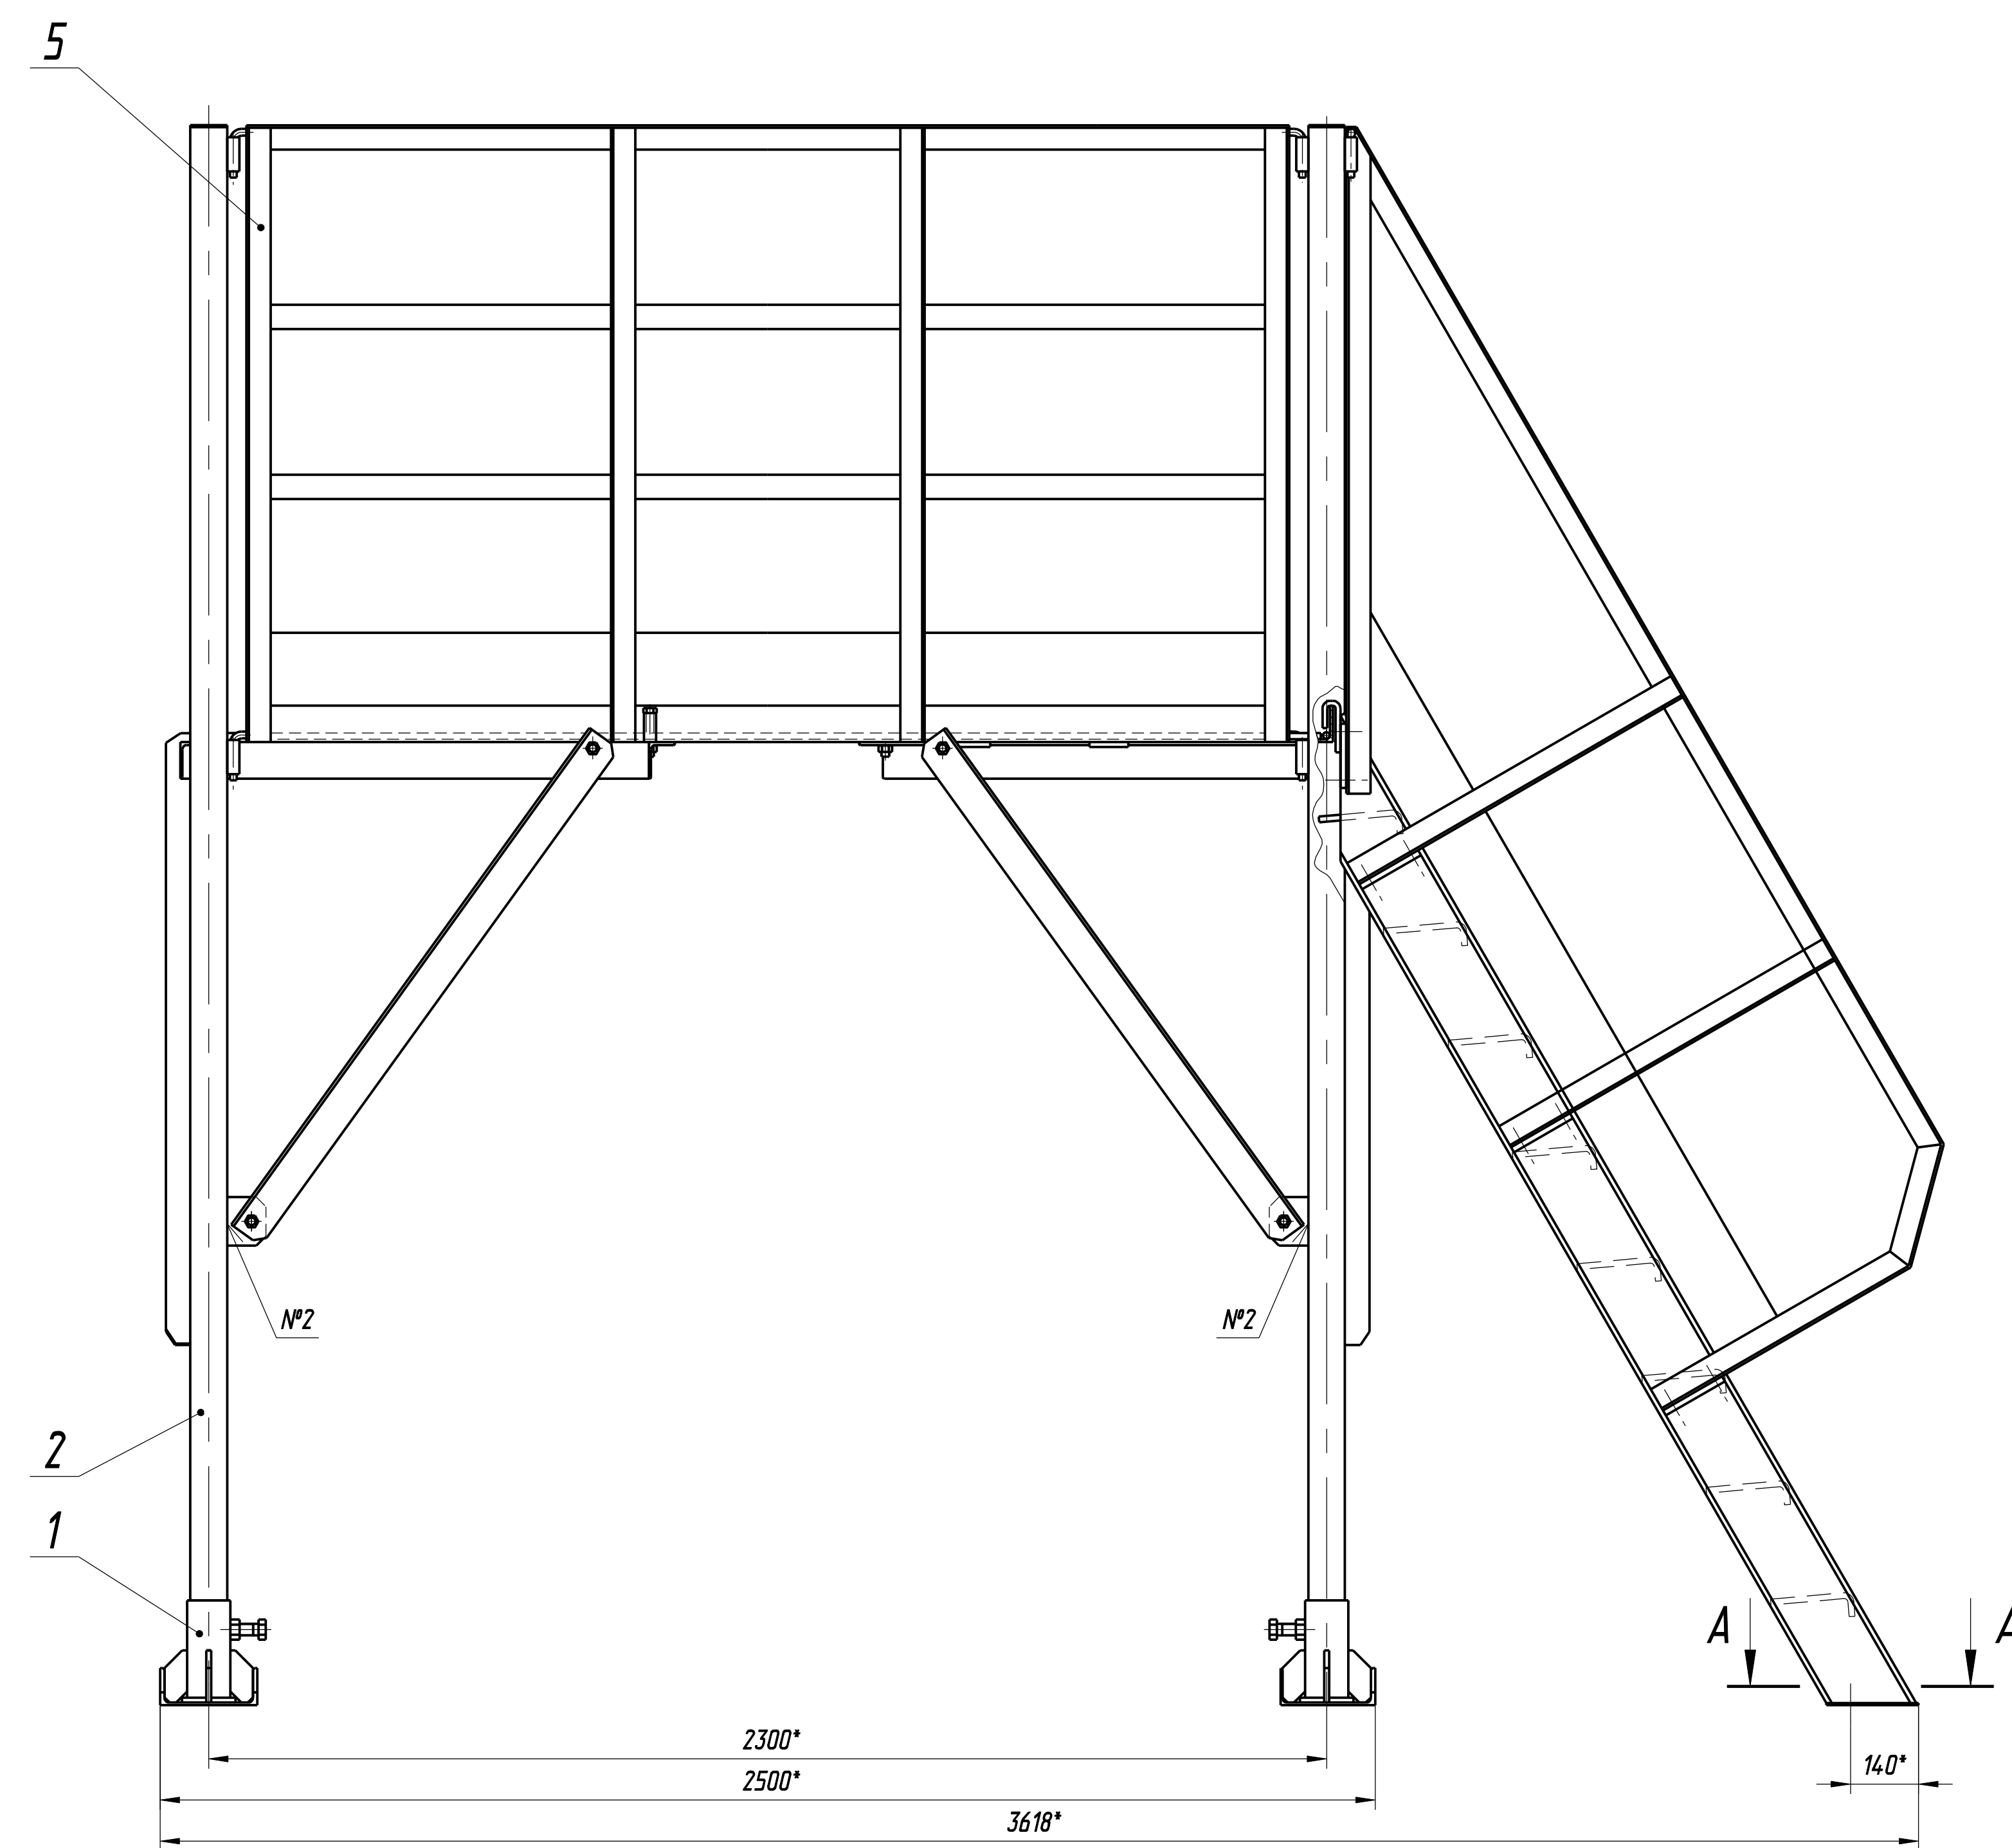


1. Климатическое исполнение и категория размещения по ГОСТ 15150-69 ХЛ1

Технические требования

1. *Размеры для справок.
2. *ИП16/2.
3. Сварку производить проволокой Св-08Г2 ГОСТ 2246-70
4. Сварка дуговая в защитном газе
5. Шероховатость поверхности Дет. Б4 - $\sqrt{Ra\ 25}$ $\sqrt{(\sqrt{ })}$
7. Покрытие: грунтровка ХС-010 ТУ 6-51-51-90 в один слой, эмаль ХВ-124 серая
ГОСТ 1014-89 в два слоя. VII ХЛ1
Допускается другое видо антикоррозионного покрытия согласно проекту.

[illegible]