

Инв. № подл.

Подп. и дата

Взам. инв. №

Инв. № дубл.

Подп. и дата

Спраб. №

9 9 61-606'5 ындэз 71-000 00 779-71 75

1 : 5

1

2

3

4

6

7

5

8

11

9

12

10

50

928

523

105

200

128

R30


A-A

ТЗ K 4 места

φ 12

φ 10

φ 30

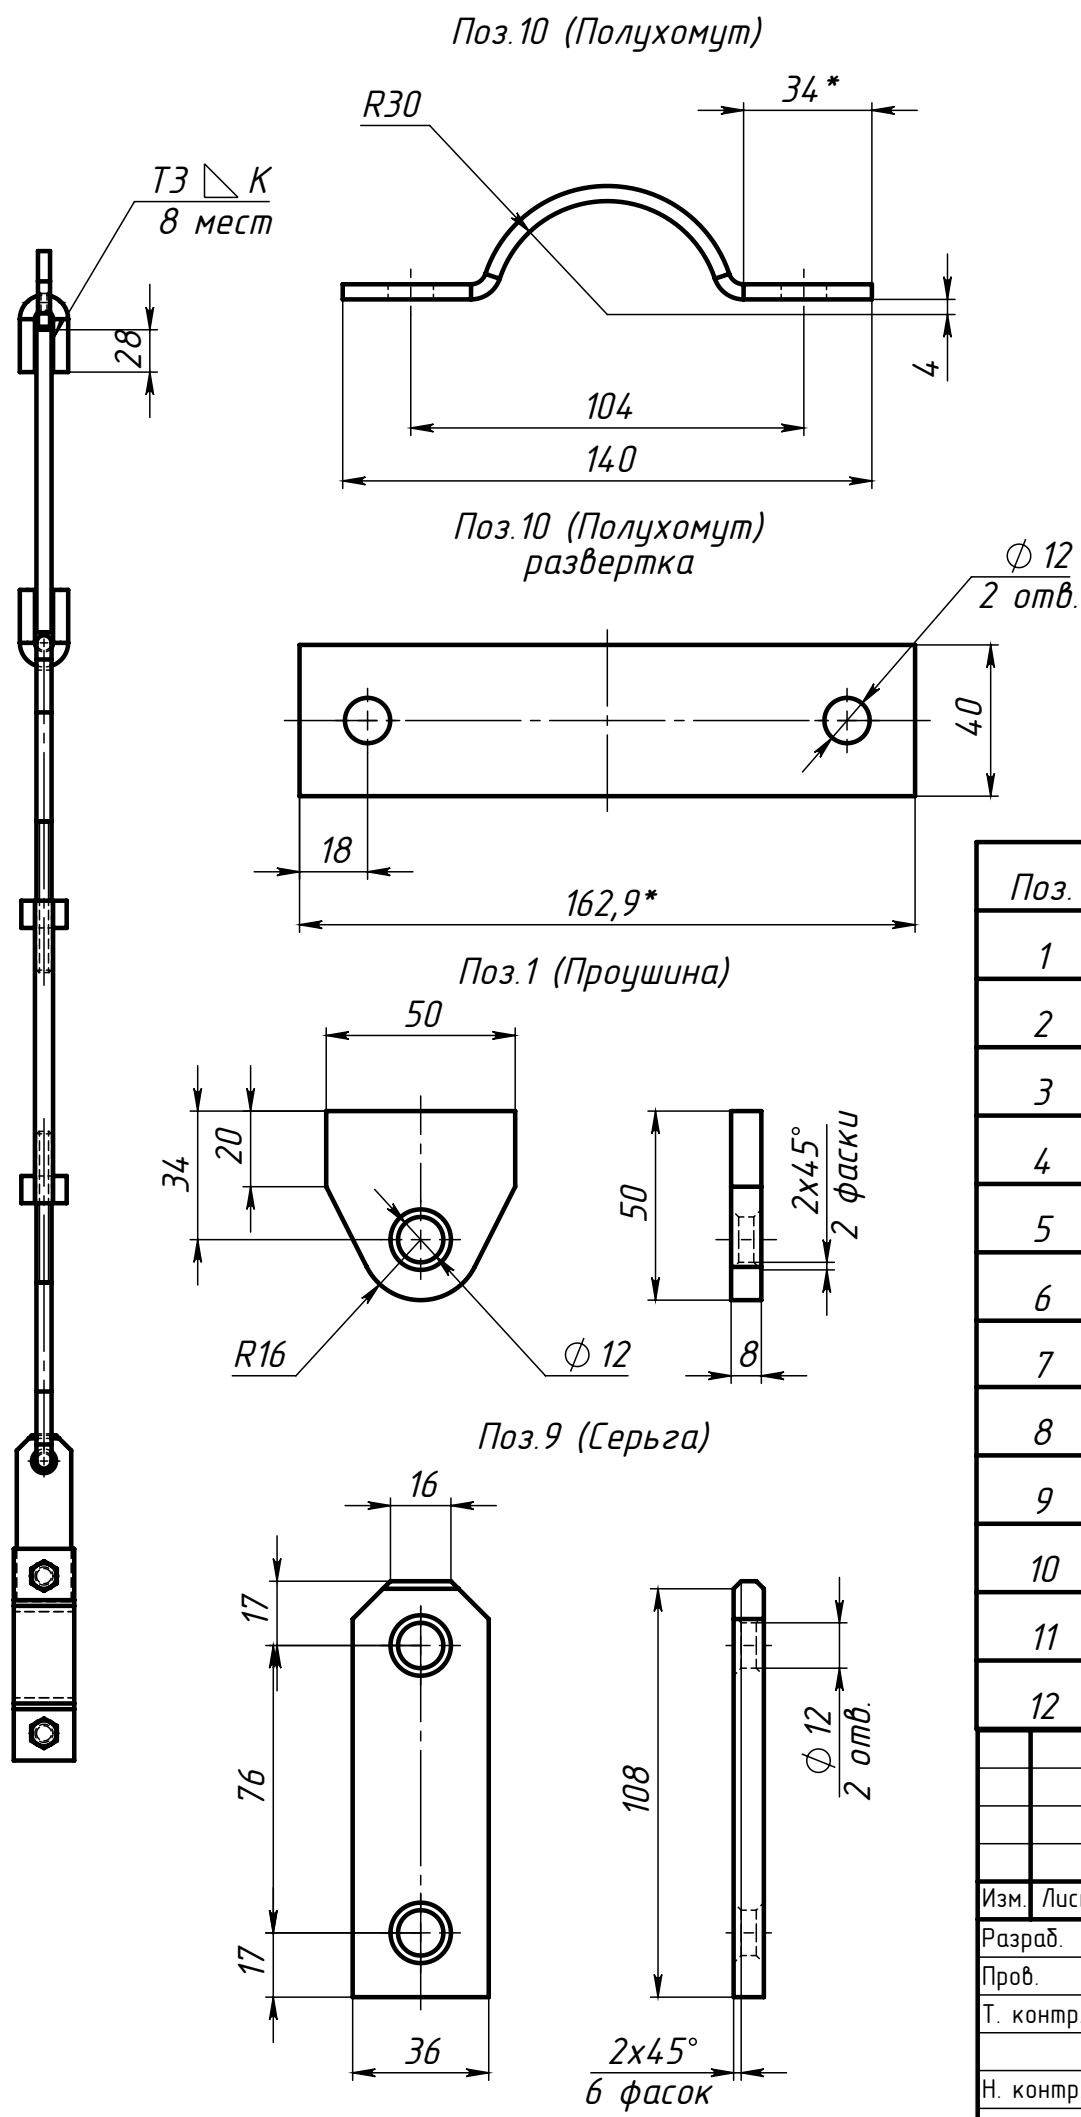

Поз.	Обозначение	Наименование	Вес	К-во
1	50x50x8	Проушина	0.12	1
2	φ10x105	Ушко	0.06	4
3	φ10x200	Тяга гладкая	0.12	1
4	M10x200	Шпилька левая	0.12	1
5	φ30x18, M10	Гайка	0.09	1
6	φ30x18, M10	Гайка левая	0.09	1
7	φ12x200	Пруток	0.18	2
8	M10x200	Шпилька	0.12	1
9	110x38x8	Серьга	0.23	1
10	163x40x4	Полухомут	0.20	2
11	Болт M10x35 ГОСТ 7798-70		0.0339	2
12	Гайка M10 ГОСТ 5915-70		0.011	4

57 ТС-677.00.000-12 серия 5.903-13 в.6				
Изм.	Лист	№ докум.	Подп.	Дата
Разраб.				
Пров.				
Т. контр.				
Н. контр.				
Утв.				
Подвеска жесткая горизонтальных трубопроводов			Лит.	Масса
09Г2С ГОСТ 4543-71			Лист 1	Листов 1
			000 "ЗМП"	
			Масштаб	1:2

Копировал

Формат А3

Файл: 57 ТС-677.00.000-12 Конфигурация: 00