


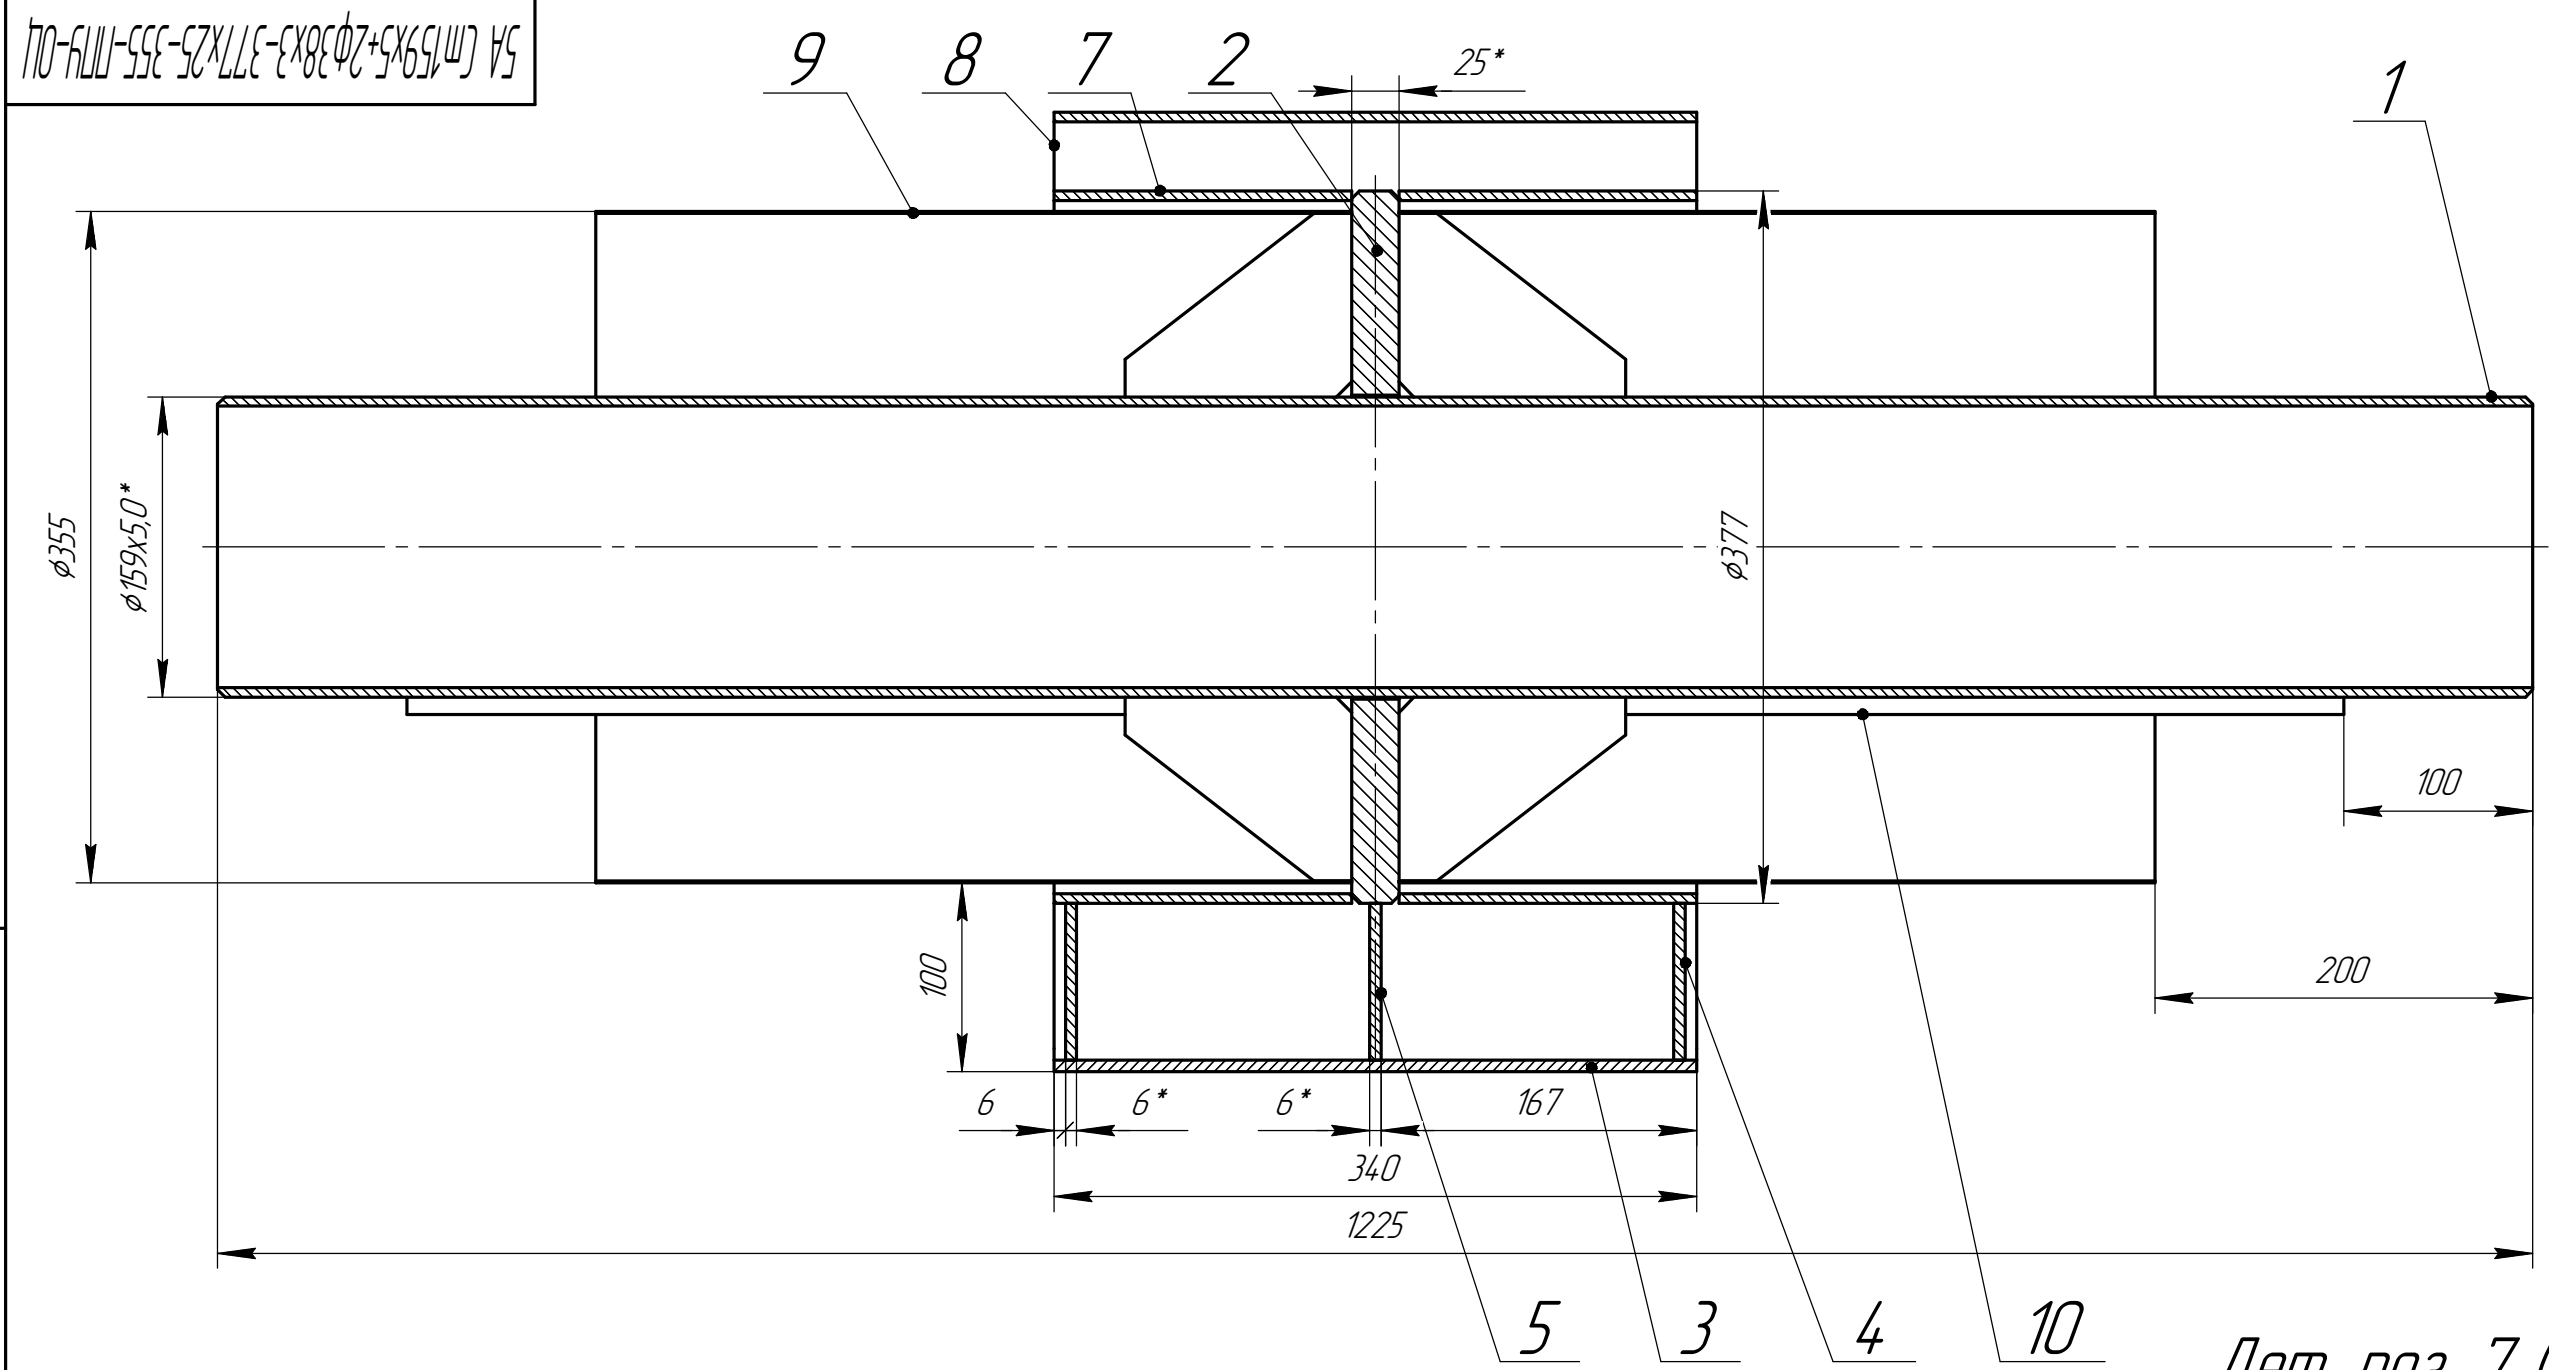


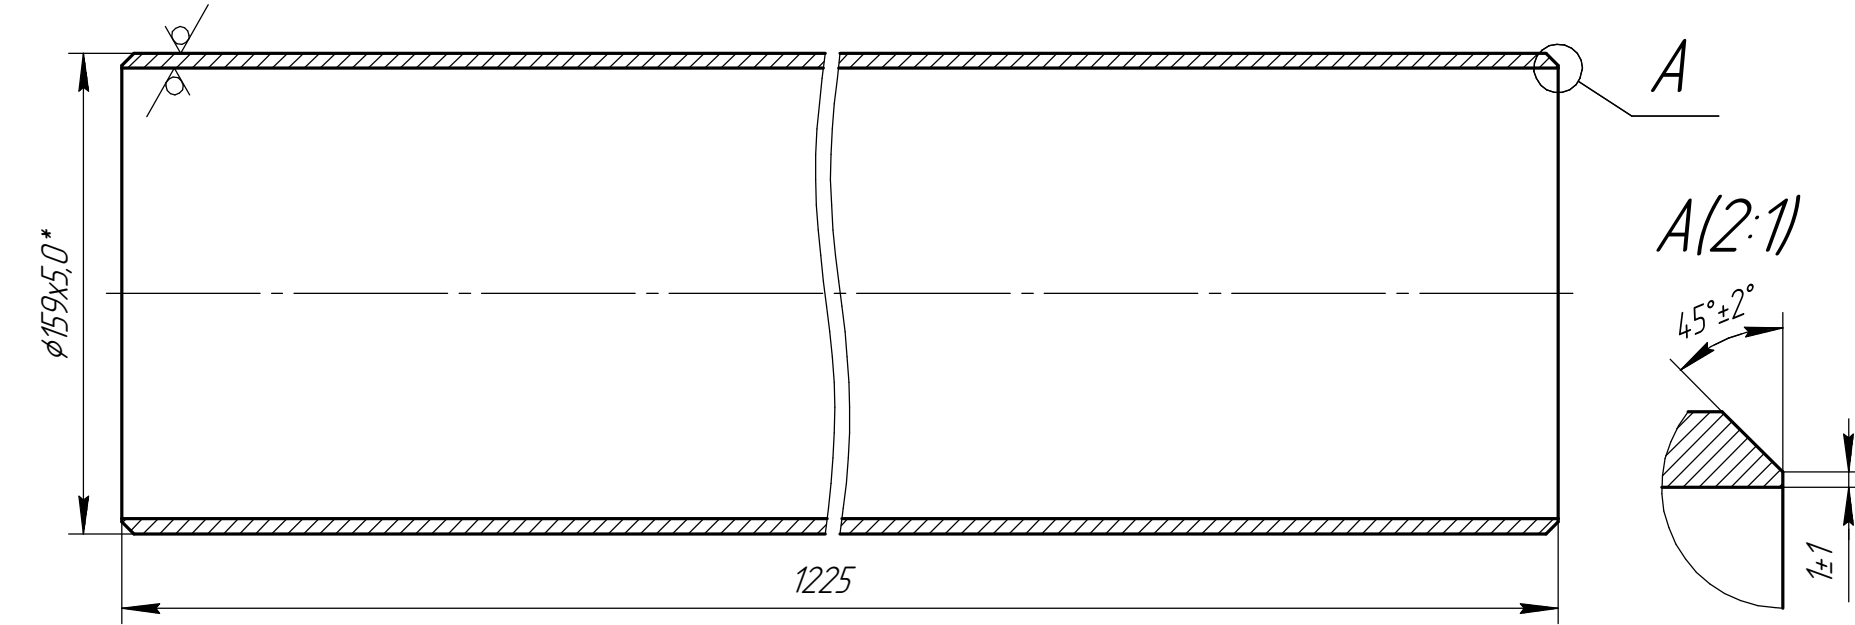


Дет. поз. 1 (1:2,5)

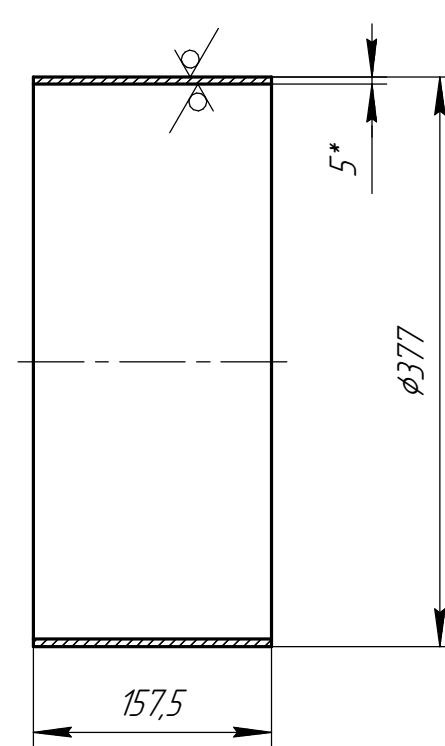



$A(2:1)$

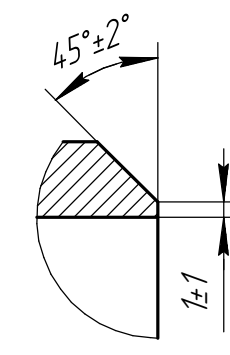


Q_→(1:5)

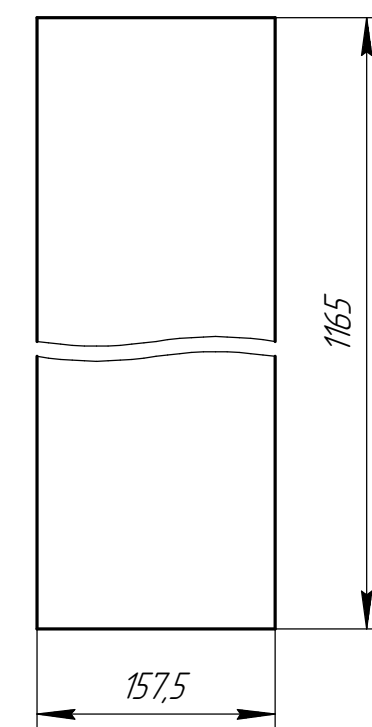


Дет. поз. 5

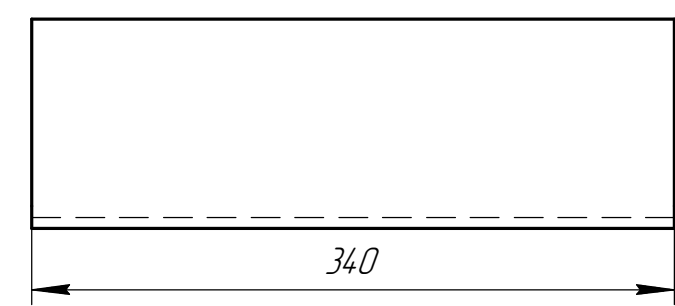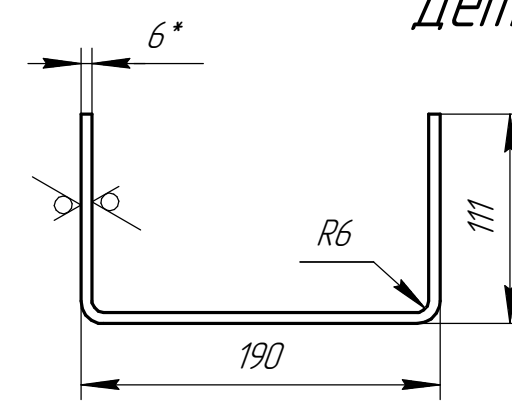


Q₂ (1:10)

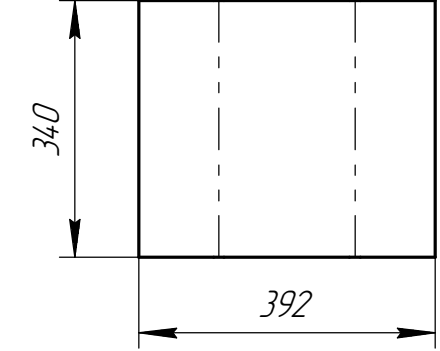


Дет. поз. 10 (1:2)

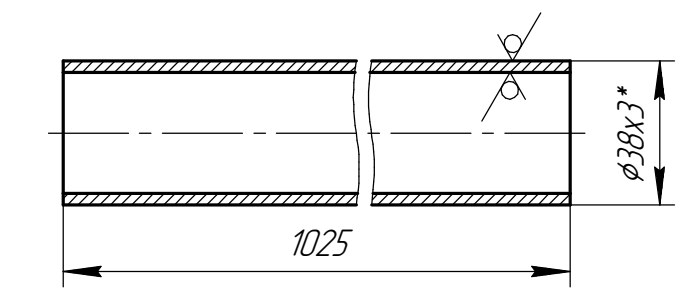


Дет. поз. 6 (1:2)

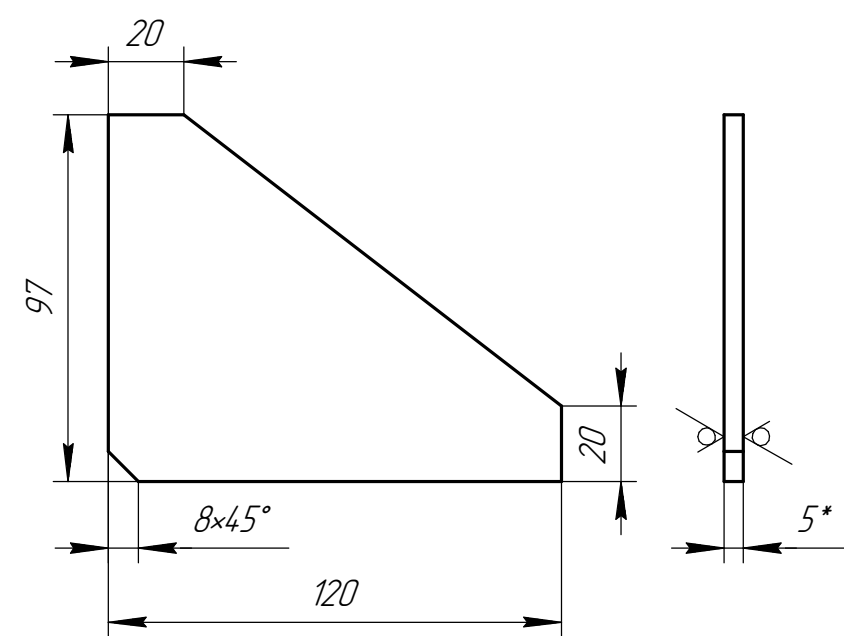


Дет. поз. 9 (1:5)

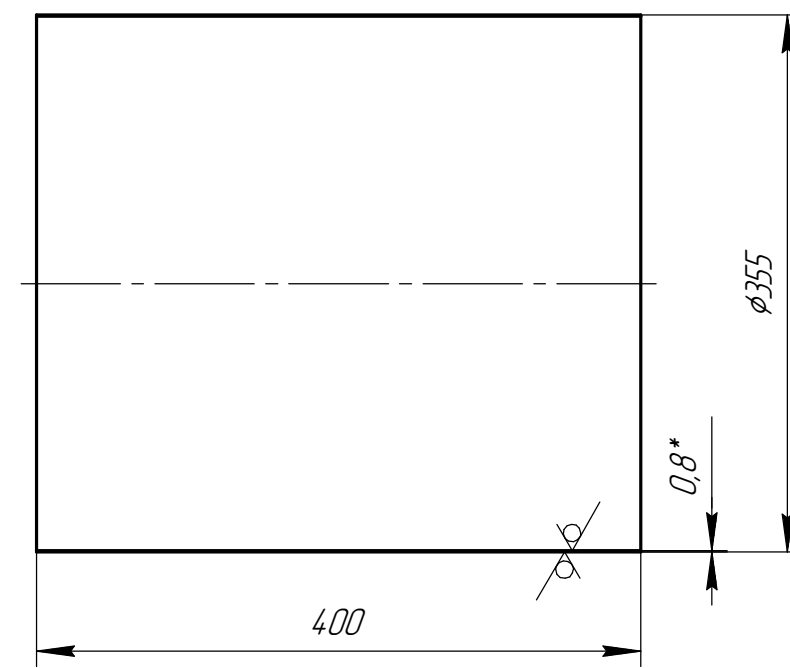


Q₂ (1:10)

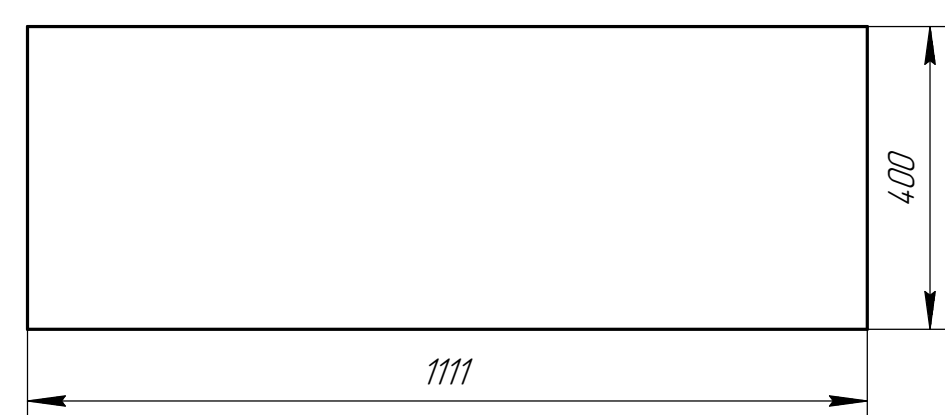


Дет. поз. 4 (1:2)

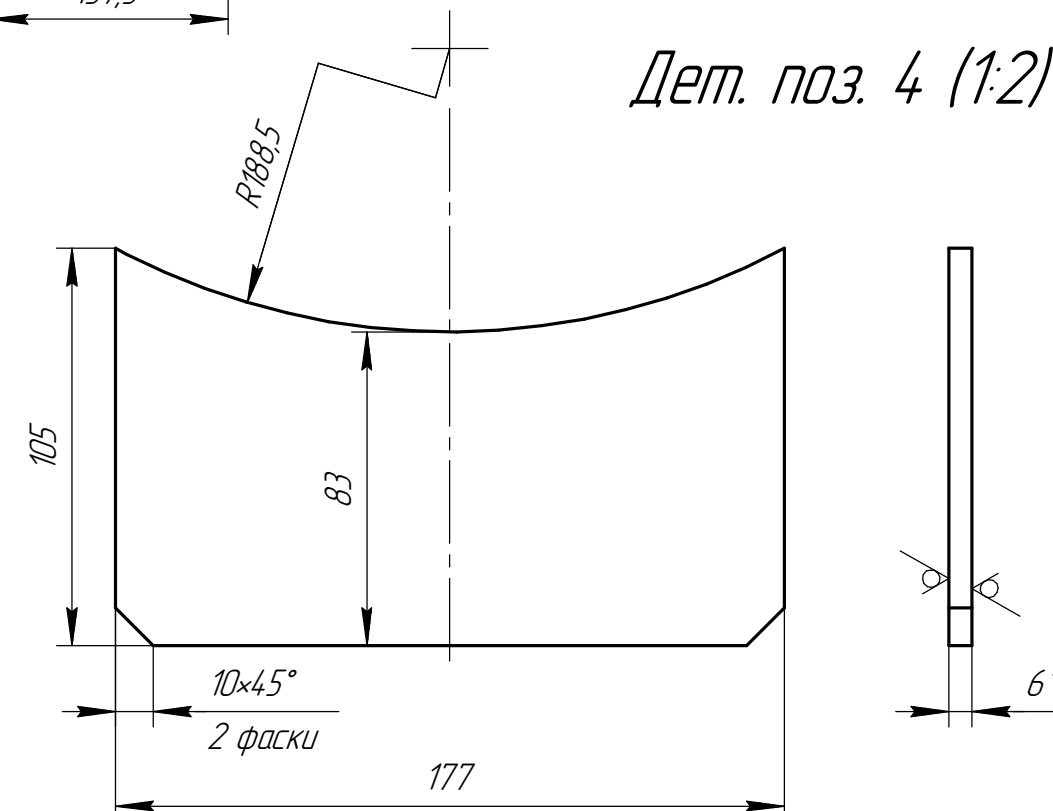


Дет. поз. 5 (1:2)

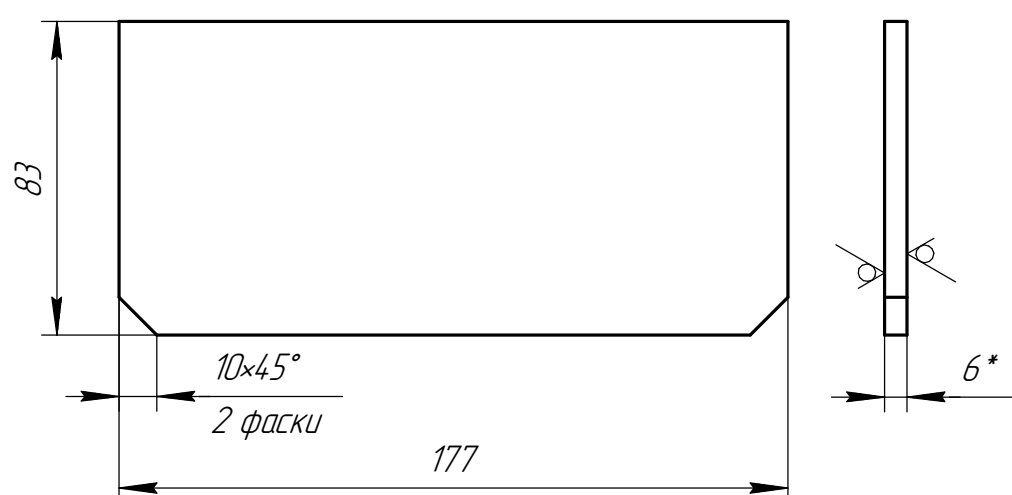

Дет. поз. 8 (1:5)

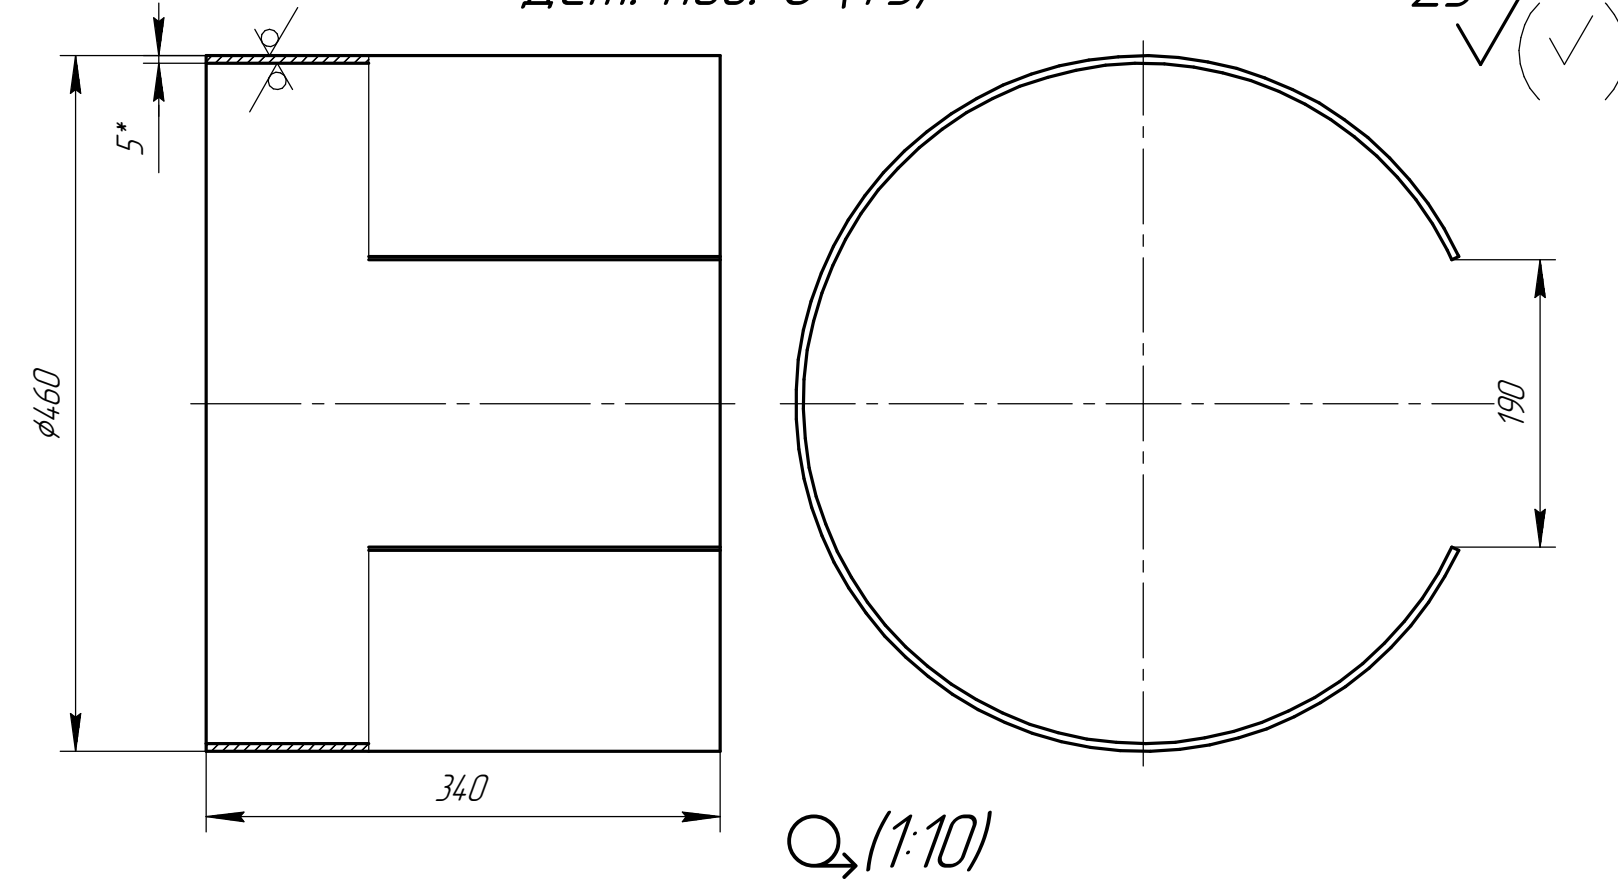

Q₂ (1:10)

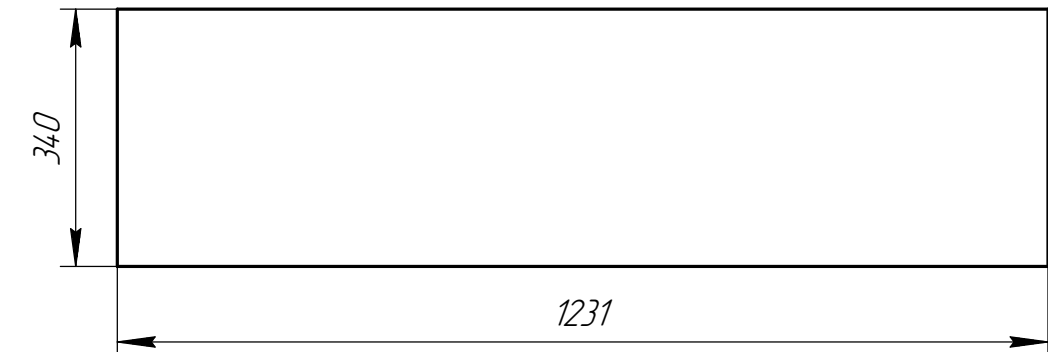

1. Общие допуски по ГОСТ 30893.1: H17, h17, ±IT17/2.
2. *Размеры для справок.
3. Материалы:
 - Лист ГОСТ 19903-2015, 09Г2С ГОСТ 19281-2014;
 - Труба ГОСТ 10704-91, Сталь 09Г2С ГОСТ 5520-2017;
 - Проволока Св-08Г2С ГОСТ 2246-70.
4. Сварка дуговая в защитном газе по ГОСТ 14771-76.
Проволока Св-08Г2С ГОСТ 2246-70.
5. Сварку выполнить по контуру прилегания деталей. Катет шва по наименьшей толщине свариваемых деталей.
6. Допускается изготовление сварного корпуса.
7. Площадь покрытия 3,9 м².

Поз.	Обозначение	Наименование	Кол	Прим.
1	Труба $\phi 159 \times 5,0$ L=1225	Труба	1	23,08 кг
2	$\phi 377 \times 25$	Опора	1	17,2 кг
3	392x340x6	Основание	1	6,28 кг
4	177x105x6	Ребра	2	0,75 кг
5	177x83x6	Ребра	1	0,69 кг
6	120x97x5	Косынка	8	0,3 кг
7	1165x157,5x5	Обечайка	2	7,22 кг
8	1231x340x5	Обечайка наружная	1	16,42 кг
9	111x400x0,8	Оболочка (аццинка)	2	2,79 кг
10	Труба $\phi 38 \times 3,0$ L=1025	Труба-септик	2	2,65 кг

					5А Ст159х5+2ф38х3-377х25-355-ППУ-ОЦ			
					Неподвижная опора	Лит.	Масса	Масштаб
Изм./Лист	№ докум.	Подп.	Дата				92,9	1:4
Разраб.								
Пров.								
Т.контр.						Лист	Листов	1
Н.контр. Чтв.								