
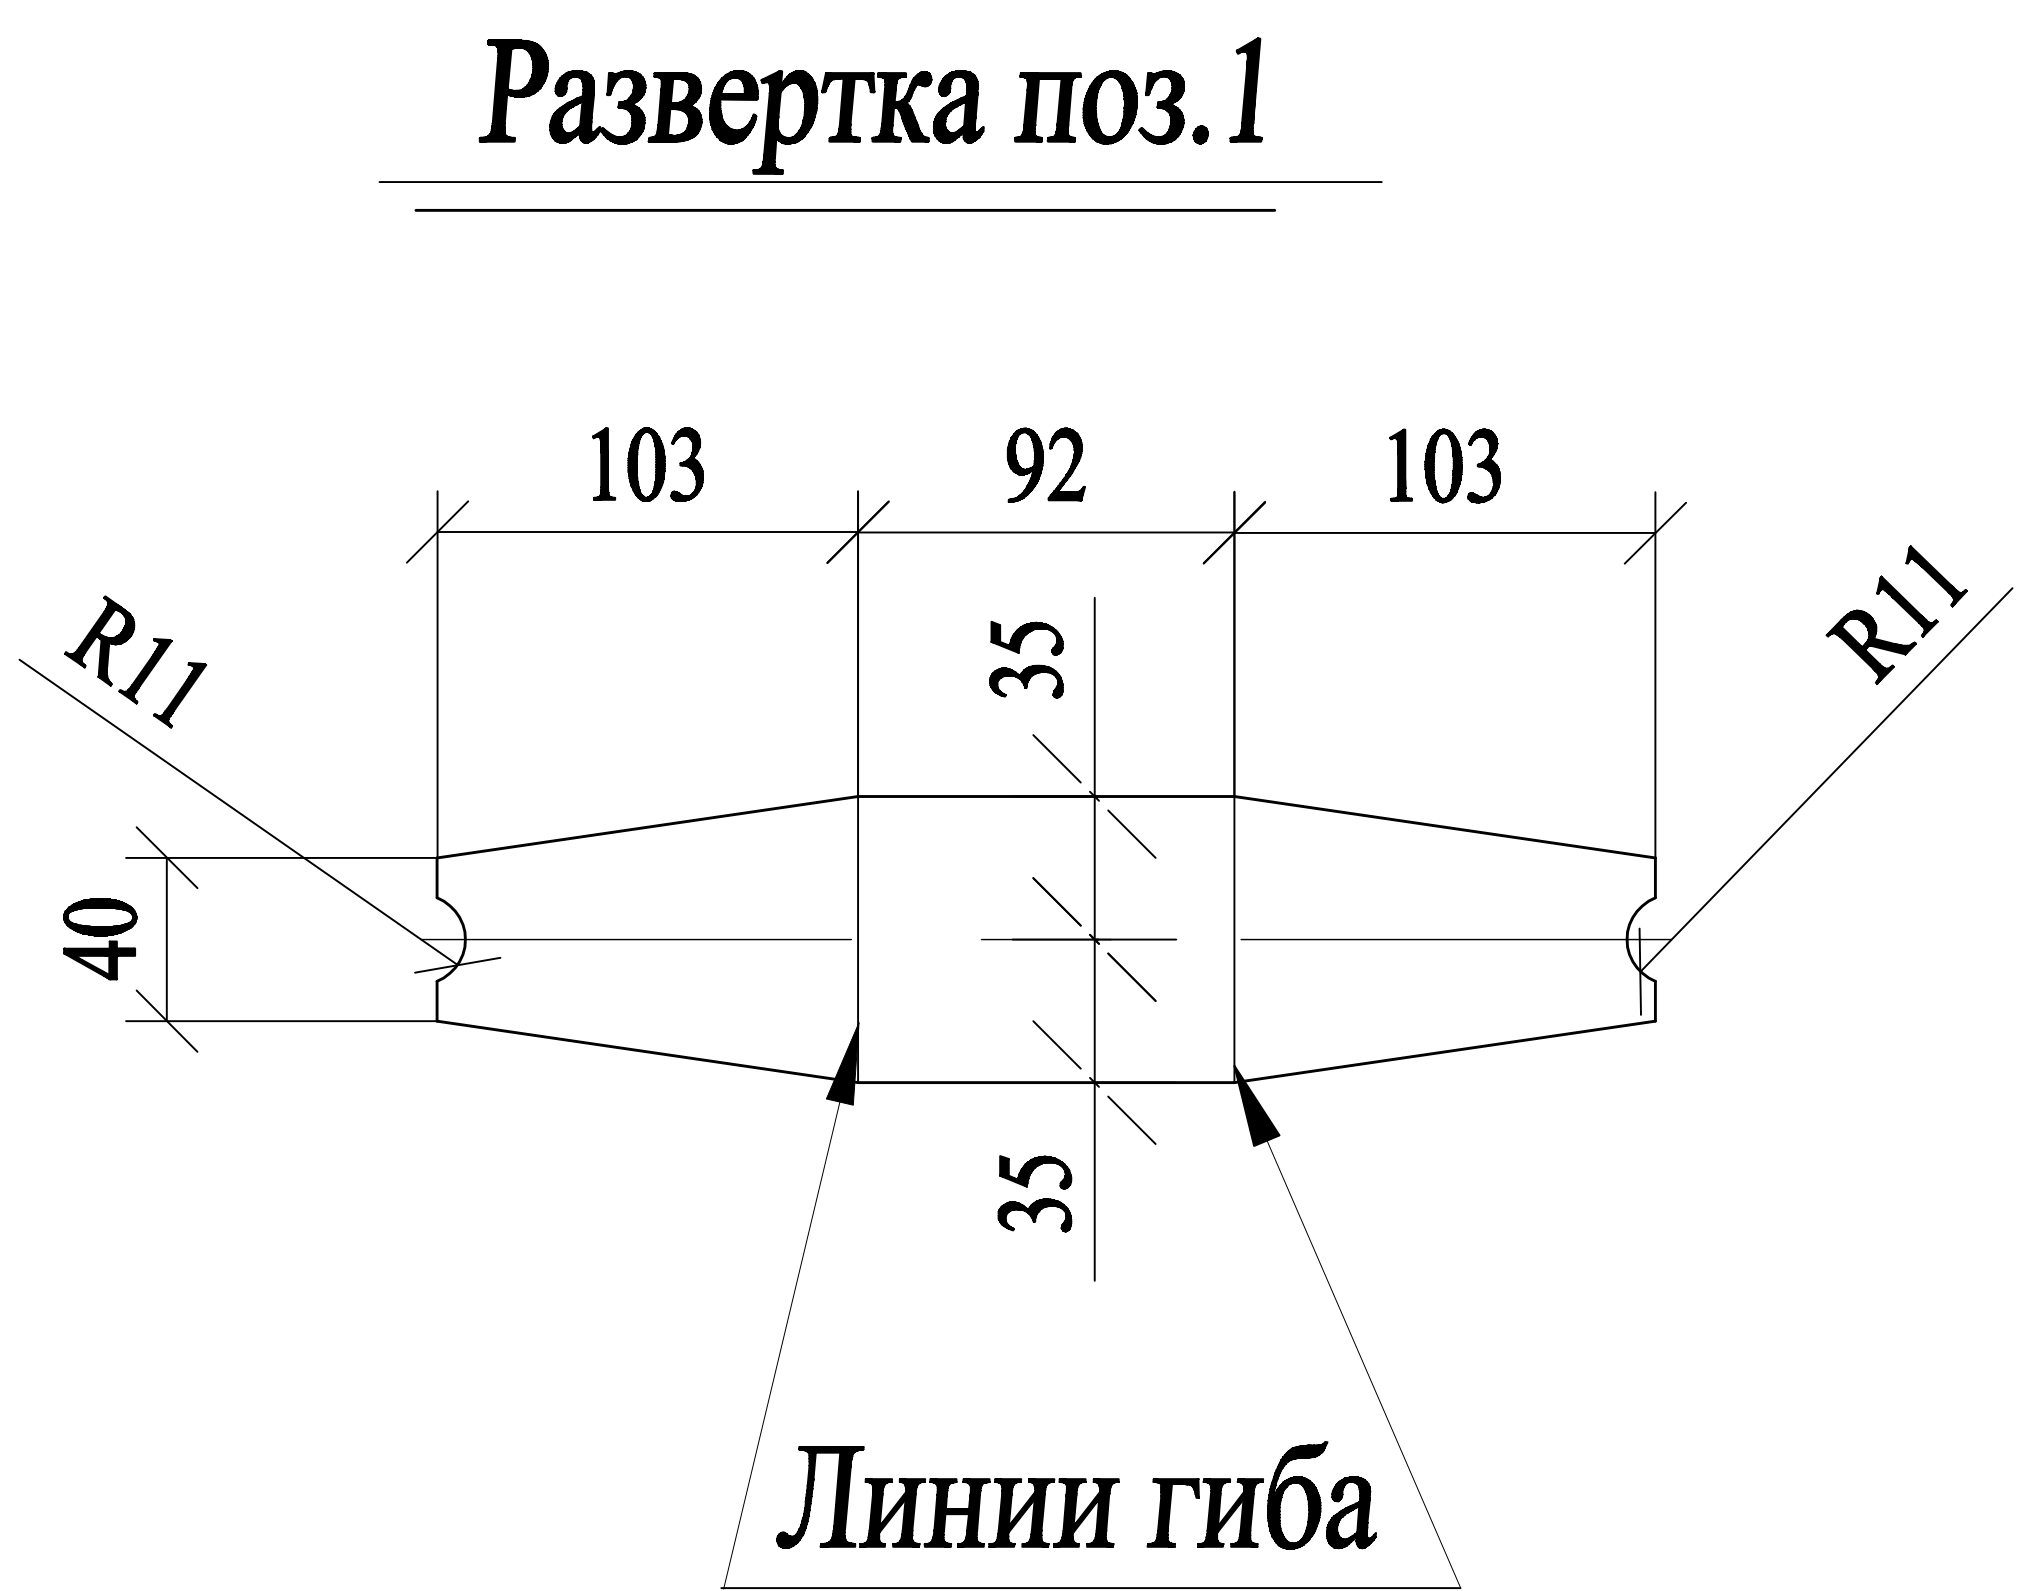
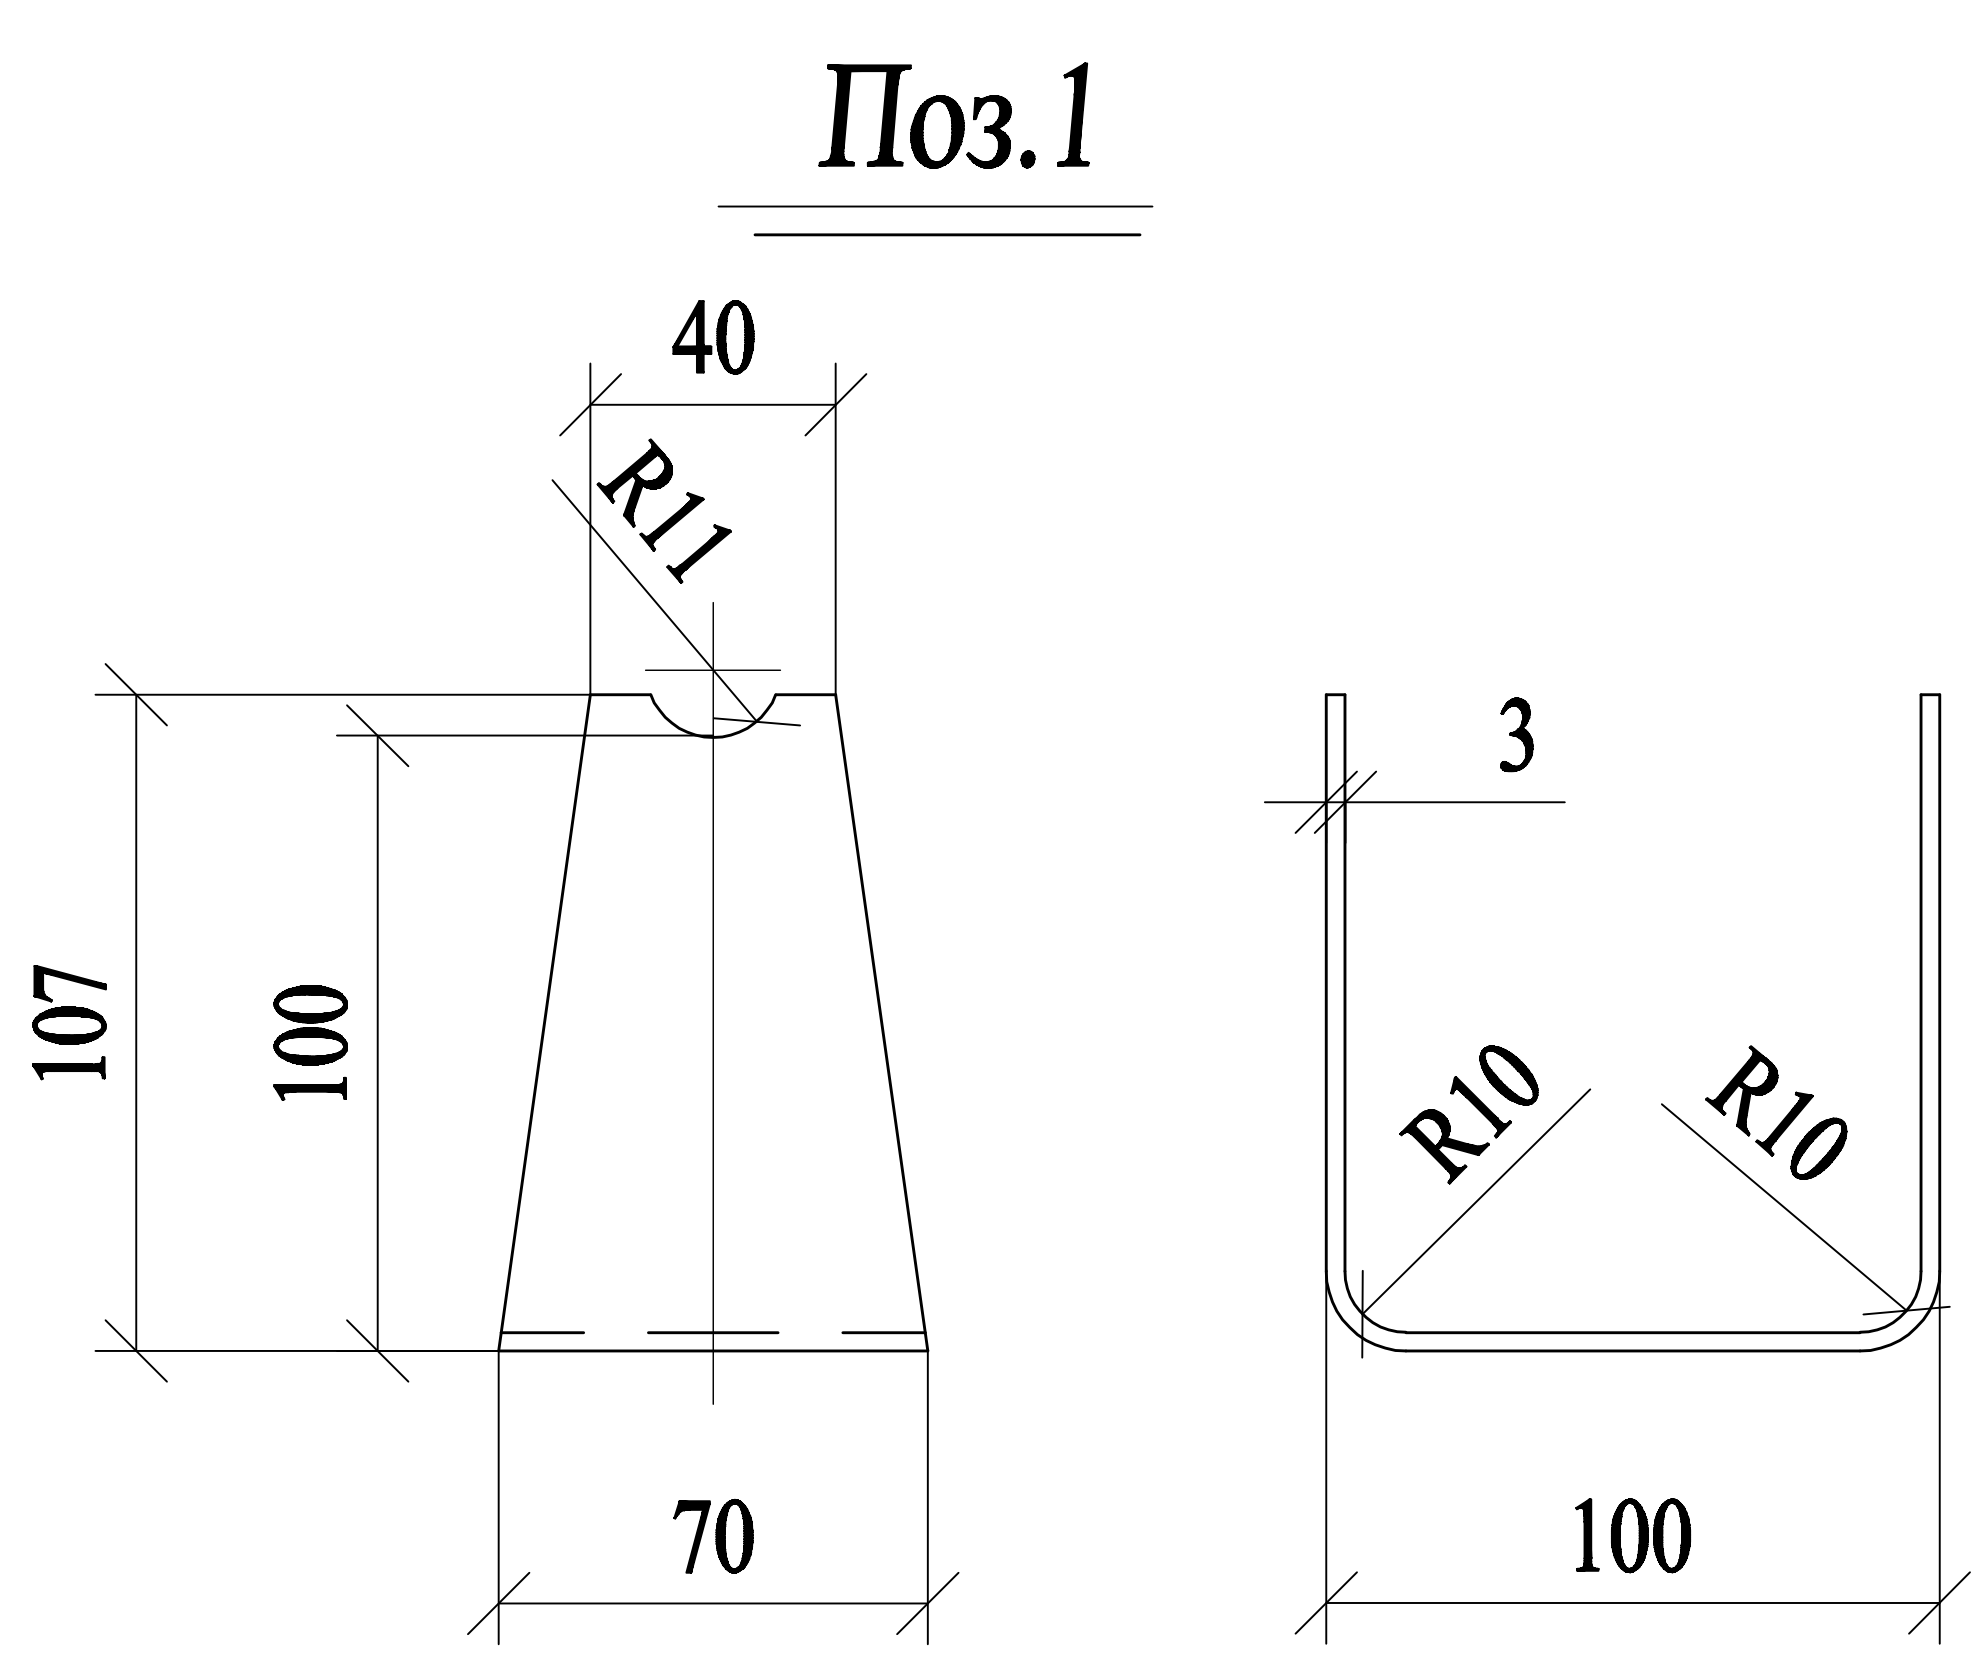
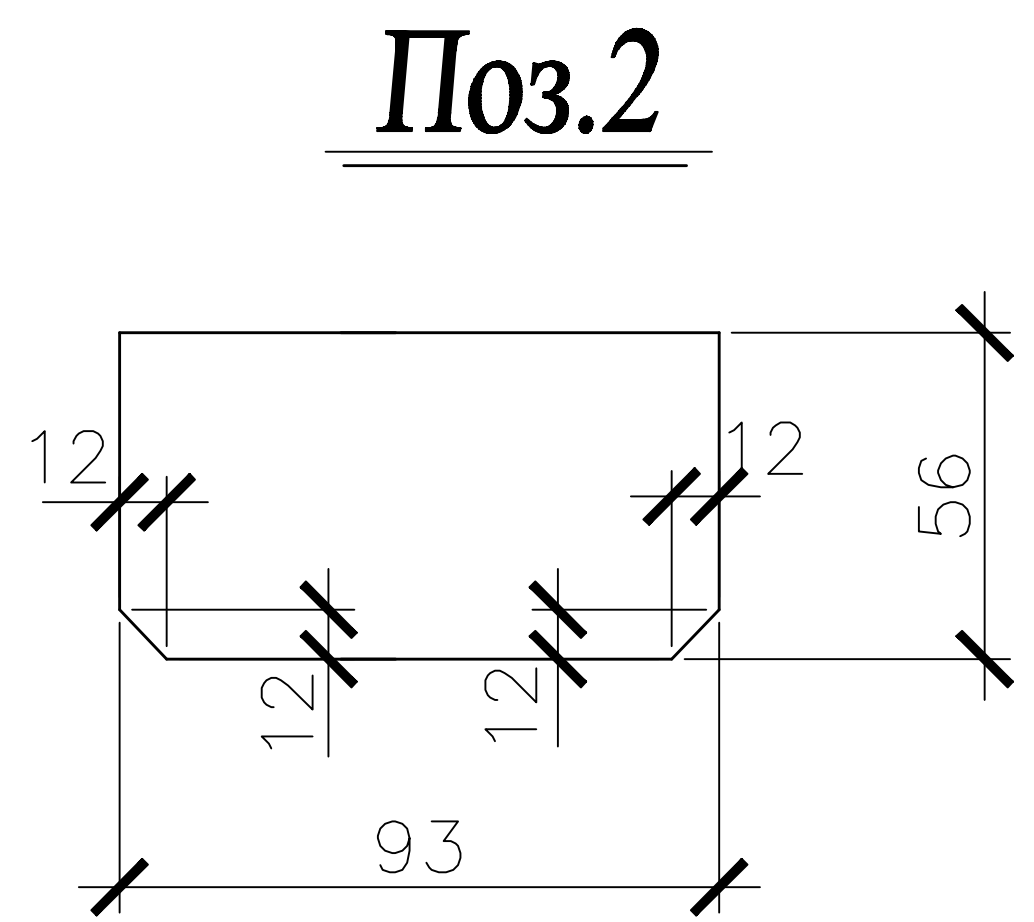


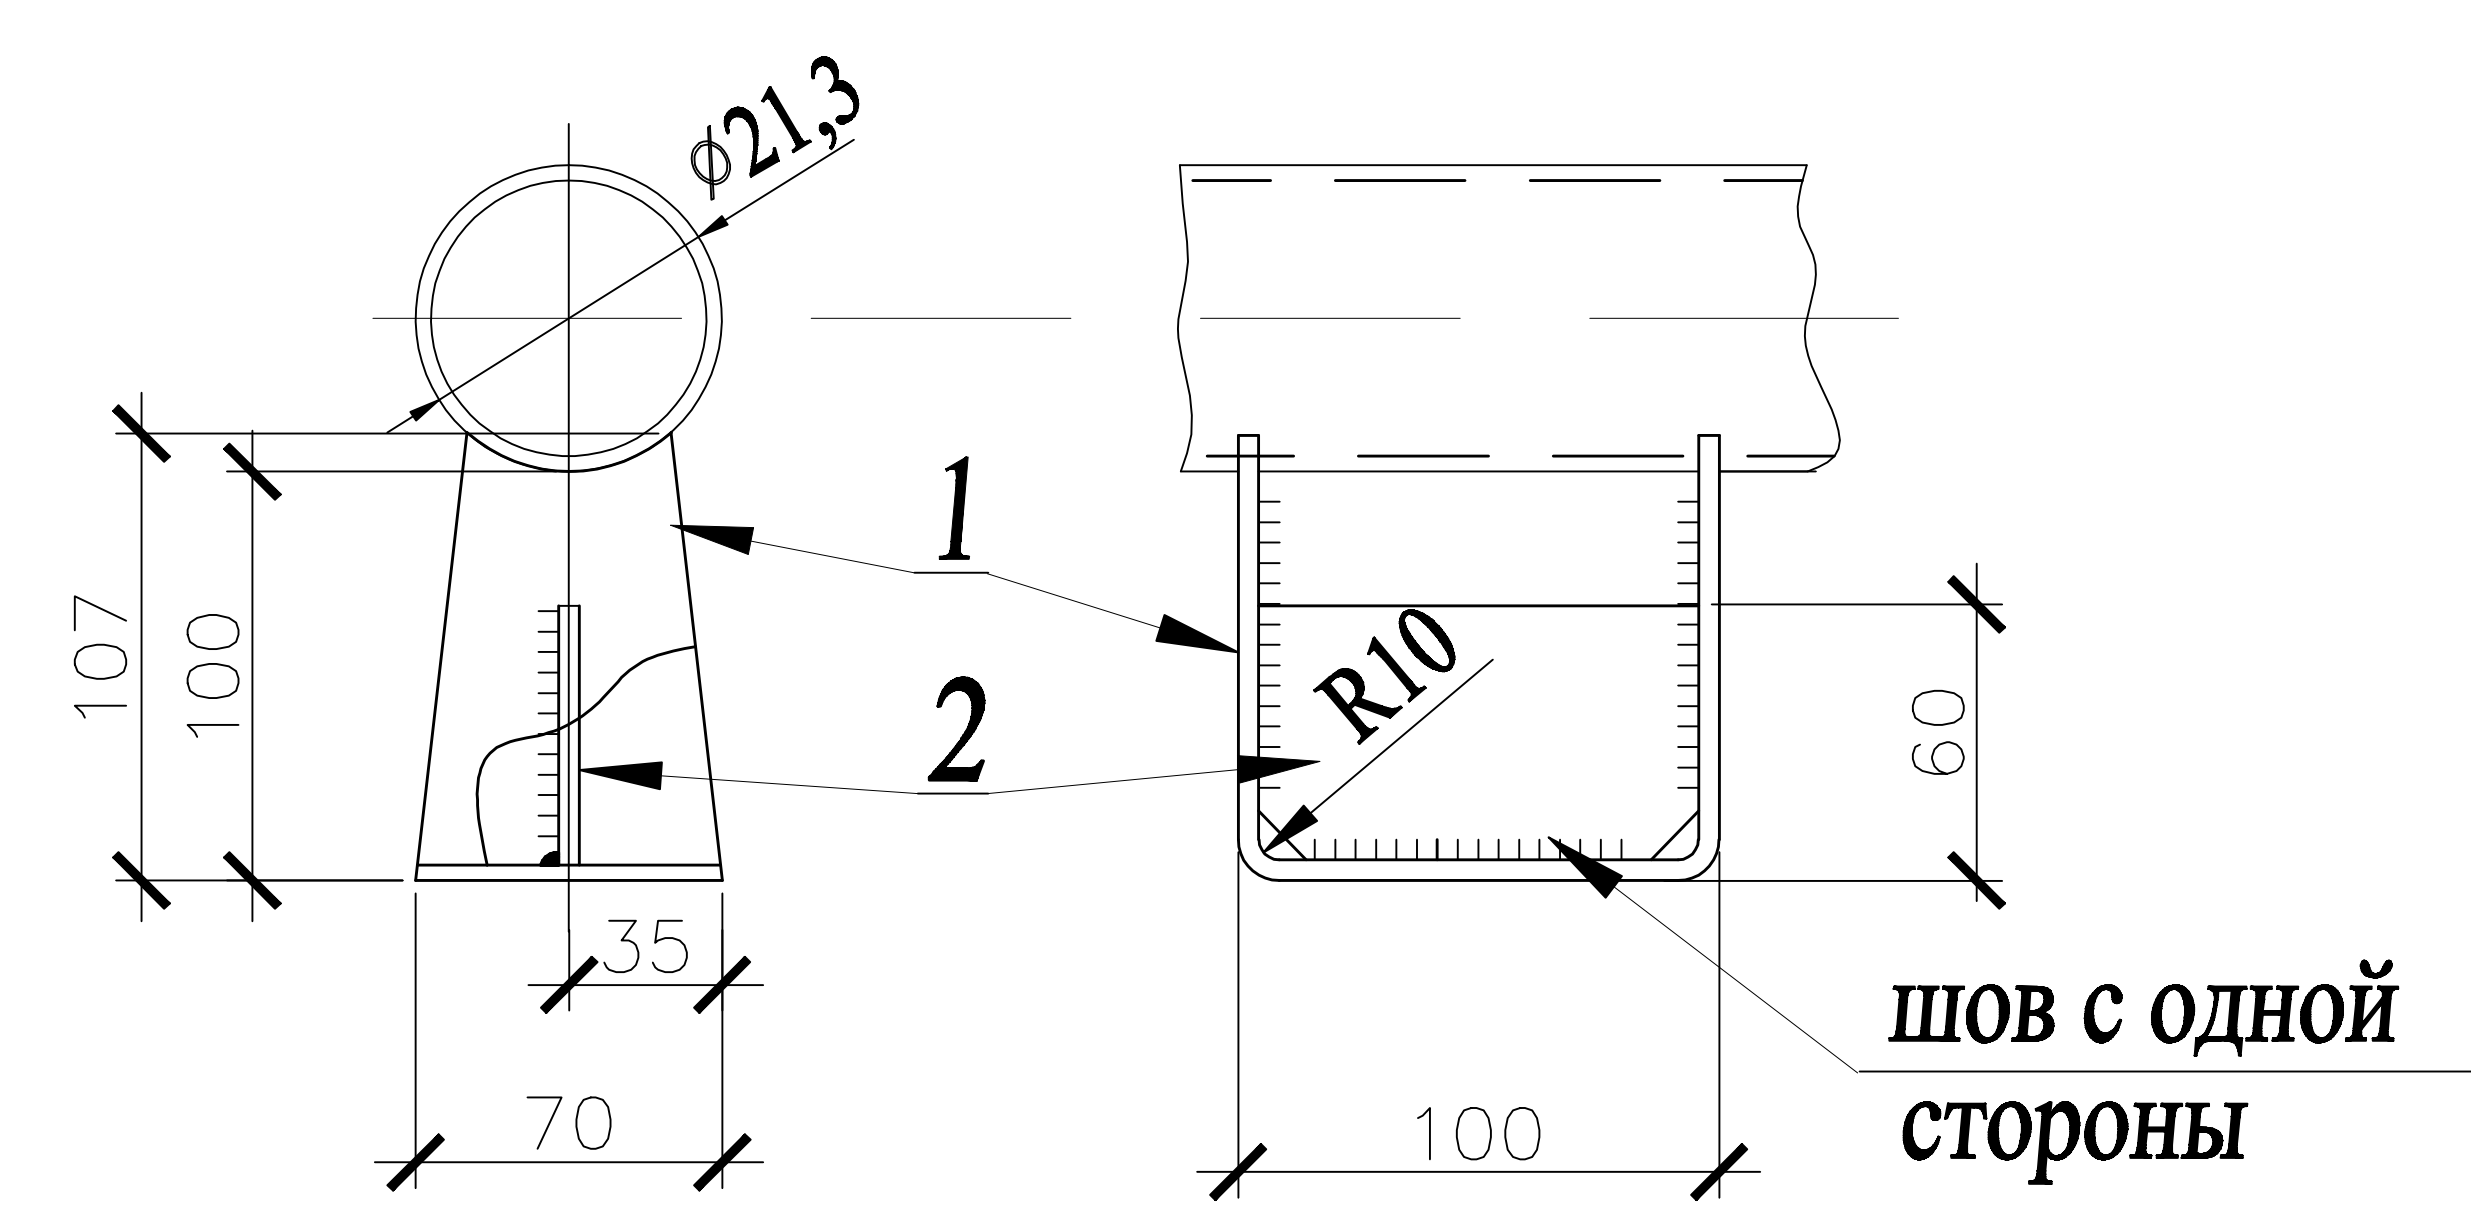

1. Сварные швы - 3 мм
2. Сварка полуавтоматическая по ГОСТ 14771-76 в среде CO₂. Сварочная проволока Св-08Г2С по ГОСТ2246-70 диаметром 1,4-2,0 мм.
3. На заводе окрасить грунтом ГФ-021 по ГОСТ 25129-82 в два слоя.
4. Не указанные предельные отклонения размеров по Н 14. h 4. ±IT 14/2
5. Острые кромки притупить радиусом R = 0,5 мм.
6. Опору маркировать: ОПП1-100.21,3

				на сварные швы			0,01			
	2	1		- 56 x 3	93	0,08	0,08			ср.угл.
	1	1		- 70 x 3	298	0,37	0,37			ф.л.гнуть
ОТПР.		Т.	Н.			ШТ.	ОБЩ.	ЭЛЕМ.	МАРКА	
ЭЛЕМ.	ДЕТ.	КОЛ-ВО		СЕЧЕНИЕ	ДЛИНА		МАССА В КГ		СТАЛИ	ПРИМЕЧАНИЯ

СПЕЦИФИКАЦИЯ СТАЛИ 09Г2С ГОСТ 19281-88

Исполнил										
Проверил										
Рук.груп.										
Гл.конст.										
Гл.техн.										
Гл.инж.	Немиров									

007.ГО.21,3.ОПП1.100.0012.00

Опора подвижная
ОПП1-100.21,3

ГОСТ 14911-82

Стадия	Лист	Листов
Р	1	1
ООО НПП "Строительные технологии"		