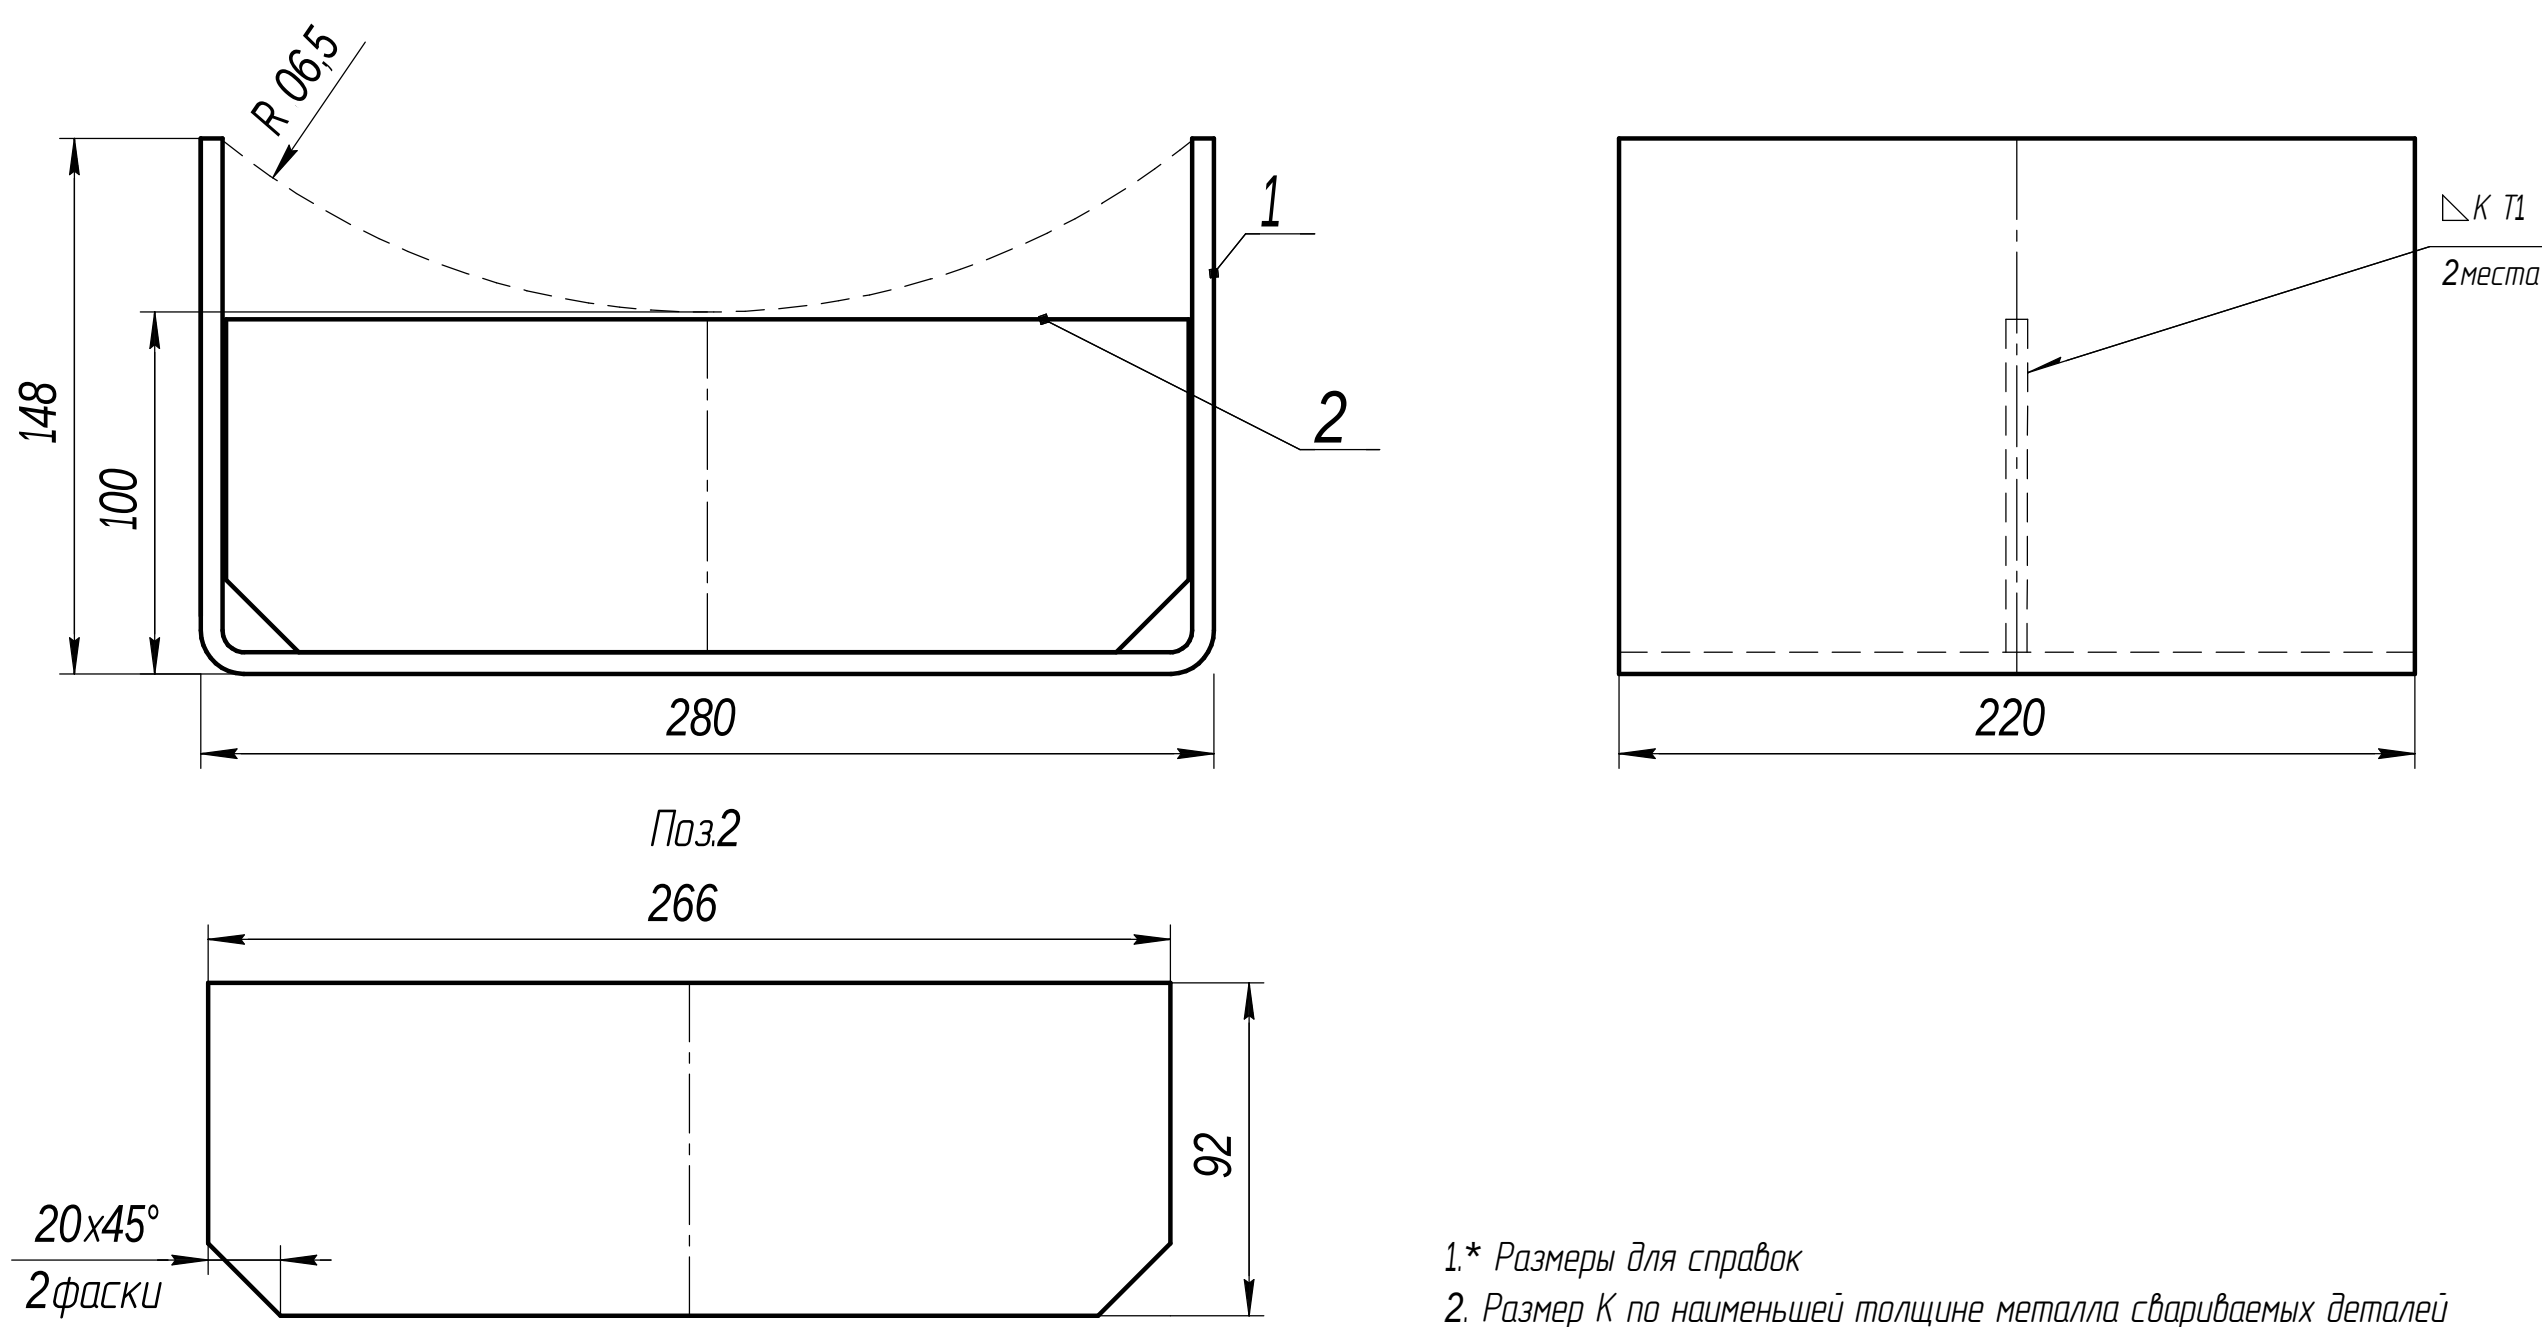


Перв. примен.		Справ. №		Инв. № дубл.		Инв. № инв.		Взам. инв. №		Подп. и дата		Инв. № подл.	
ОПГ2 100.426	
	
1.* Размеры для справок 2. Размер К по наименьшей толщине металла свариваемых деталей 3. H12; h12 + IT/2	
<table><tr><td colspan="2">Формат</td><td colspan="2">Зона</td><td colspan="2">Поз.</td><td colspan="2">Обозначение</td><td colspan="2">Наименование</td><td colspan="2">Кол.</td><td colspan="2">Примечание</td></tr><tr><td colspan="2"></td><td colspan="2"></td><td colspan="2"></td><td colspan="2"></td><td colspan="2">Сборочные единицы</td><td colspan="2"></td><td colspan="2"></td></tr><tr><td colspan="2"></td><td colspan="2"></td><td colspan="2">1</td><td colspan="2">Корпус</td><td colspan="2">556x220x6</td><td colspan="2">1</td><td colspan="2">5.72</td></tr><tr><td colspan="2"></td><td colspan="2"></td><td colspan="2">2</td><td colspan="2">Редра</td><td colspan="2">266x92x6</td><td colspan="2">1</td><td colspan="2">1.13</td></tr></table>														Формат		Зона		Поз.		Обозначение		Наименование		Кол.		Примечание										Сборочные единицы										1		Корпус		556x220x6		1		5.72						2		Редра		266x92x6		1		1.13	
Формат		Зона		Поз.		Обозначение		Наименование		Кол.		Примечание	
								Сборочные единицы	
				1		Корпус		556x220x6		1		5.72	
				2		Редра		266x92x6		1		1.13	
<table><tr><td colspan="2">Изм.</td><td colspan="2">Лист</td><td colspan="2">№ докум.</td><td colspan="2">Подп.</td><td colspan="2">Дата</td><td colspan="4">ОПГ2 100.426</td></tr><tr><td colspan="2">Разраб.</td><td colspan="2"></td><td colspan="2"></td><td colspan="2"></td><td colspan="2"></td><td colspan="2" rowspan="2">Опора подвижная</td><td colspan="2">Лит.</td><td colspan="2">Масса</td><td colspan="2">Масштаб</td></tr><tr><td colspan="2">Пров.</td><td colspan="2"></td><td colspan="2"></td><td colspan="2"></td><td colspan="2"></td><td colspan="2"></td><td colspan="2">6.85</td><td colspan="2">1:2</td></tr><tr><td colspan="2">Т.контр.</td><td colspan="2"></td><td colspan="2"></td><td colspan="2"></td><td colspan="2"></td><td colspan="2"></td><td colspan="2">Лист</td><td colspan="2">Листов</td><td colspan="2">1</td></tr><tr><td colspan="2">Н.контр.</td><td colspan="2"></td><td colspan="2"></td><td colspan="2"></td><td colspan="2"></td><td colspan="2"></td><td colspan="2"></td><td colspan="2"></td><td colspan="2"></td></tr><tr><td colspan="2">Утв.</td><td colspan="2"></td><td colspan="2"></td><td colspan="2"></td><td colspan="2"></td><td colspan="2"></td><td colspan="2"></td><td colspan="2"></td><td colspan="2"></td></tr></table>														Изм.		Лист		№ докум.		Подп.		Дата		ОПГ2 100.426				Разраб.										Опора подвижная		Лит.		Масса		Масштаб		Пров.												6.85		1:2		Т.контр.												Лист		Листов		1		Н.контр.																		Утв.																	
Изм.		Лист		№ докум.		Подп.		Дата		ОПГ2 100.426	
Разраб.										Опора подвижная		Лит.		Масса		Масштаб	
Пров.														6.85		1:2	
Т.контр.												Лист		Листов		1	
Н.контр.	
Утв.	