

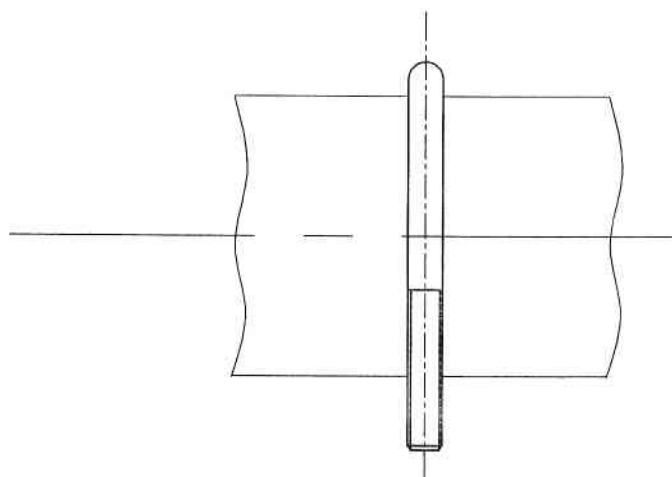


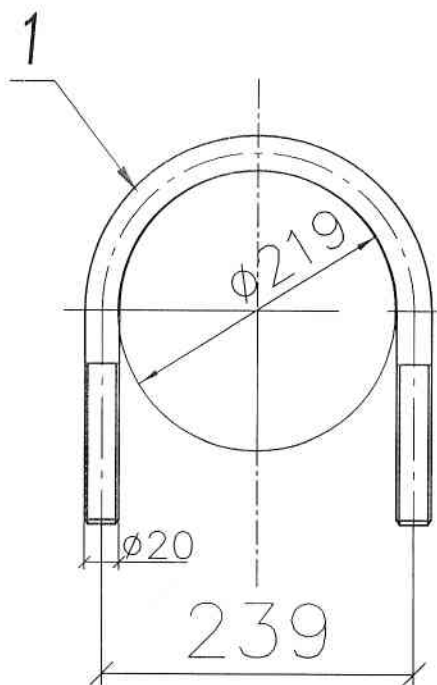

Поз.1

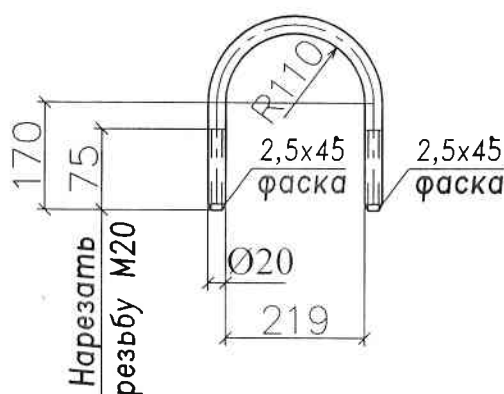

Примечания:

1. Острые кромки притупить.
2. На заводе окрасить грунтом ГФ-021 по ГОСТ 25129-82 в два слоя.
3. Не указанные предельные отклонения размеров по Н14, h14. $\pm IT14/2$.
4. Маркировать контрастной на смываемой краской Х-108

								1,767		
	1	1		Кр.ø20	717	1,767	1,767			гнуть
		Т.	Н.	СЕЧЕНИЕ	ДЛИНА	ШТ.	ОБЩ.	ЭЛЕМ.	МАРКА СТАЛИ	ПРИМЕЧАНИЯ
	ДЕТ.	КОЛ.				МАССА В КГ				

СПЕЦИФИКАЦИЯ СТАЛИ 09Г2С ГОСТ19281-88

007.ГО.219.Х.000.8147.01

Исполнил				Хомут 219	Стадия	Лист	Листов
Проверил					Р	1	1
Рук.груп.	Стасьев			по муны ГОСТ 24137-80	ООО НПП "Строительные технологии"		
Гл.конст.							
Гл.техн.							
Гл.инж.	Немиров						