



Э6-919-01-7Е 170 80-Х-801


Справ. №

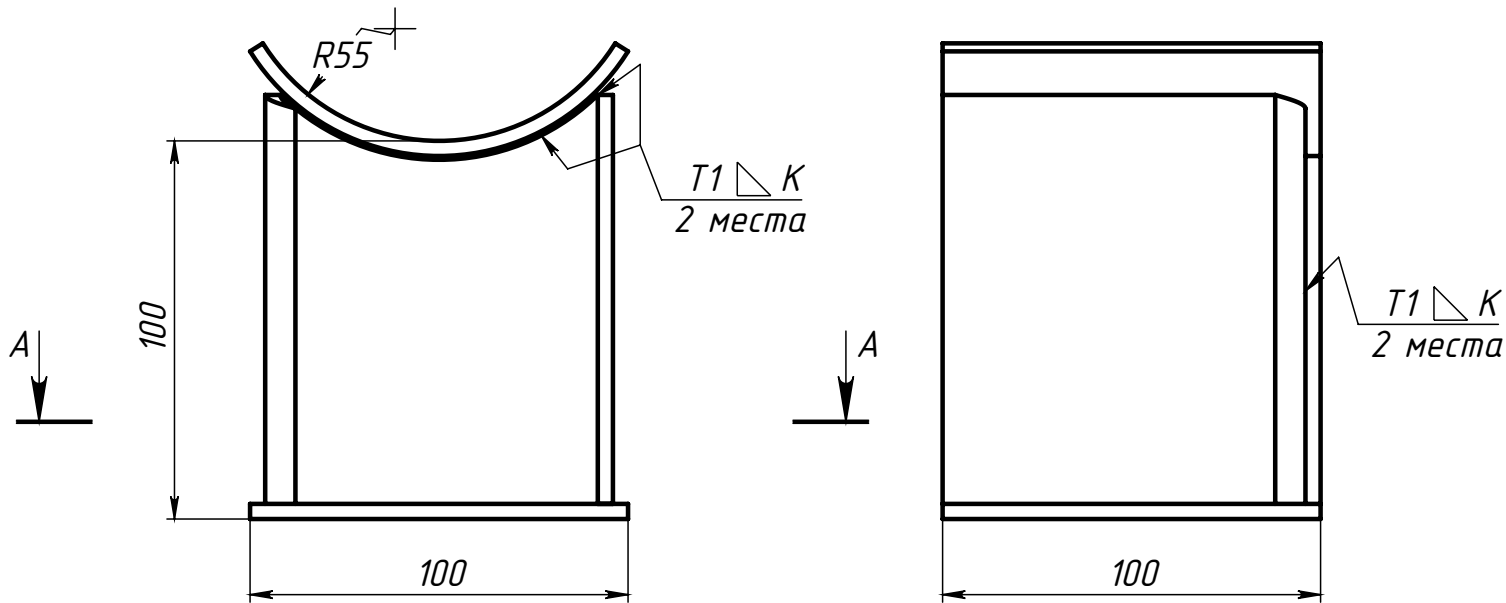


Поз.3 (Ложемент)

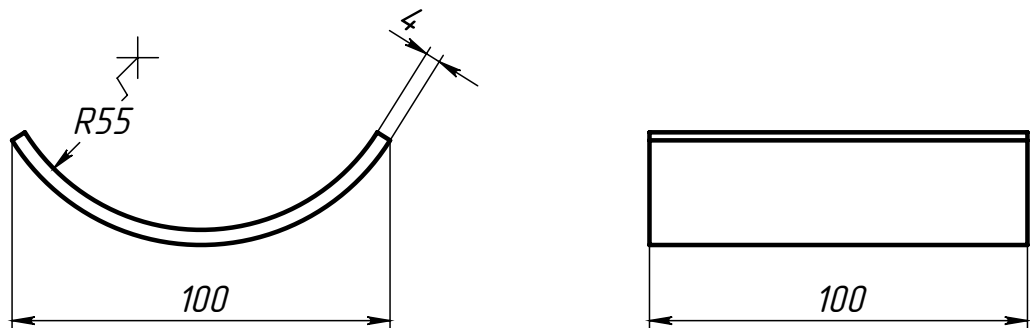


A-A

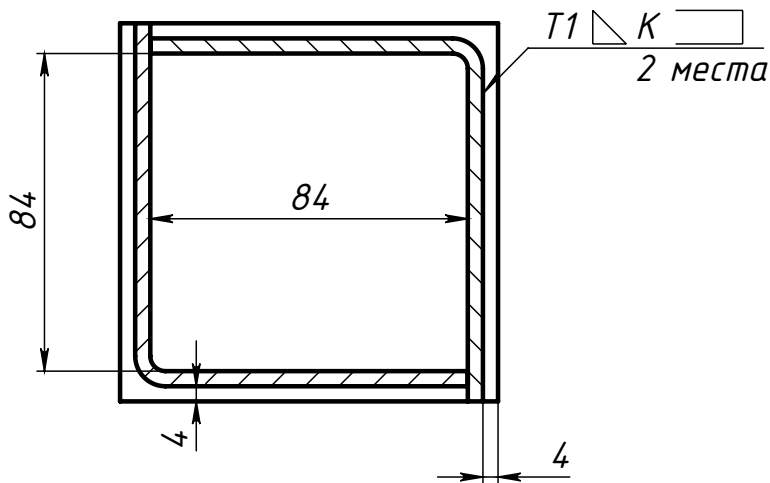

Поз.2 (Угольник)

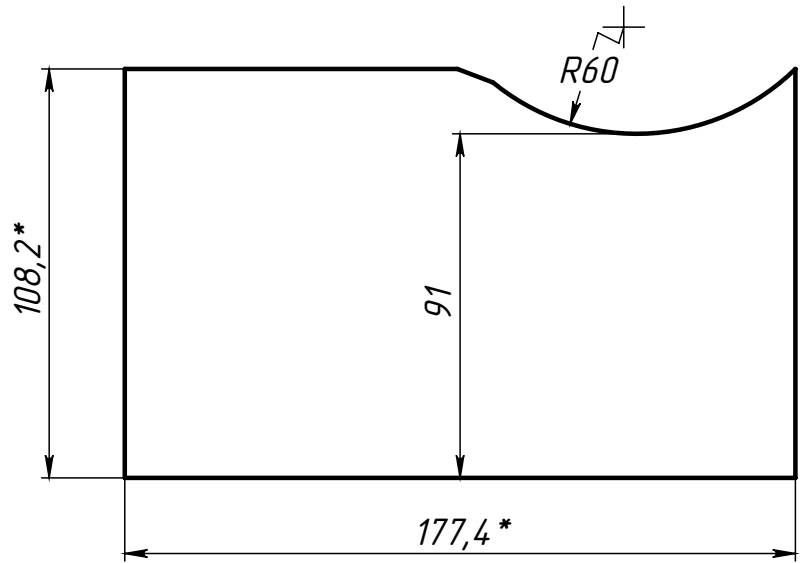

1 : 10

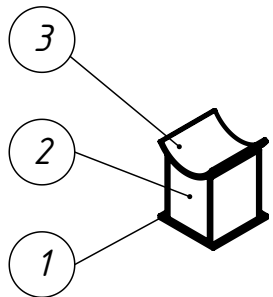

1. *Размеры для справок.
2. Размер К - по наименьшей толщине металла свариваемых деталей.
3. Н12; h12 $\pm$ 1 Т/2.

Поз.	Обозначение	Наименование	Материал	Вес	К-во
1	100x100x4	Основание	09Г2С ГОСТ 4543-71	0.32	1
2	177x108x4	Угольник	09Г2С ГОСТ 4543-71	0.57	2
3	115x100x4	Ложемент	Сталь 08Х18Н12Т ГОСТ 5632-72	0.36	1

Изм.	Лист	№ докум.	Подп.	Дата	108-К-08 ОСТ 34-10-616-93		
Разраб.					Опора приварная скользящая и неподвижная		
Пров.							
Т. контр.							
Н. контр.							
Утв.					09Г2С ГОСТ 4543-71 08Х18Н12Т ГОСТ 5632-72		

Лит.	Масса	Масштаб
1	1.83	1:2
Лист 1	Листов 1	

000 "ЗМП"
