



Э6-919-01-7Е 130 01-Х-801

Справ. №



Подп. и дата
Инв. № дубл.
Взам. инв. №
Подп. и дата
Инв. № подл.

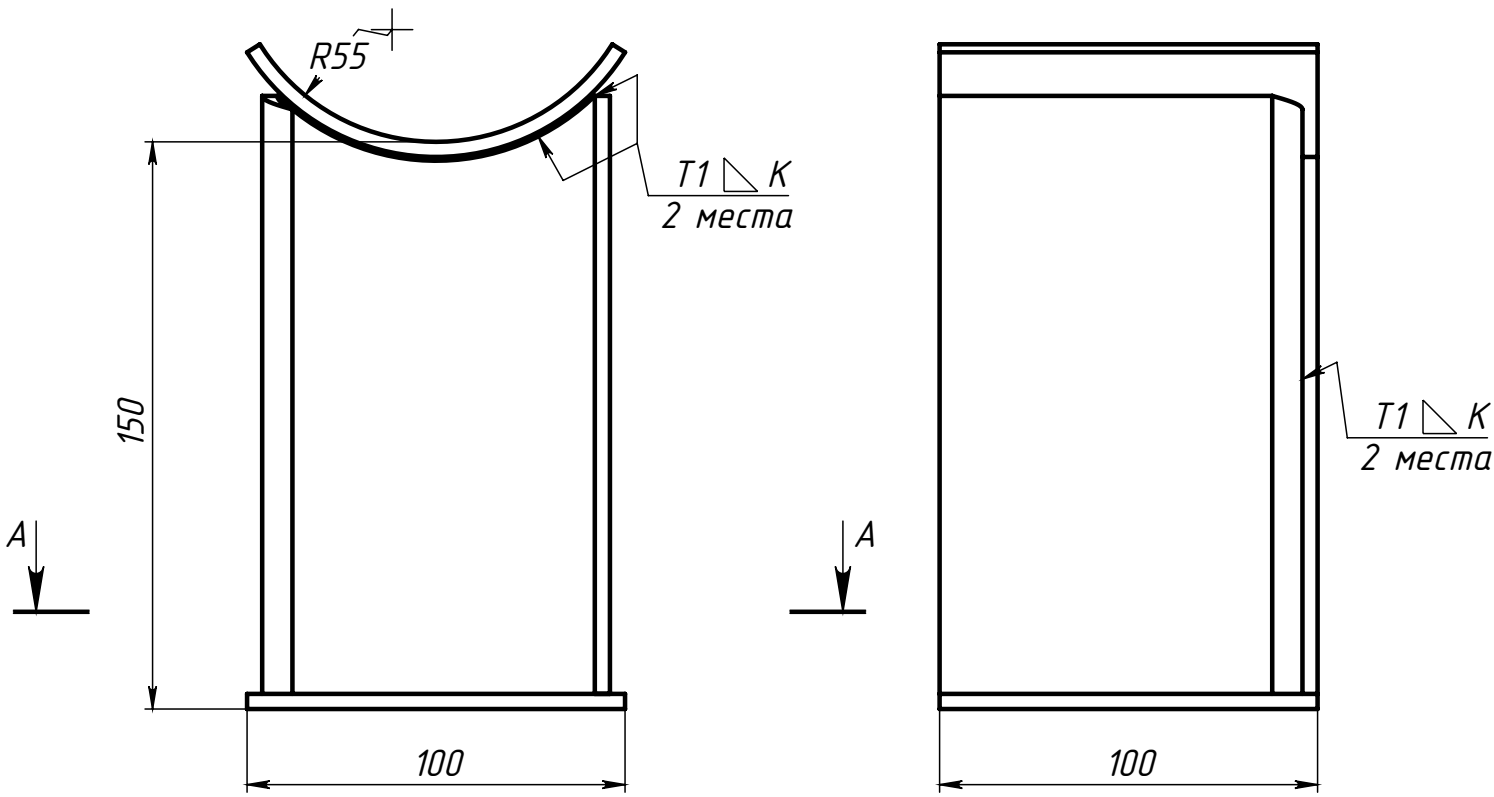


Поз.3 (Ложемент)

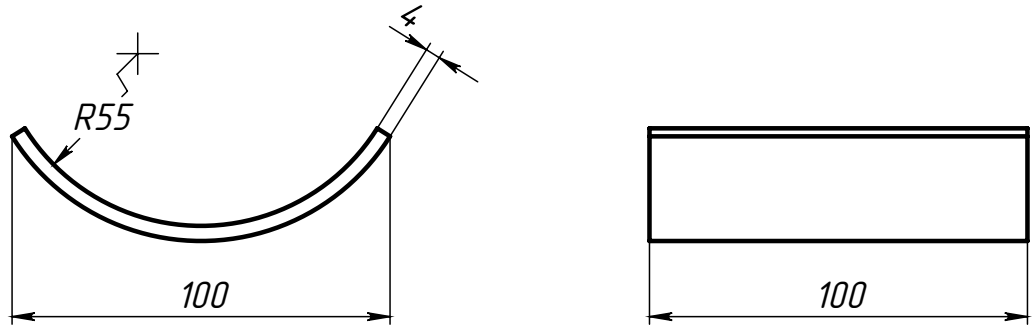

A-A

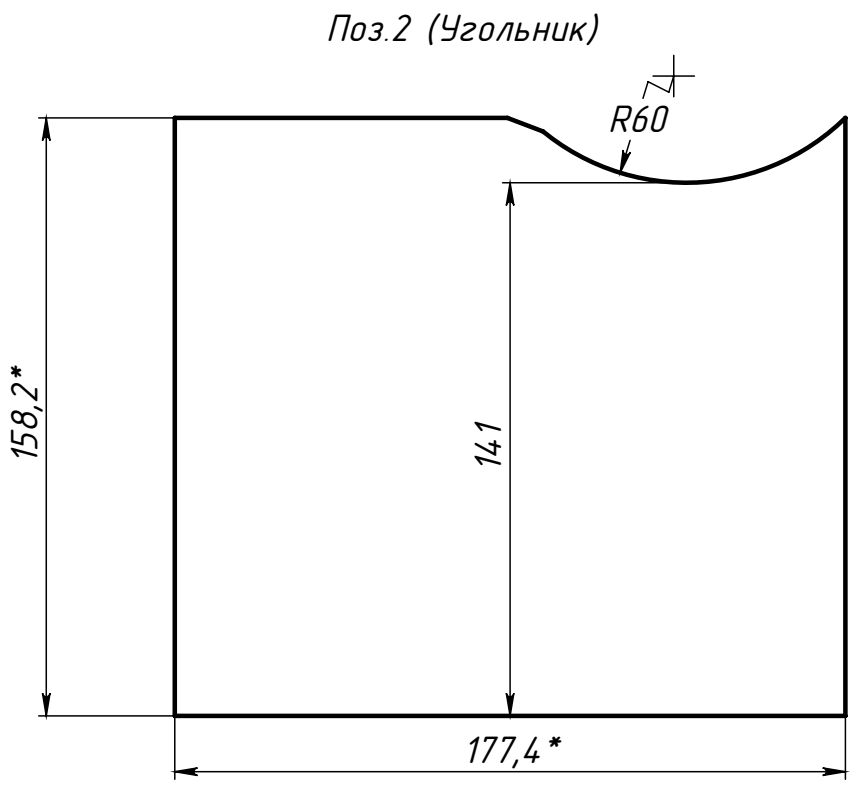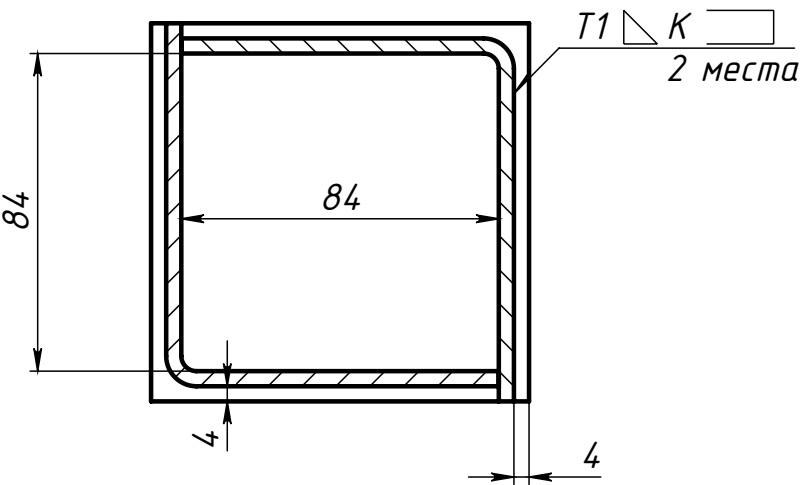

Поз.2 (Угольник)

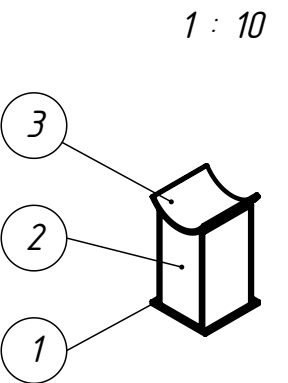

1 : 10

1. *Размеры для справок.
2. Размер К - по наименьшей толщине металла свариваемых деталей.
3. Н12; н12 $\pm$ 1 Т/2.

Поз.	Обозначение	Наименование	Материал	Вес	К-во
1	100x100x4	Основание	09Г2С ГОСТ 4543-71	0.32	1
2	177x158x4	Угольник	09Г2С ГОСТ 4543-71	0.86	2
3	115x100x4	Ложемент	Сталь 08Х18Н12Т ГОСТ 5632-72	0.36	1

					108-К-10 ОСТ 34-10-616-93		
					Опора приварная скользящая и неподвижная		
					000 "ЗМП"		

Изм.	Лист	№ докум.	Подп.	Дата	Лит.	Масса	Масштаб
Разраб.						2.39	1:2
Пров.							
Т. контр.							
Н. контр.							
Утв.							

Лист 1		Листов 1	
--------	--	----------	--

Копировал

Формат А3