



Э6-919-01-7Е 130 72-Х-651

Справ. №



Подп. и дата  
Инв. № дубл.  
Взам. инв. №  
Подп. и дата  
Инв. № подл.

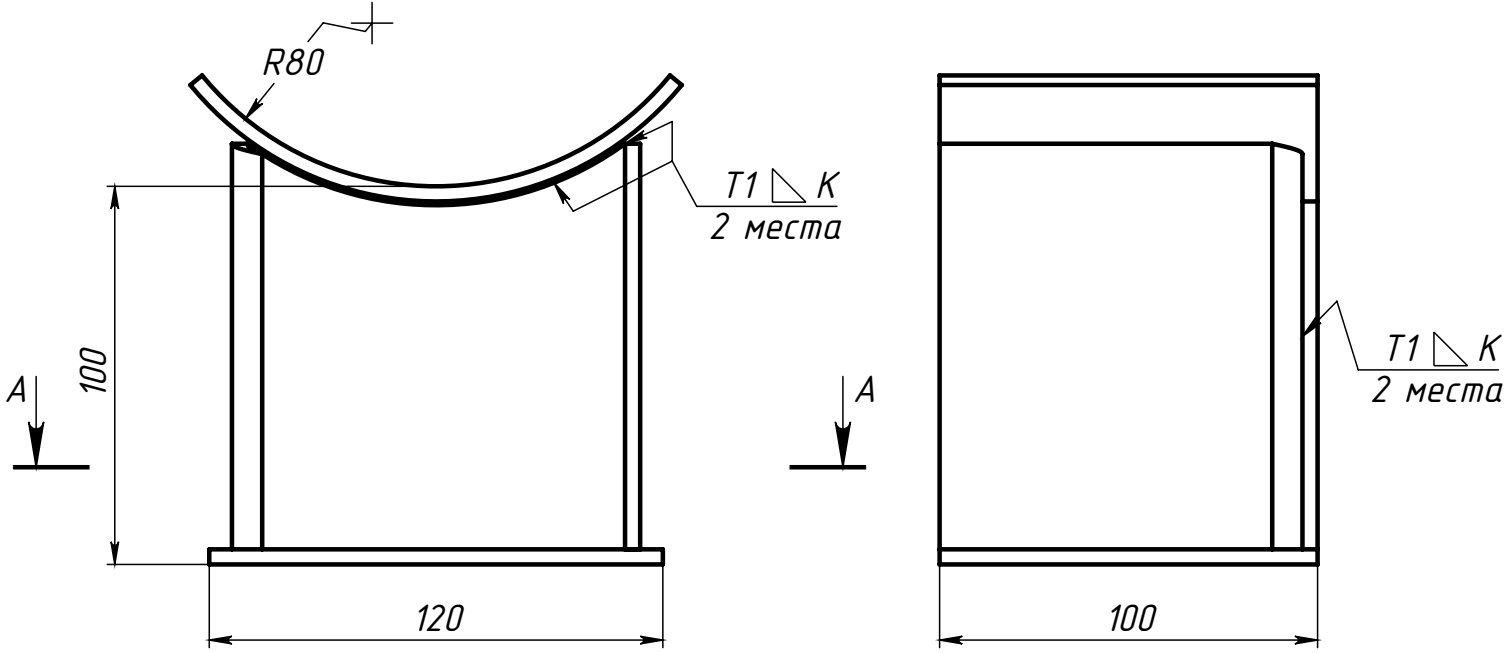


Поз.3 (Ложемент)

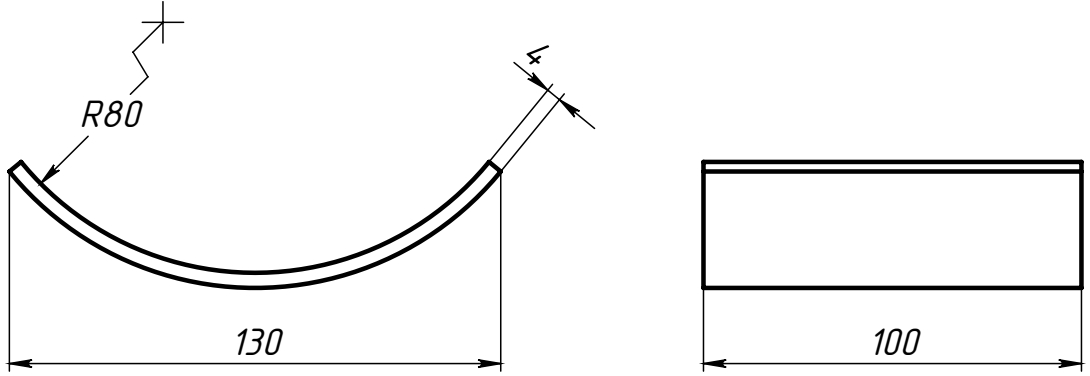

A-A

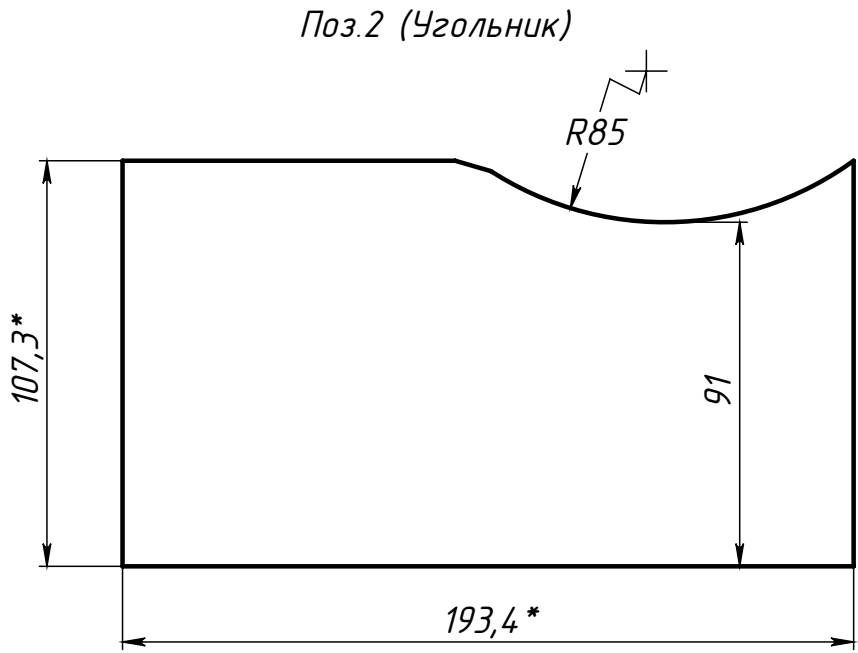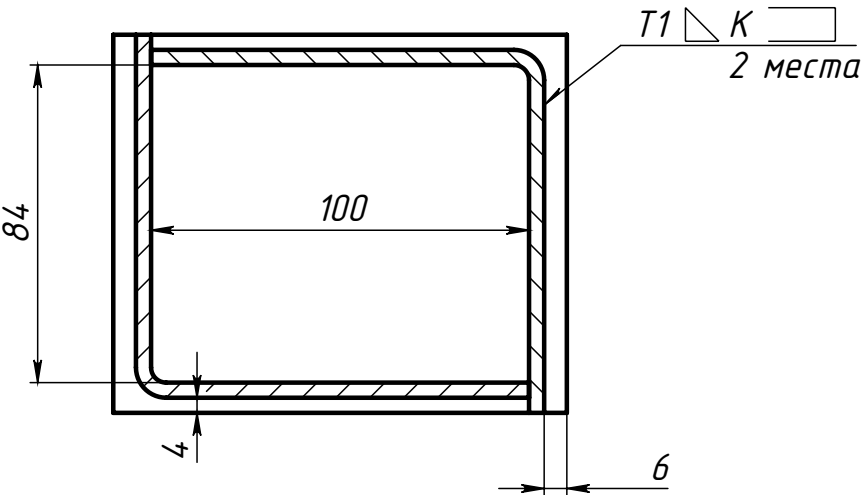

1 : 10

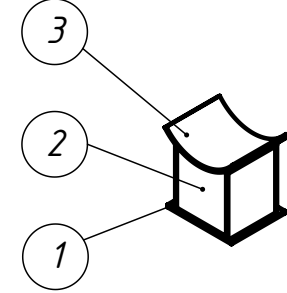

1. \*Размеры для справок.  
2. Размер К - по наименьшей толщине металла свариваемых деталей.  
3. Н12; h12  $\pm$  1 Т/2.

| Поз. | Обозначение | Наименование | Материал                        | Вес  | К-во |
|------|-------------|--------------|---------------------------------|------|------|
| 1    | 120x100x4   | Основание    | 09Г2С ГОСТ 4543-71              | 0.38 | 1    |
| 2    | 193x107x4   | Угольник     | 09Г2С ГОСТ 4543-71              | 0.62 | 2    |
| 3    | 145x100x4   | Ложемент     | Сталь 08Х18Н12Т<br>ГОСТ 5632-72 | 0.46 | 1    |

|           |      |          |       |      |                                             |  |  |
|-----------|------|----------|-------|------|---------------------------------------------|--|--|
| Изм.      | Лист | № докум. | Подп. | Дата | 159-К-24 ОСТ 34-10-616-93                   |  |  |
| Разраб.   |      |          |       |      | Опора приварная<br>скользящая и неподвижная |  |  |
| Пров.     |      |          |       |      |                                             |  |  |
| Т. контр. |      |          |       |      | Лист 1                                      |  |  |
| Н. контр. |      |          |       |      | Листов 1                                    |  |  |
| Утв.      |      |          |       |      | 000 "ЗМП"                                   |  |  |

|      |       |         |
|------|-------|---------|
| Лит. | Масса | Масштаб |
|      | 2.08  | 1:2     |

Файл: 159-К-24 ОСТ 34-10-616-93 Конфигурация: 00