

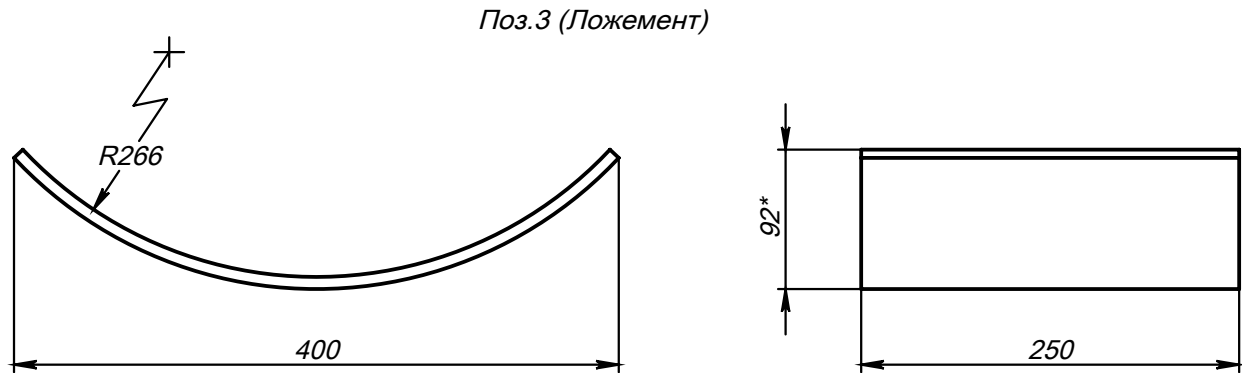
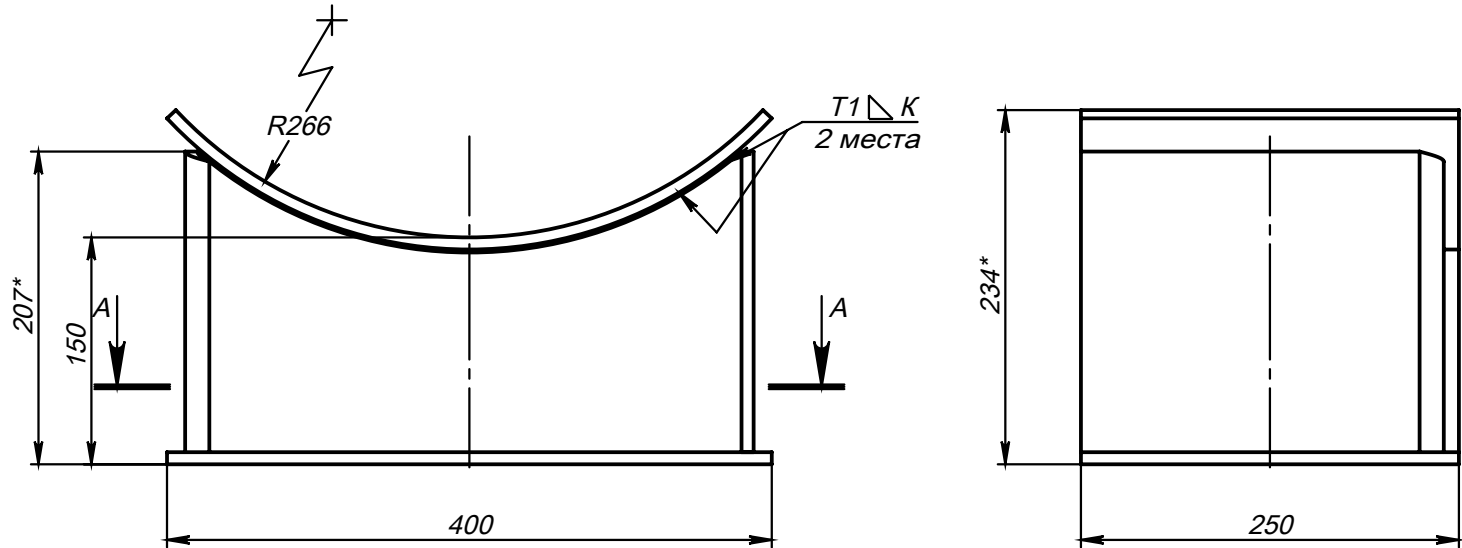



530-К-82 ОСТ 34-10-616-93

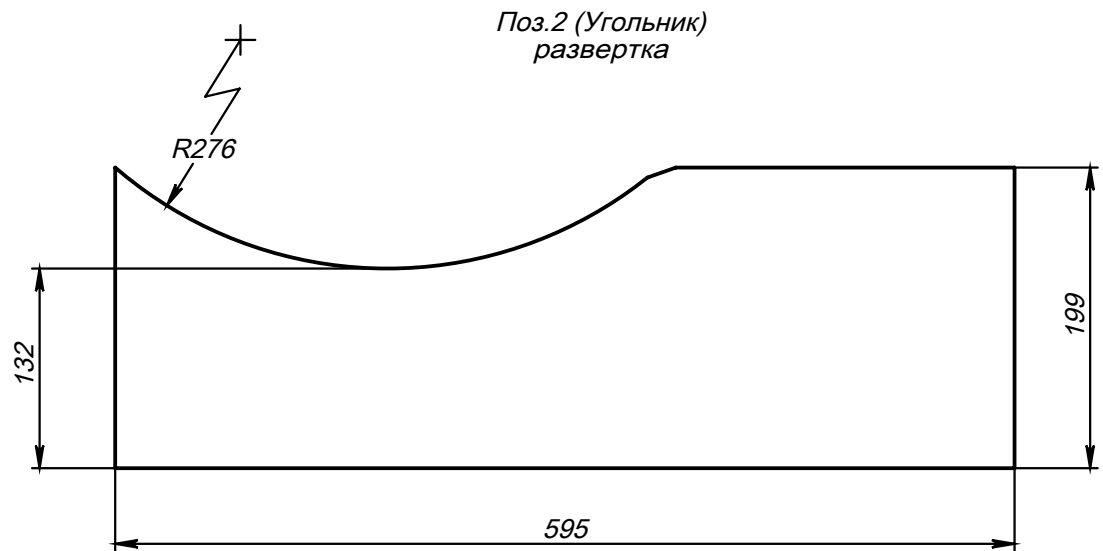

A-A

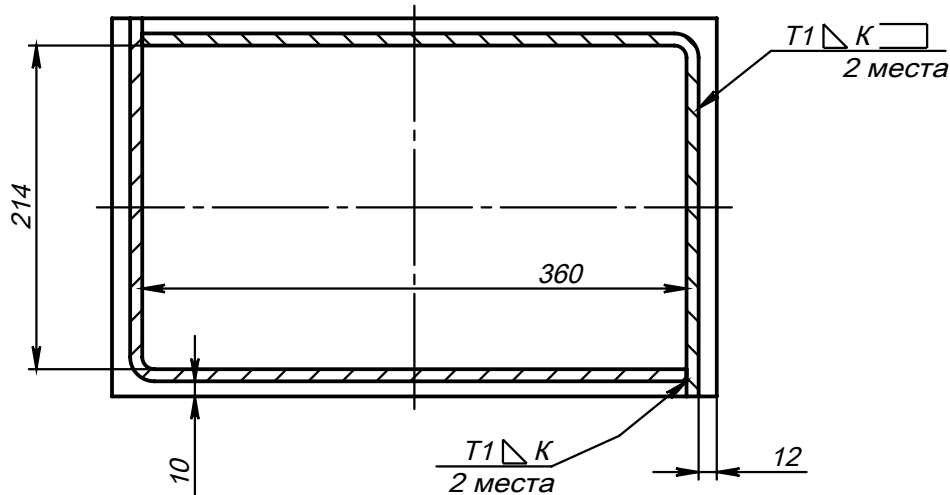

1 : 10

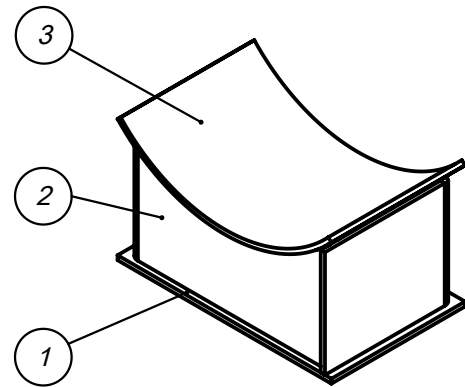

1. *Размеры для справок.
2. Размер К - по наименьшей толщине металла свариваемых деталей.
3. Н12; н12; ±IT/2.

Поз.	Обозначение	Наименование	Вес	К-во
1	400x250x8	Основание	6.32	1
2	595x199x8	Угольник	6.43	2
3	442x250x8	Ложечник (12Х18Н10Т ГОСТ 5632)	6.98	1
530-К-82 ОСТ 34-10-616-93				
Опора приварная			Лит.	Масса
			26.16	1:5
			Лист 1	Листов 1
			ООО "ЗМП"	
09Г2С ГОСТ 4543-71				
Изм.	Лист	№ докум.	Подп.	Дата
Разраб.				
Пров.				
Т. контр.				
Н. контр.				
Утв.				