

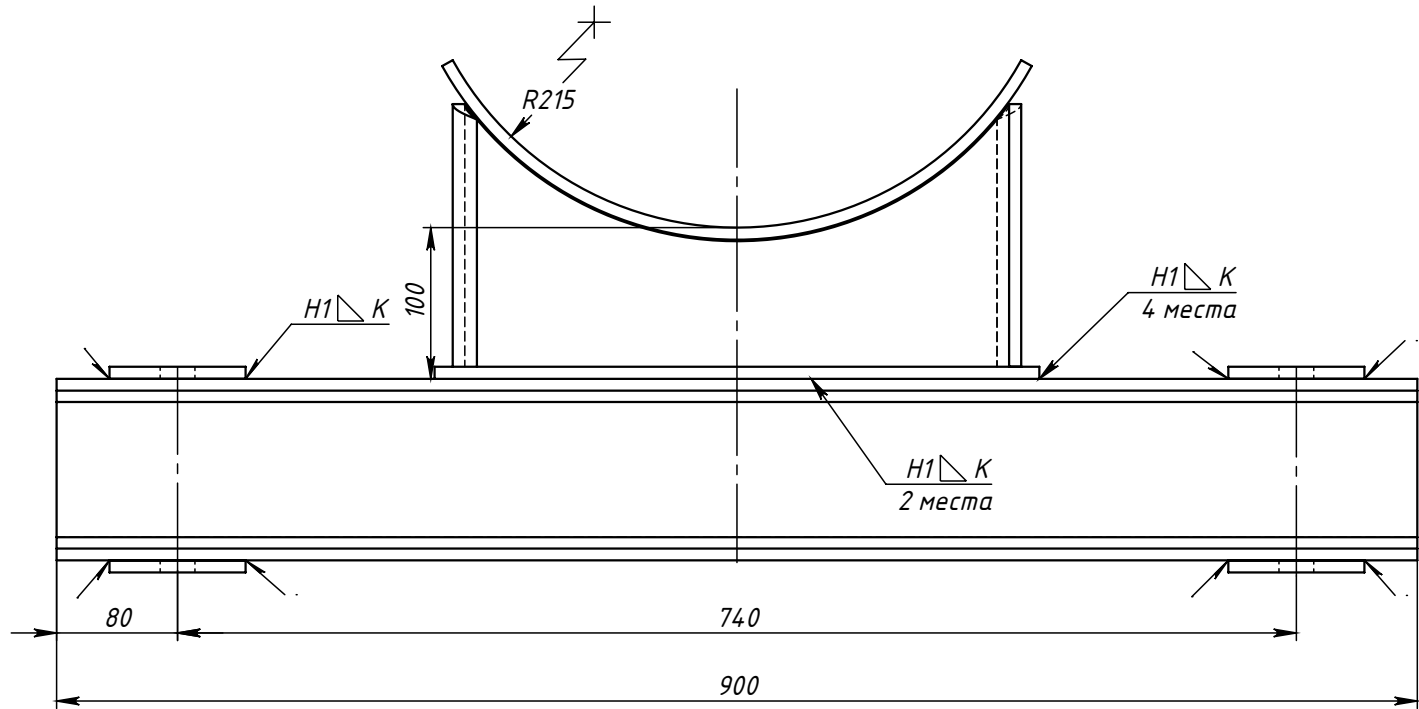


|          |  |              |  |              |  |              |  |              |  |              |  |
|----------|--|--------------|--|--------------|--|--------------|--|--------------|--|--------------|--|
| Справ. № |  | Подп. и дата |  | Инф. № дубл. |  | Взам. инф. № |  | Подп. и дата |  | Инв. № подл. |  |
|          |  |              |  |              |  |              |  |              |  |              |  |


Э6-92L-01-7Э L30 Э9-Г-927

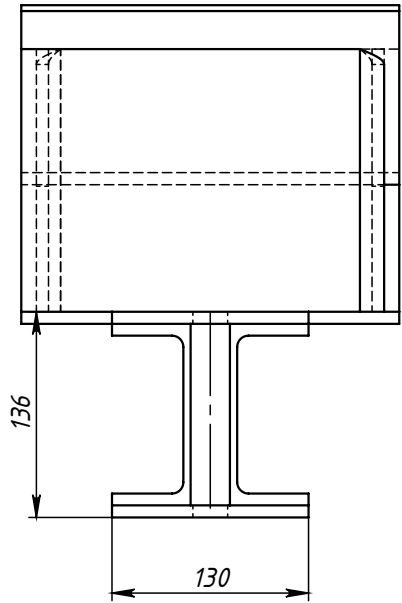

Поз.2 (Планка)

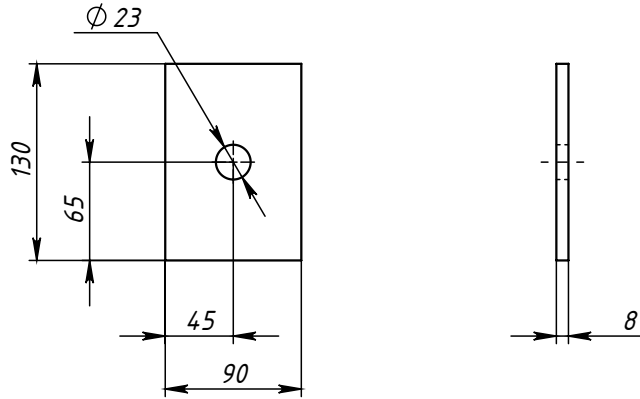

1:10

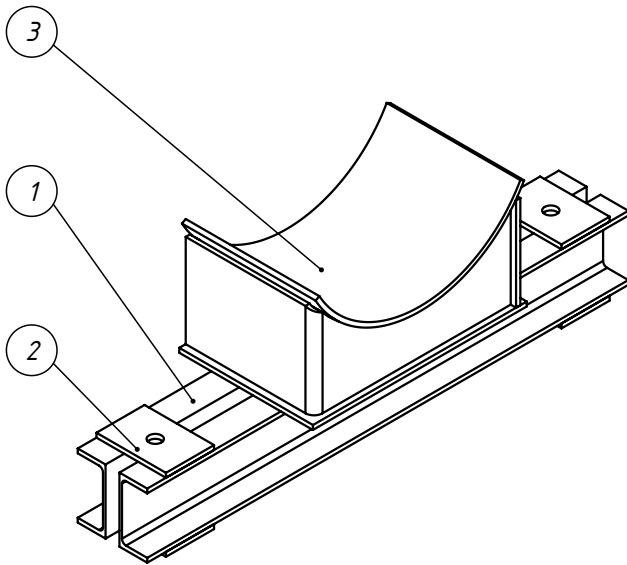

1. \*Размеры для справок.  
2. Размер К – по наименьшей толщине металла свариваемых деталей.  
3. H12; h12; ¼IT/2.

| Поз.                      | Обозначение               | Наименование         | Вес                | К-во      |
|---------------------------|---------------------------|----------------------|--------------------|-----------|
| 1                         | L=900                     | Швеллер 12 ГОСТ 8240 | 9.50               | 2         |
| 2                         | 130x90x8                  | Планка               | 0.71               | 4         |
| 3                         | 426-У-63 ОСТ 34-10-616-93 | Опора приварная      | 23.85              | 1         |
| 426-У-63 ОСТ 34-10-726-93 |                           |                      |                    |           |
| Балка опорная             |                           |                      | Лит.               | Масса     |
|                           |                           |                      | Масштаб            |           |
|                           |                           |                      | Лист 1             | Листов 1  |
|                           |                           |                      | 09Г2С ГОСТ 4543-71 | 000 "ЗМП" |
| Изм.                      | Лист                      | № докум.             | Подп.              | Дата      |
| Разраб.                   |                           |                      |                    |           |
| Пров.                     |                           |                      |                    |           |
| Т. контр.                 |                           |                      |                    |           |
| Н. контр.                 |                           |                      |                    |           |
| Утв.                      |                           |                      |                    |           |