



|        |              |           |       |         |      |      |          |              |              |              |        |          |
|--------|--------------|-----------|-------|---------|------|------|----------|--------------|--------------|--------------|--------|----------|
| Инв. № | Подп. и дата | Т. контр. | Пров. | Разраб. | Изм. | Лист | № докум. | Инв. № дубл. | Подп. и дата | Взам. инв. № | Инв. № | Спраб. № |
|        |              |           |       |         |      |      |          |              |              |              |        |          |

377-ВП-Б2 ОСТ 36-146-88

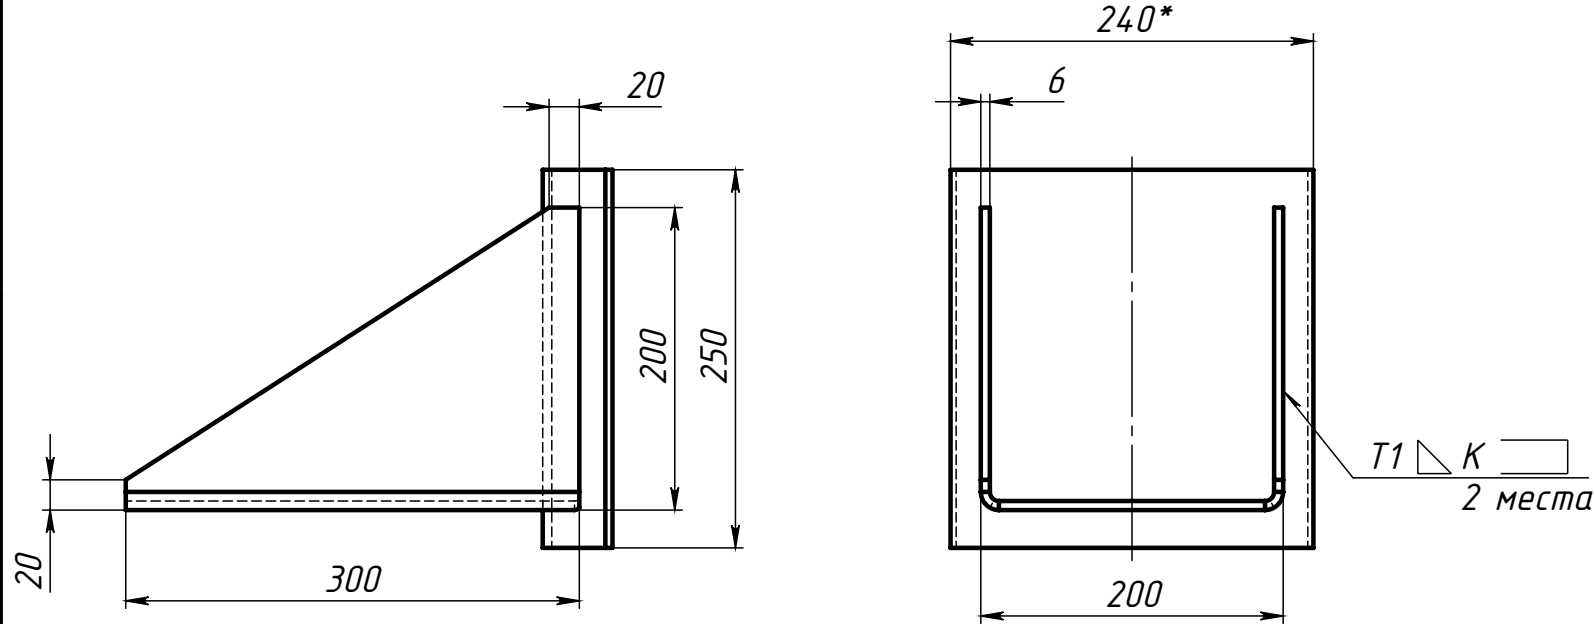


Поз.2 (Ложмент)

1 : 10

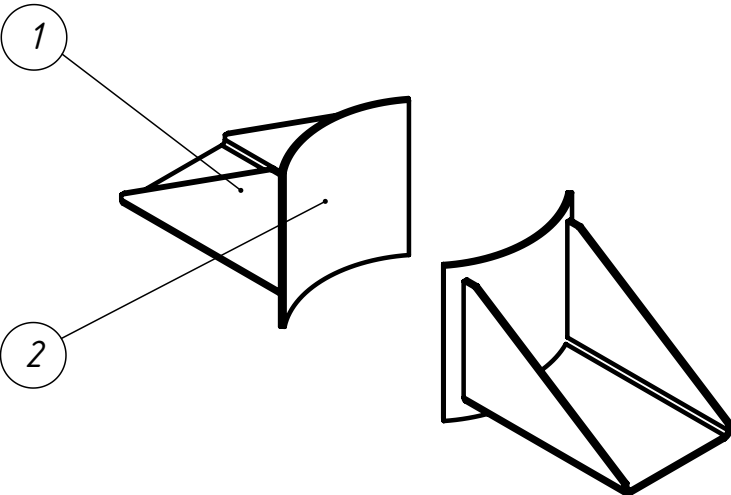

Поз.1 (Корпус) развертка

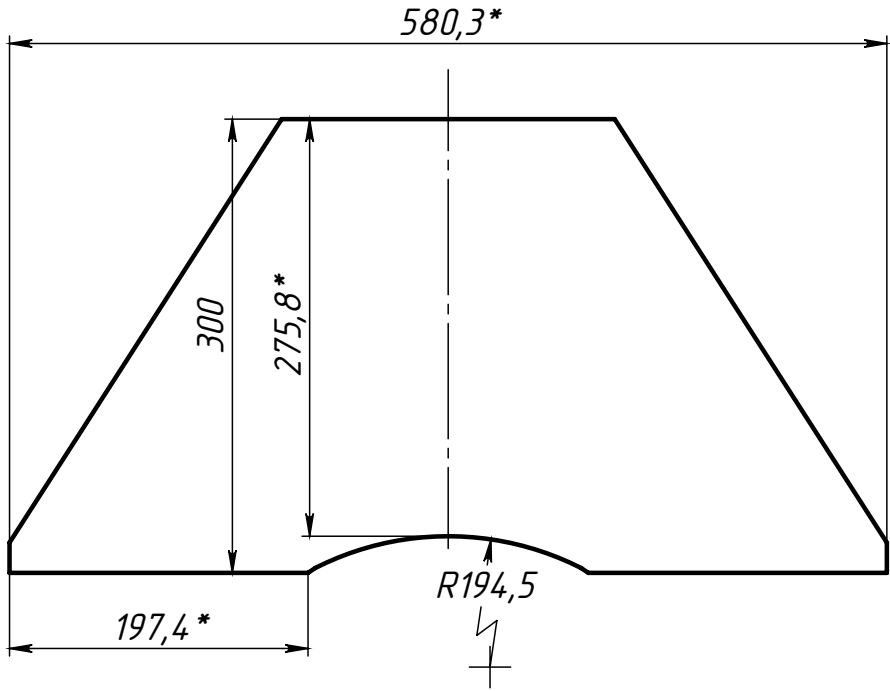

- \*Размеры для справок.
- Размер К - по наименьшей толщине металла свариваемых деталей.
- H12; h12  $\pm$  T/2.

| Поз.                             | Обозначение | Наименование | Вес       | К-во     |
|----------------------------------|-------------|--------------|-----------|----------|
| 1                                | 581х300х6   | Корпус       | 5.72      | 2        |
| 2                                | 255х250х6   | Ложмент      | 3.02      | 2        |
| 377-ВП-Б2 ОСТ 36-146-88          |             |              |           |          |
| Опоры вертикальных трубопроводов |             |              | Лит.      | Масса    |
|                                  |             |              | 17.47     | 1:5      |
|                                  |             |              | Лист 1    | Листов 1 |
|                                  |             |              | 000 "ЗМП" |          |
| 09Г2С ГОСТ 4543-71               |             |              |           |          |
| Изм.                             | Лист        | № докум.     | Подп.     | Дата     |
| Разраб.                          |             |              |           |          |
| Пров.                            |             |              |           |          |
| Т. контр.                        |             |              |           |          |
| Н. контр.                        |             |              |           |          |
| Утв.                             |             |              |           |          |