
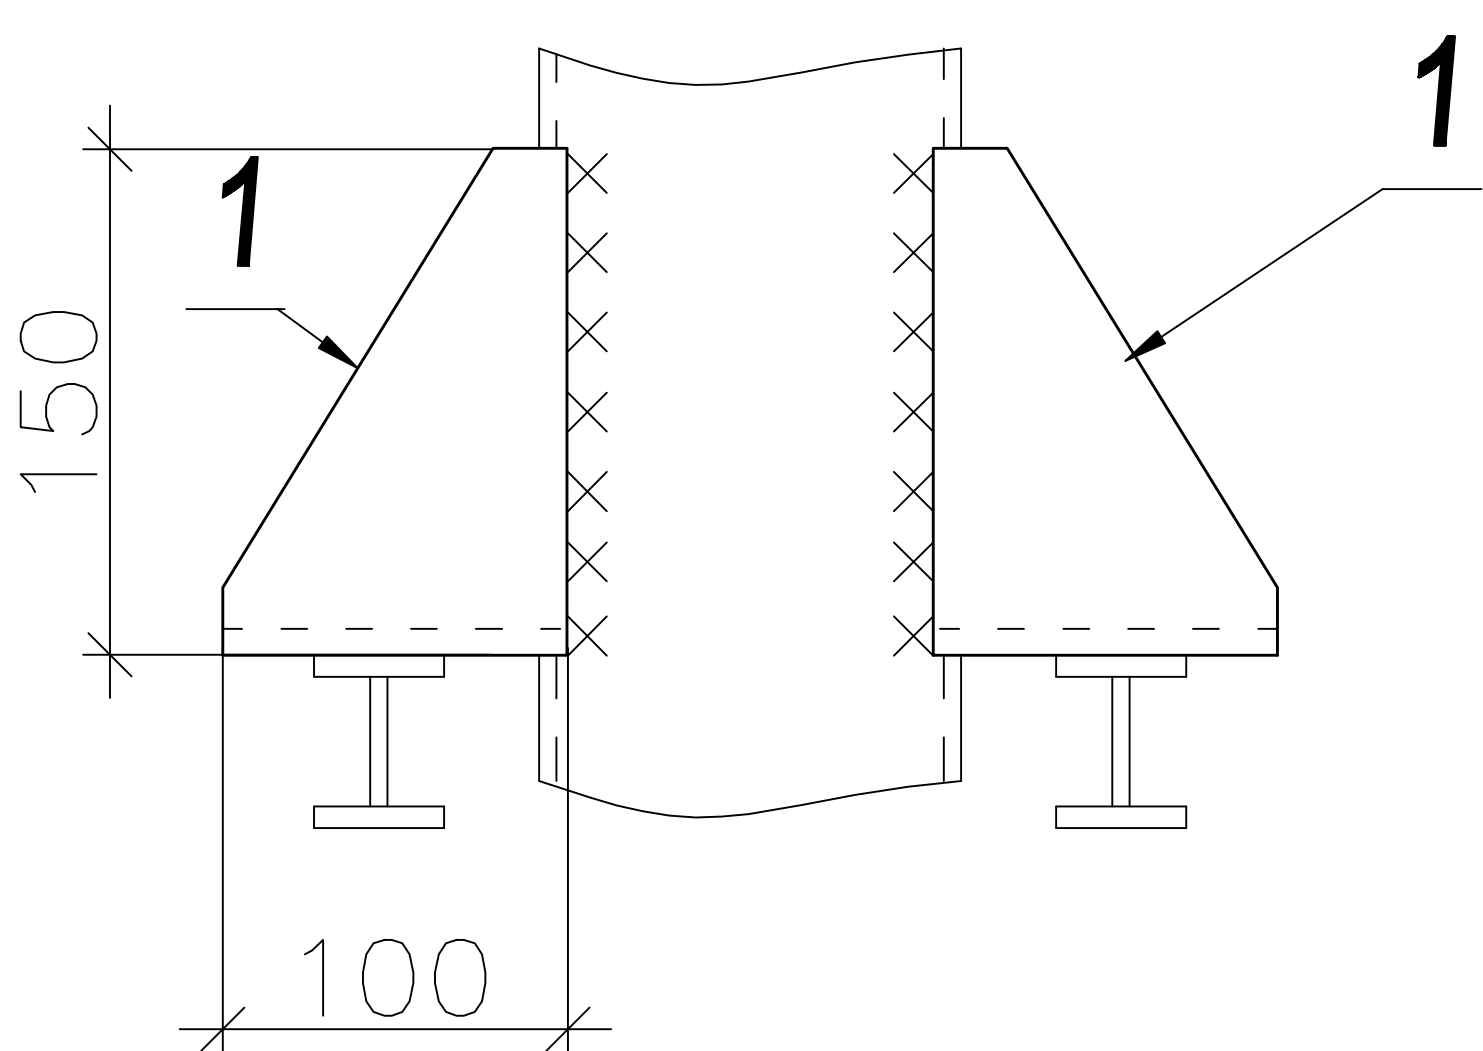
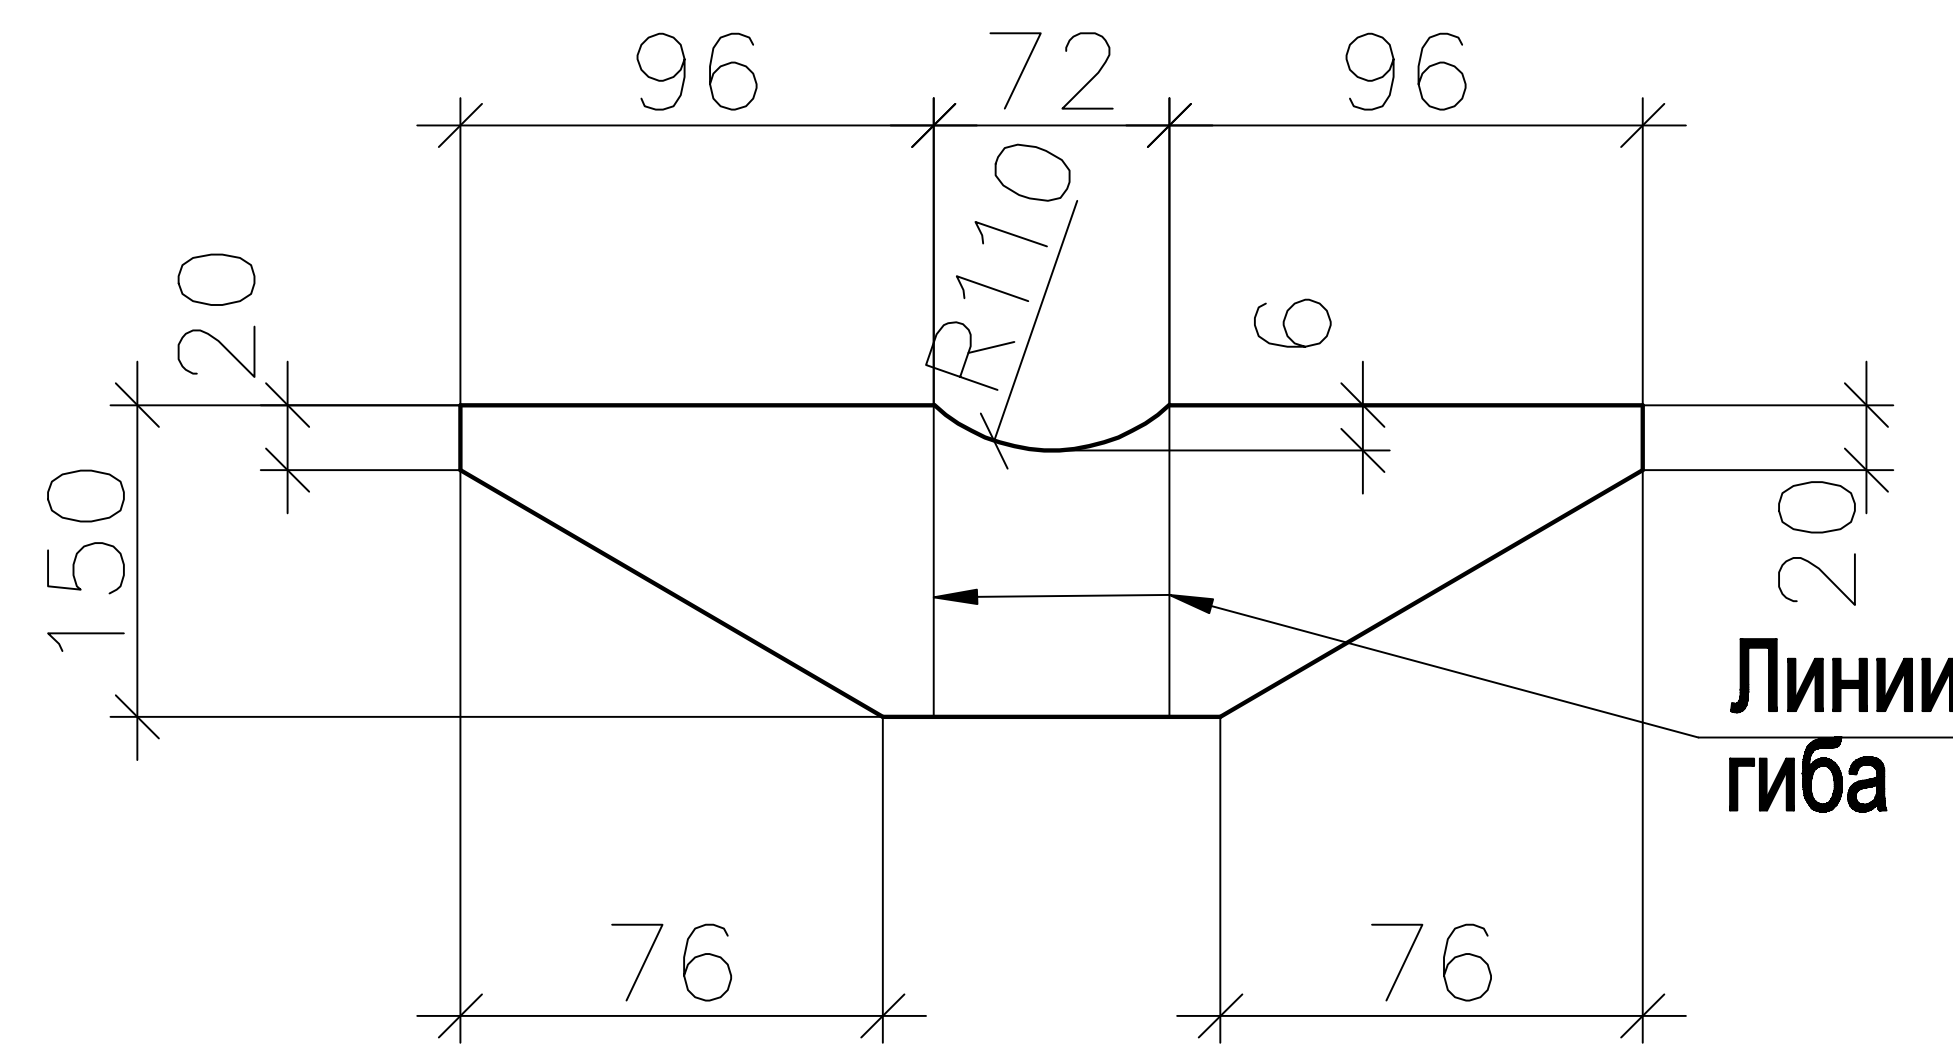


219-ВП-A1  Развертка поз.1 					Выборка металла				
					Материал		Сечение	Масса в кг	ГОСТ
					ГОСТ 19281-89	09Г2С	лист 4	2,48	19903-74
Итого			2,48	кг					

Поз.1

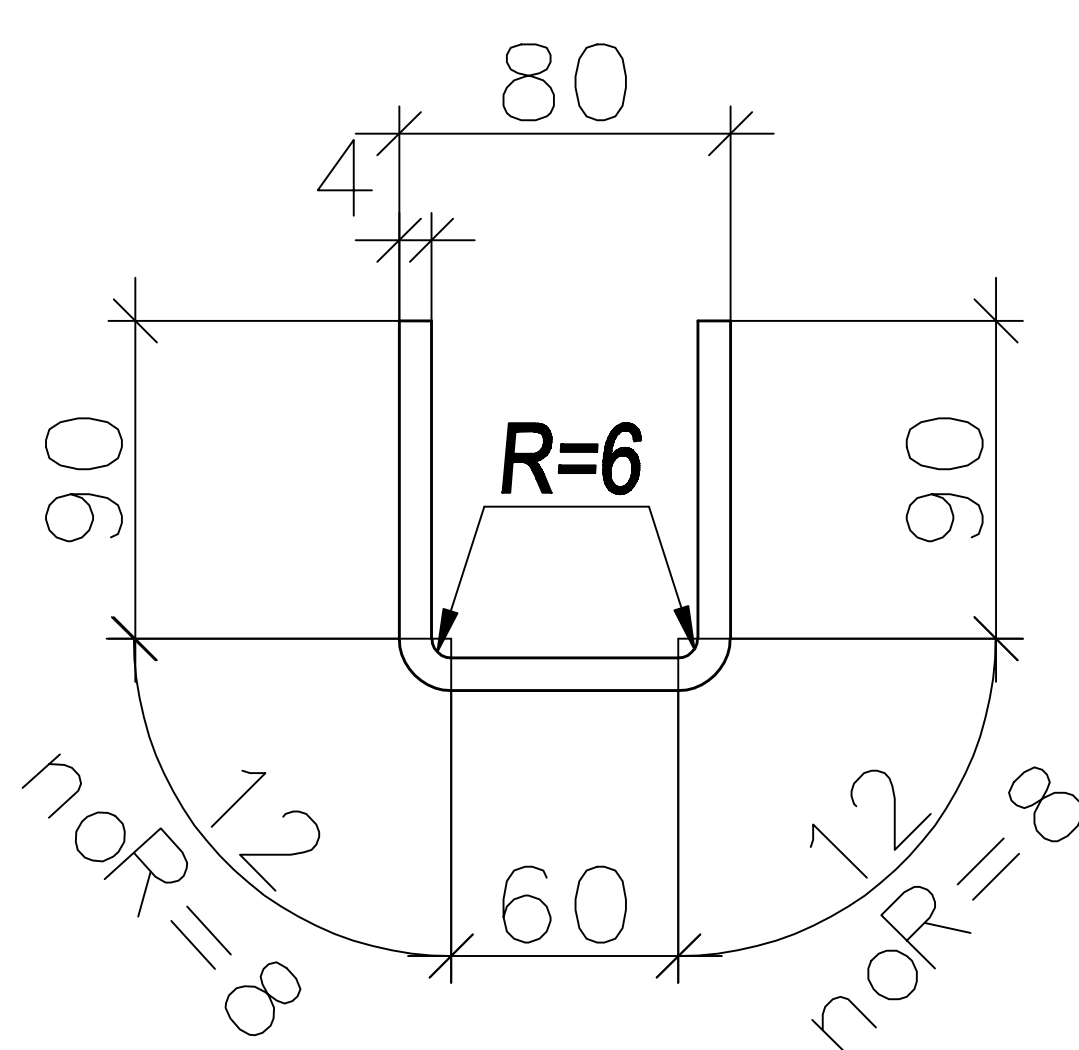

Примечания:

1. На заводе окрасить грунтом ГФ-021 по ГОСТ 25129-82 в два слоя.

2. Значения предельных отклонений размеров по Н14, h14, ±IT14/2.

3. Острые кромки притупить радиусом 0,5 мм.

4. Опору маркировать 219-ВП-A1.

	1	2		- 150 x 4	264	0,9	1,8	1,8		ф.л.гнуть
ОТПР.		Т.	Н.	СЕЧЕНИЕ	ДЛИНА	ШТ.	ОБЩ.	ЭЛЕМ.	МАРКА СТАЛИ	ПРИМЕЧАНИЯ
ЭЛЕМ.	ДЕТ.	КОЛ-ВО				МАССА В КГ				

СПЕЦИФИКАЦИЯ СТАЛИ 09Г2С ГОСТ 19281-89

				007.ОС.219.ВП.000.1240.00				
Исполнил				Опора 219-ВП-A1		Стадия	Лист	Листов
Проверил						Р	1	1
Рук.груп.				ОСТ 36-146-88		ООО НПП "Строительные технологии"		
Гл.конст.								
Гл.техн.								
Гл.инж.	Немиров							