
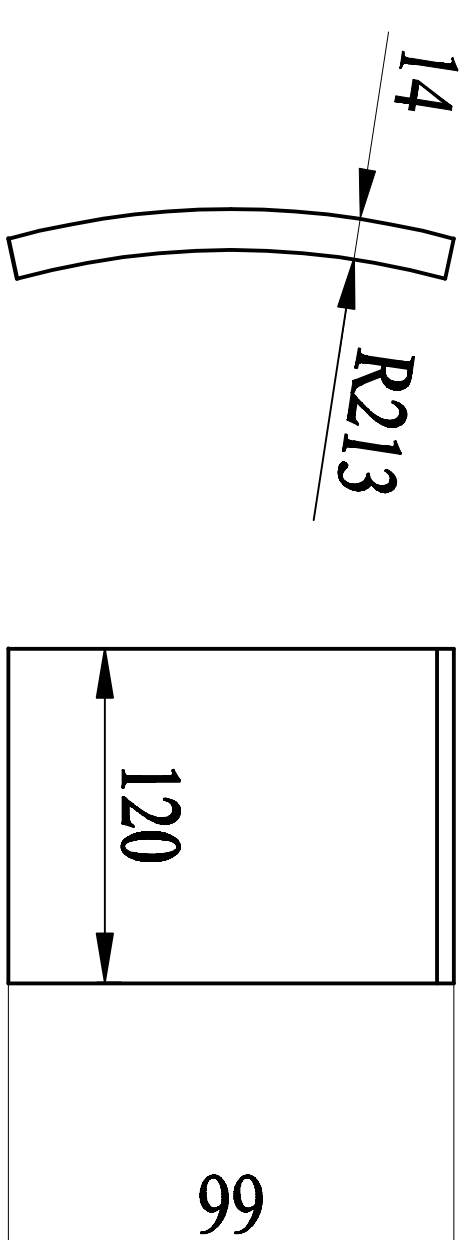





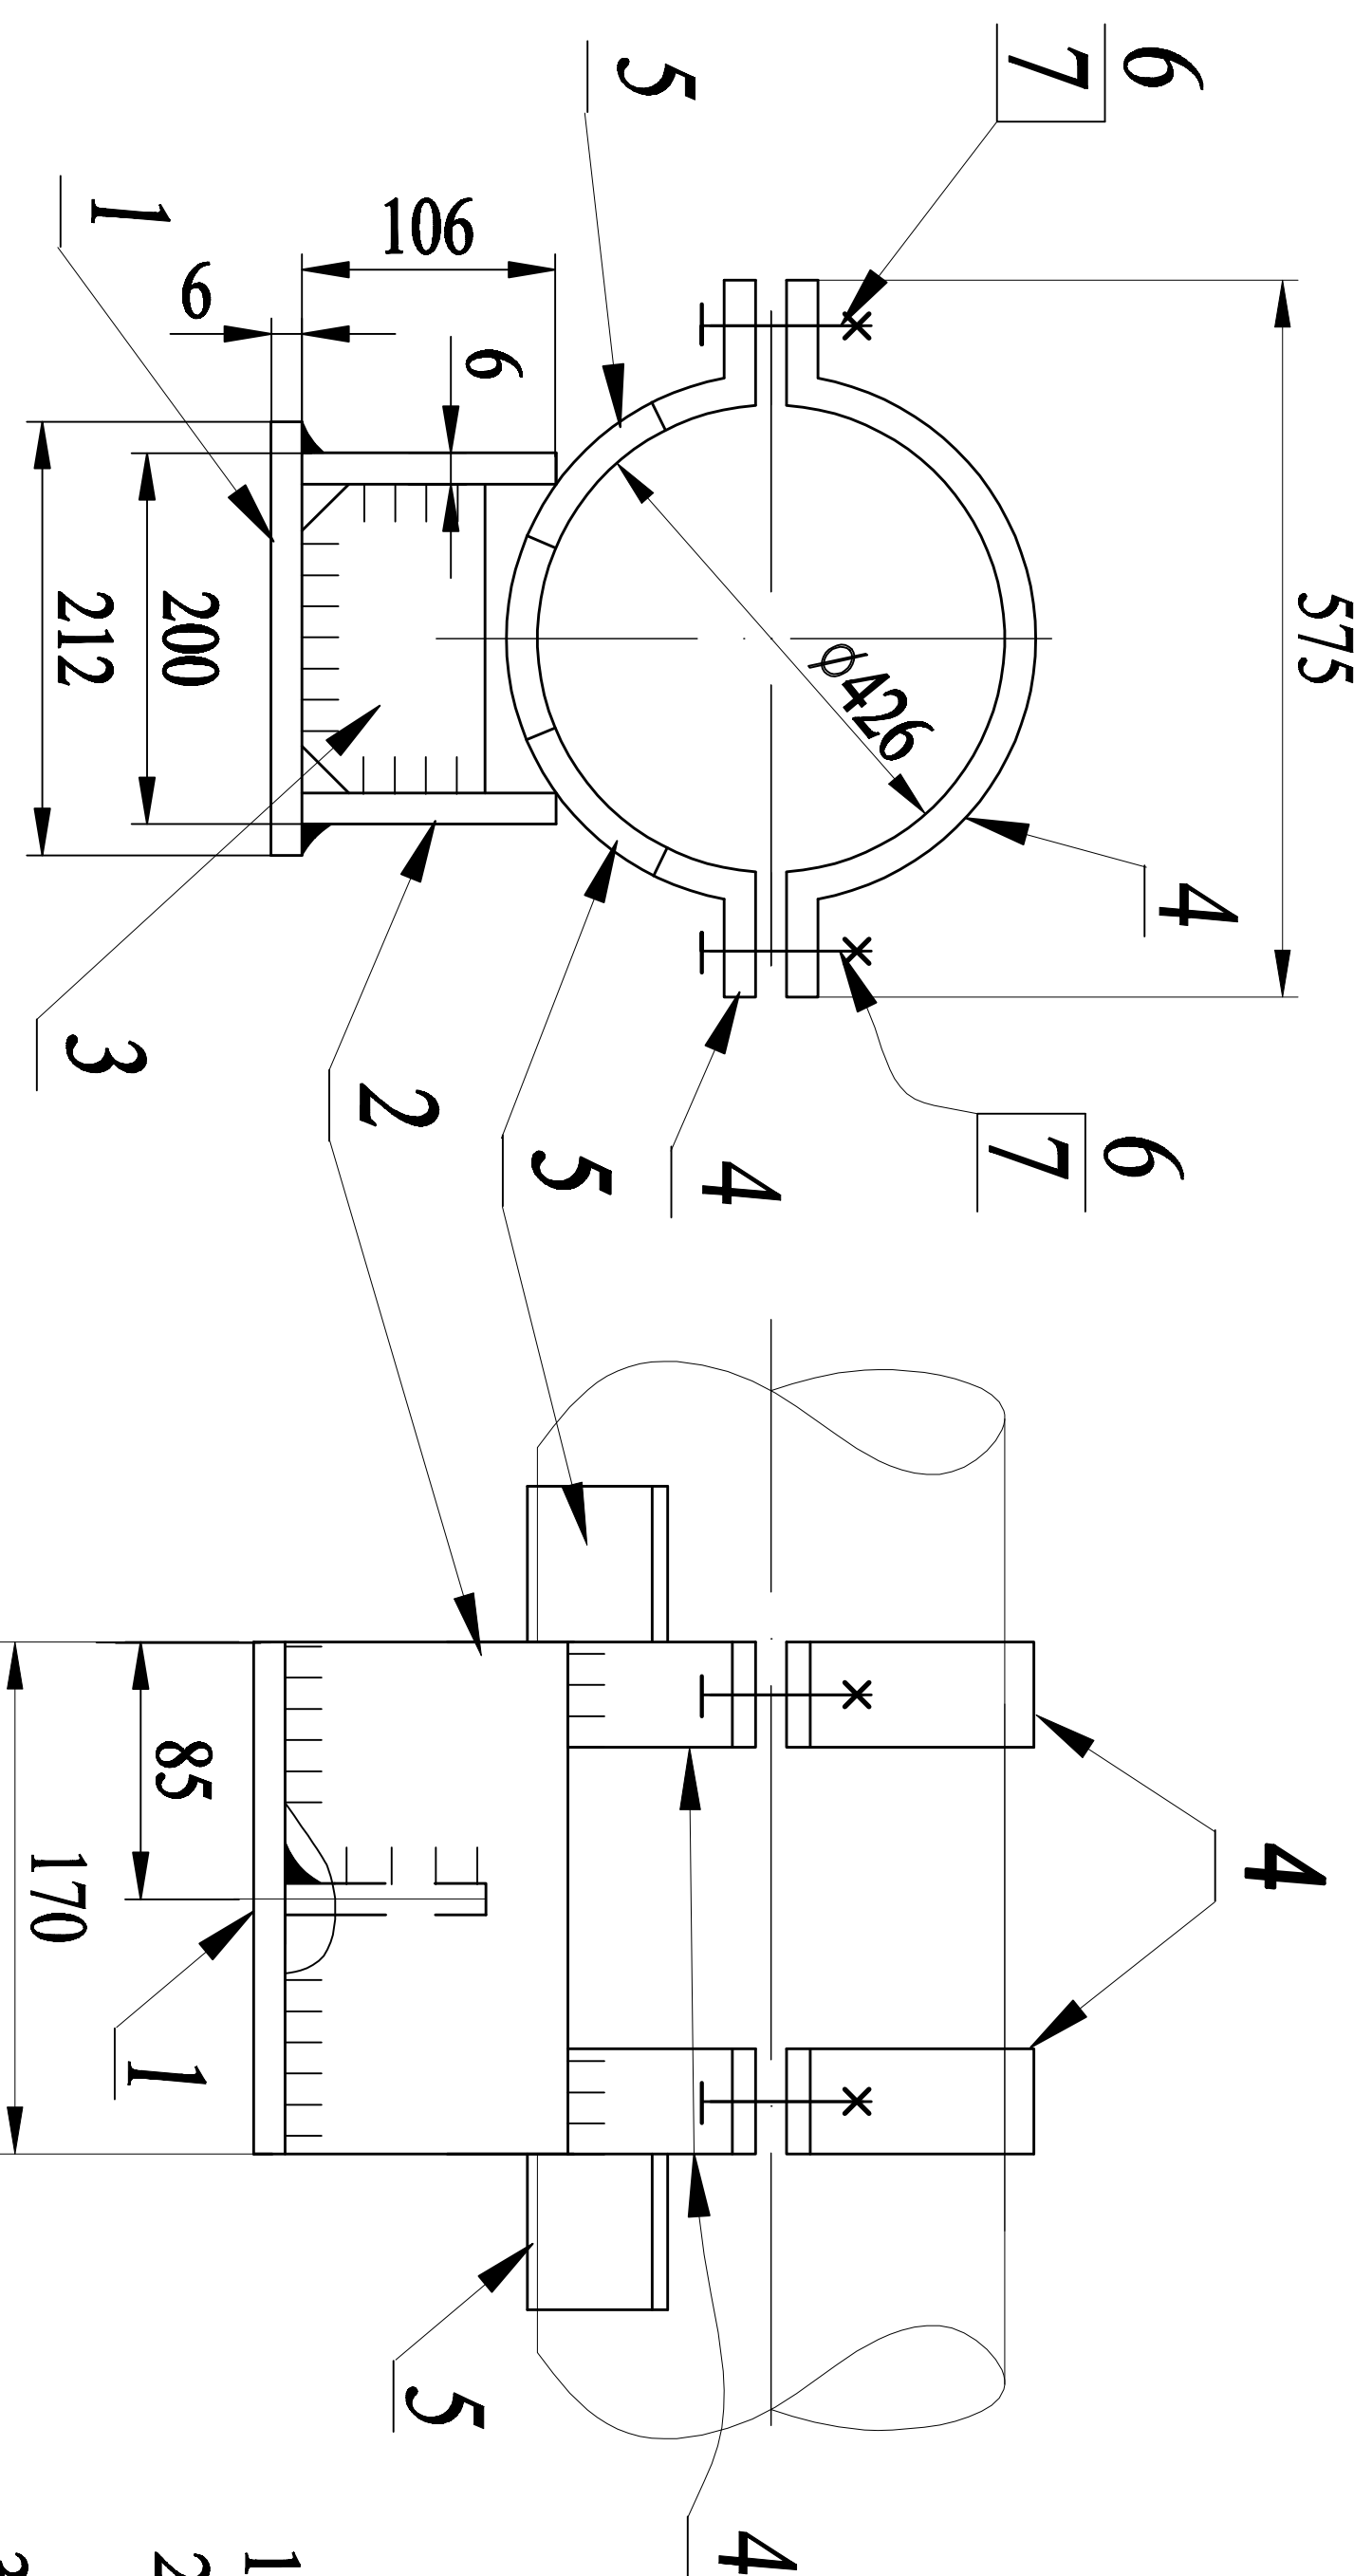


Выборка металла				
ГОСТ 19281-88	Материал	Сечение	Масса в кг	ГОСТ
	09Г2С			
	лист 6		4,2	
	лист 10		14,68	
	лист 14		5,28	
	Гайка М20		0,28	
болт М20х60		0,87		

ПРИМЕЧАНИЯ:

1. Сварные швы - 6 мм
2. Сварка полуавтоматическая по ГОСТ 14771-76 в среде СО₂. Сварочная проволока Св-08Г2С по ГОСТ2246-70 диаметром 1,4-2,0 мм.
3. На заводе окрасить грунтом ГФ-021 по ГОСТ 25129-82 в два слоя.
4. Не указанные предельные отклонения размеров по Н 14. h 14. ± IT 14/2
5. Опору маркировать: 426-КХ-АС11

Копије

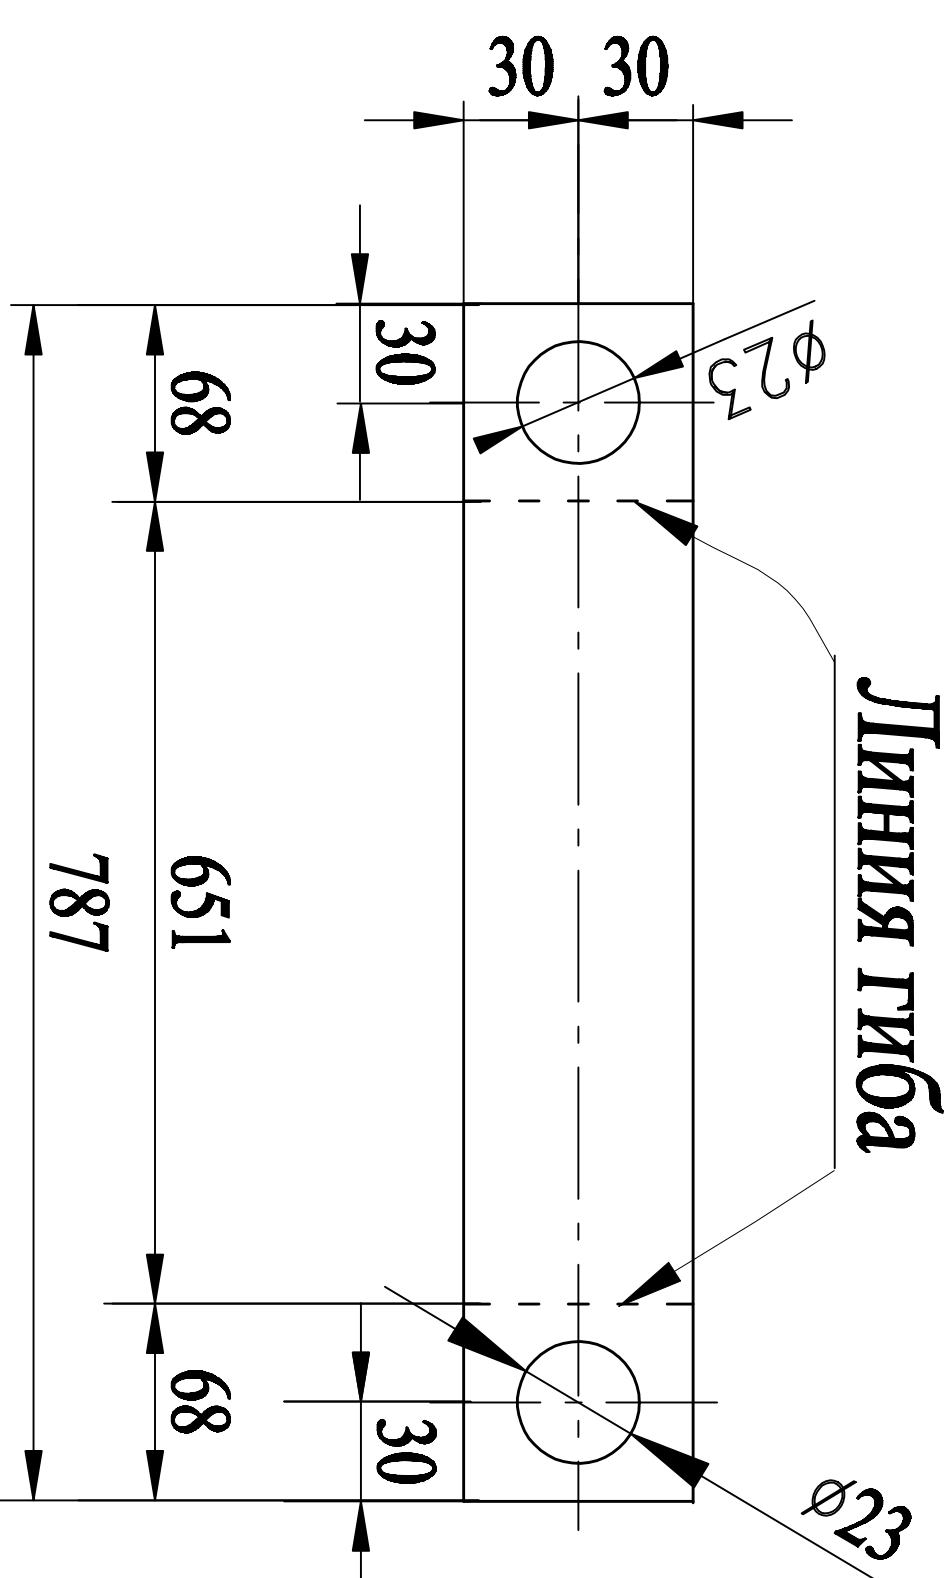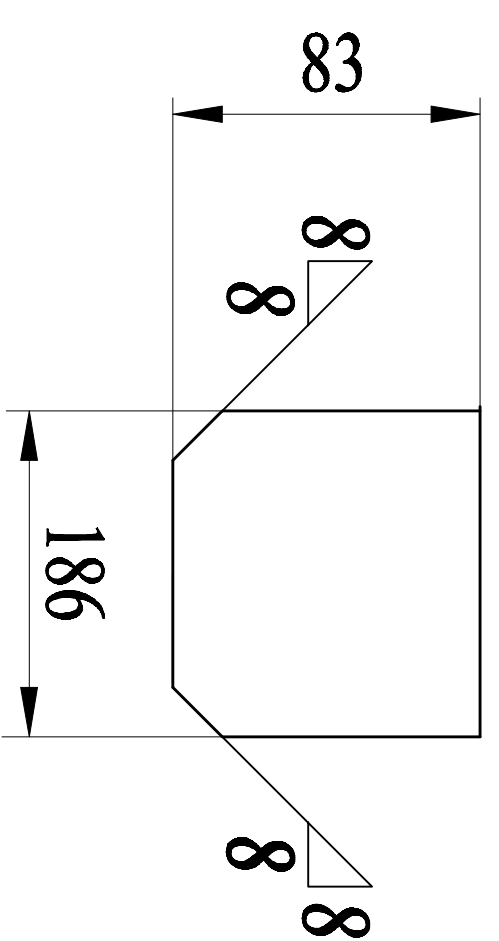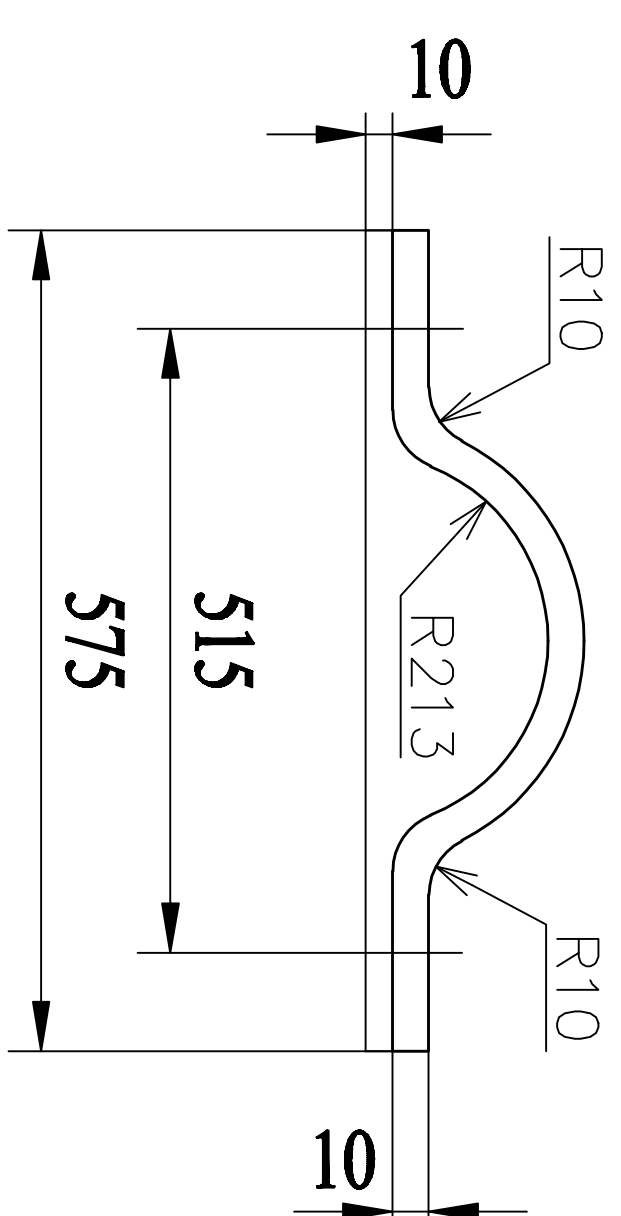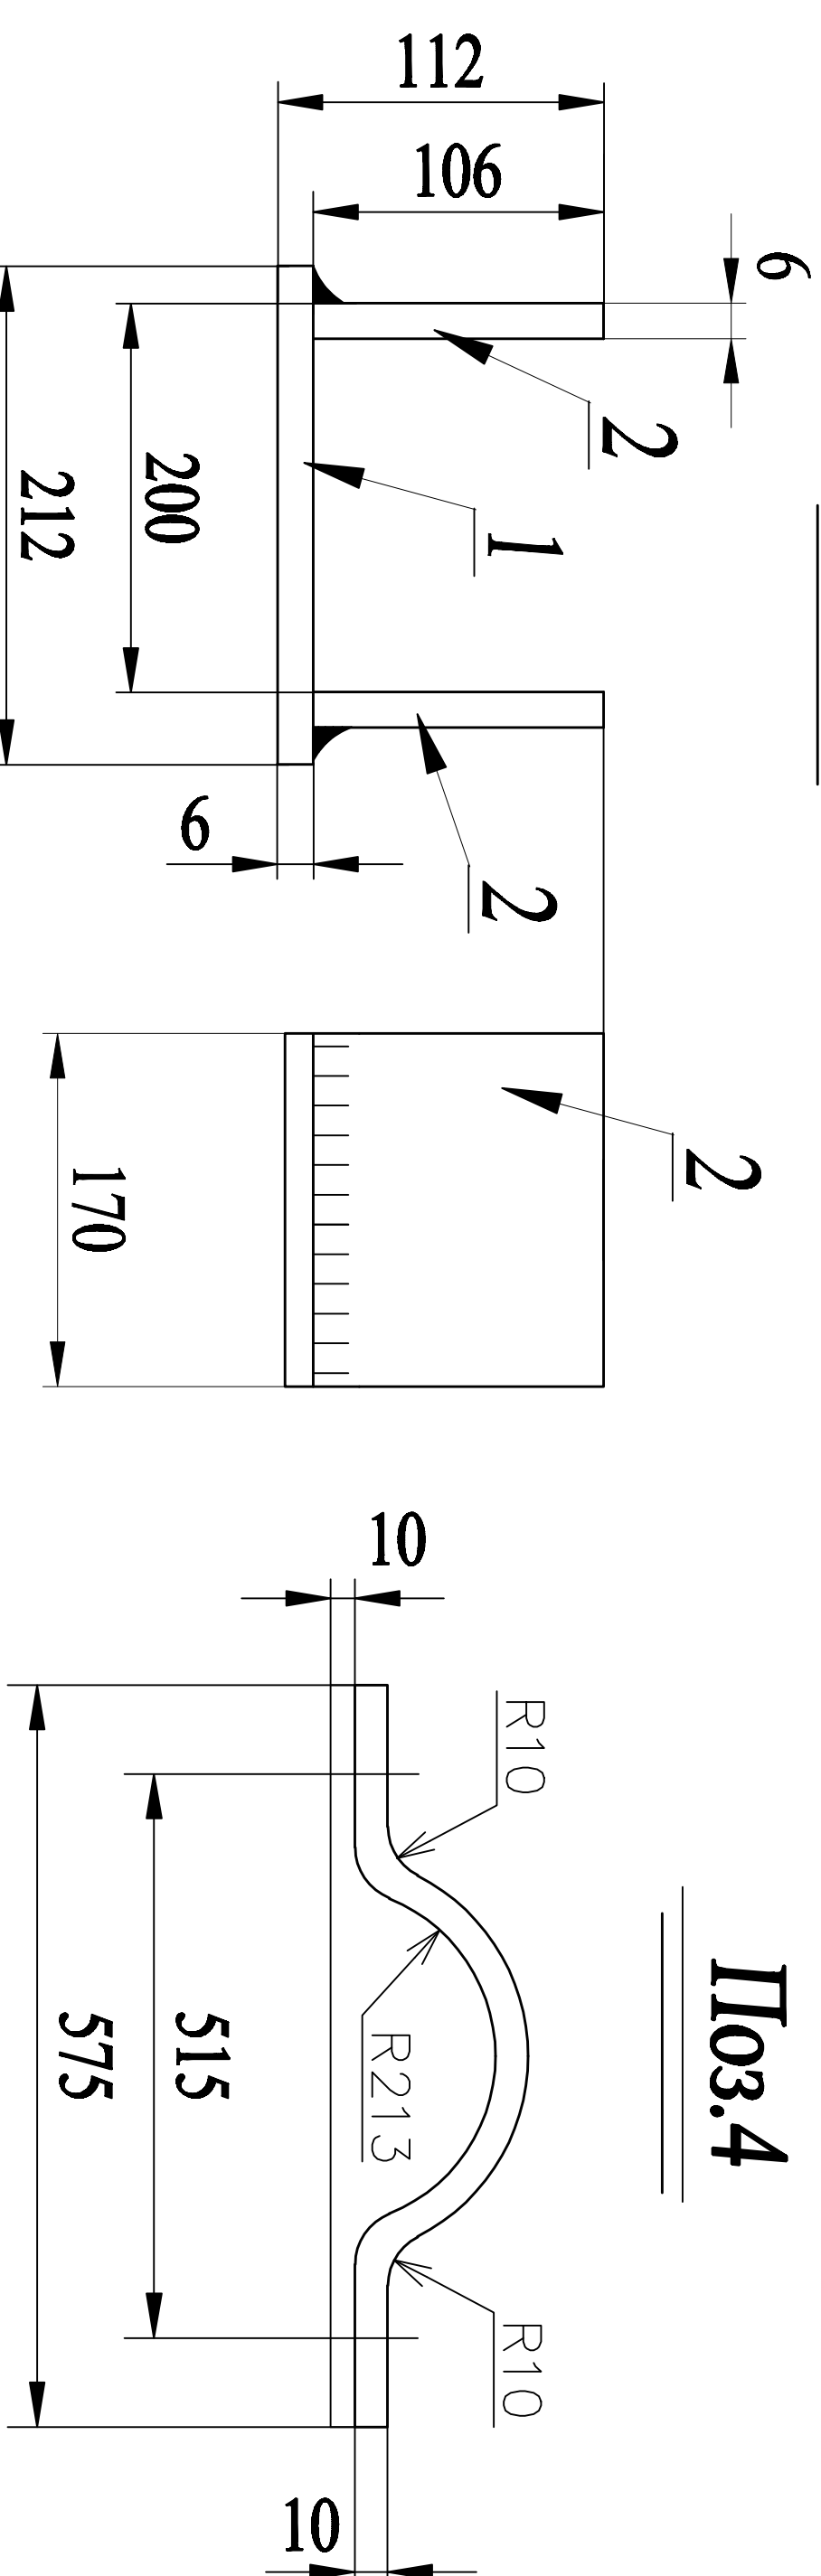

Поз.4

14

R213

120

99

Выборка металла			
Материал	Сечение	Масса в кг	ГОСТ
ГОСТ 19281-88 09Г2С	лист 6	4,2	
	лист 10	14,68	
	лист 14	5,28	
	Гайка М20	0,28	
	болт М20х60	0,87	
Итого		25,31	кг

Примечания:

1. Сварные швы - 6 мм

2. Сварка полуавтоматическая по ГОСТ 14771-76 в среде СО2. Сварочная проволока Св-08Г2С по ГОСТ2246-70 диаметром 1,4-2,0 мм.

3. На заводе окрасить грунтом ГФ-021 по ГОСТ 25129-82 в два слоя.

4. Не указанные предельные отклонения размеров по Н 14. h 14. ± IT 14/2

5. Опору маркировать: 426-КХ-АС11

--	--	

Π03.3

Развертка ПОЗ.4

Π03.4

Линия тйба

СПЕЦИФИКАЦИЯ СТАЛЫ 09Г2С ГОСТ 19281-88

007.0C.426.KX.101.0907.01

Опора 426-KX-AC11

Страница	Лист	Лист
Р	1	1

000 VIII

"Строительные технологии"