


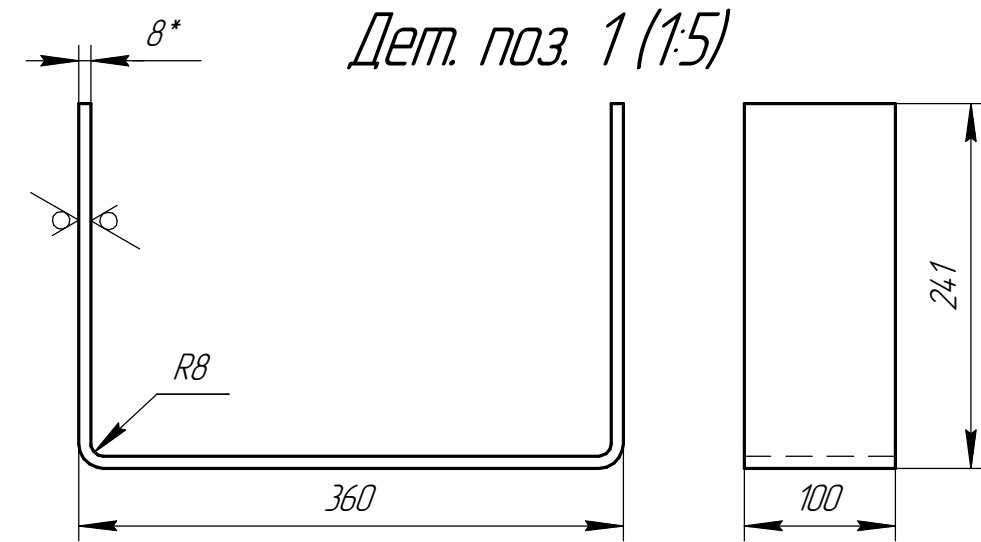
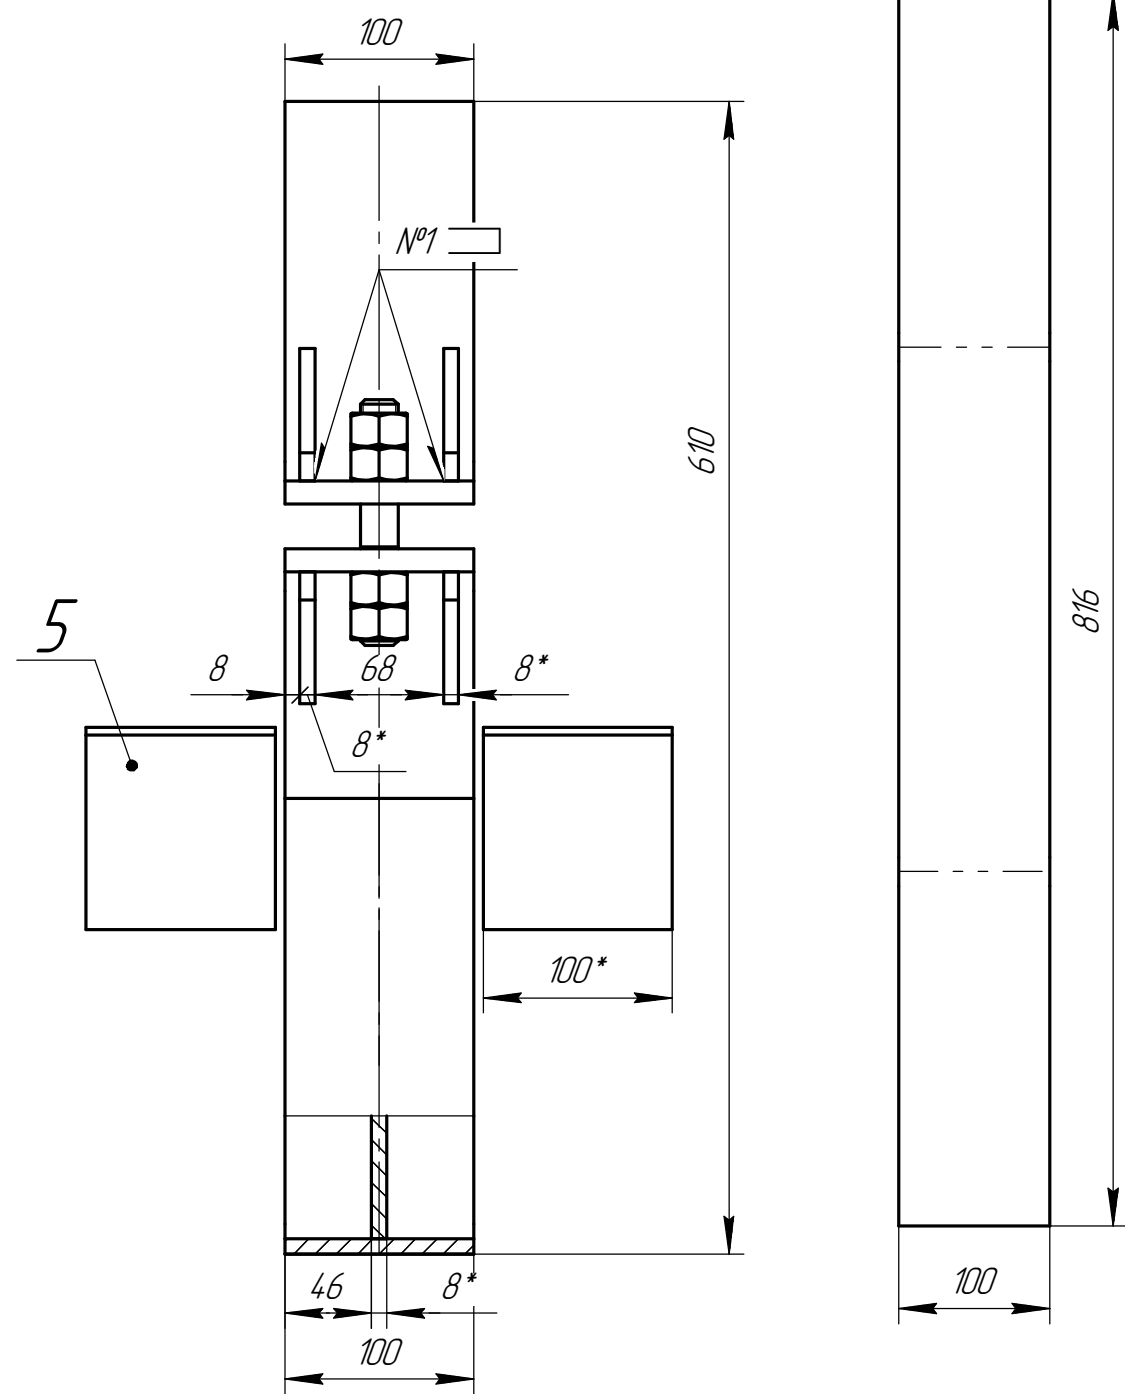
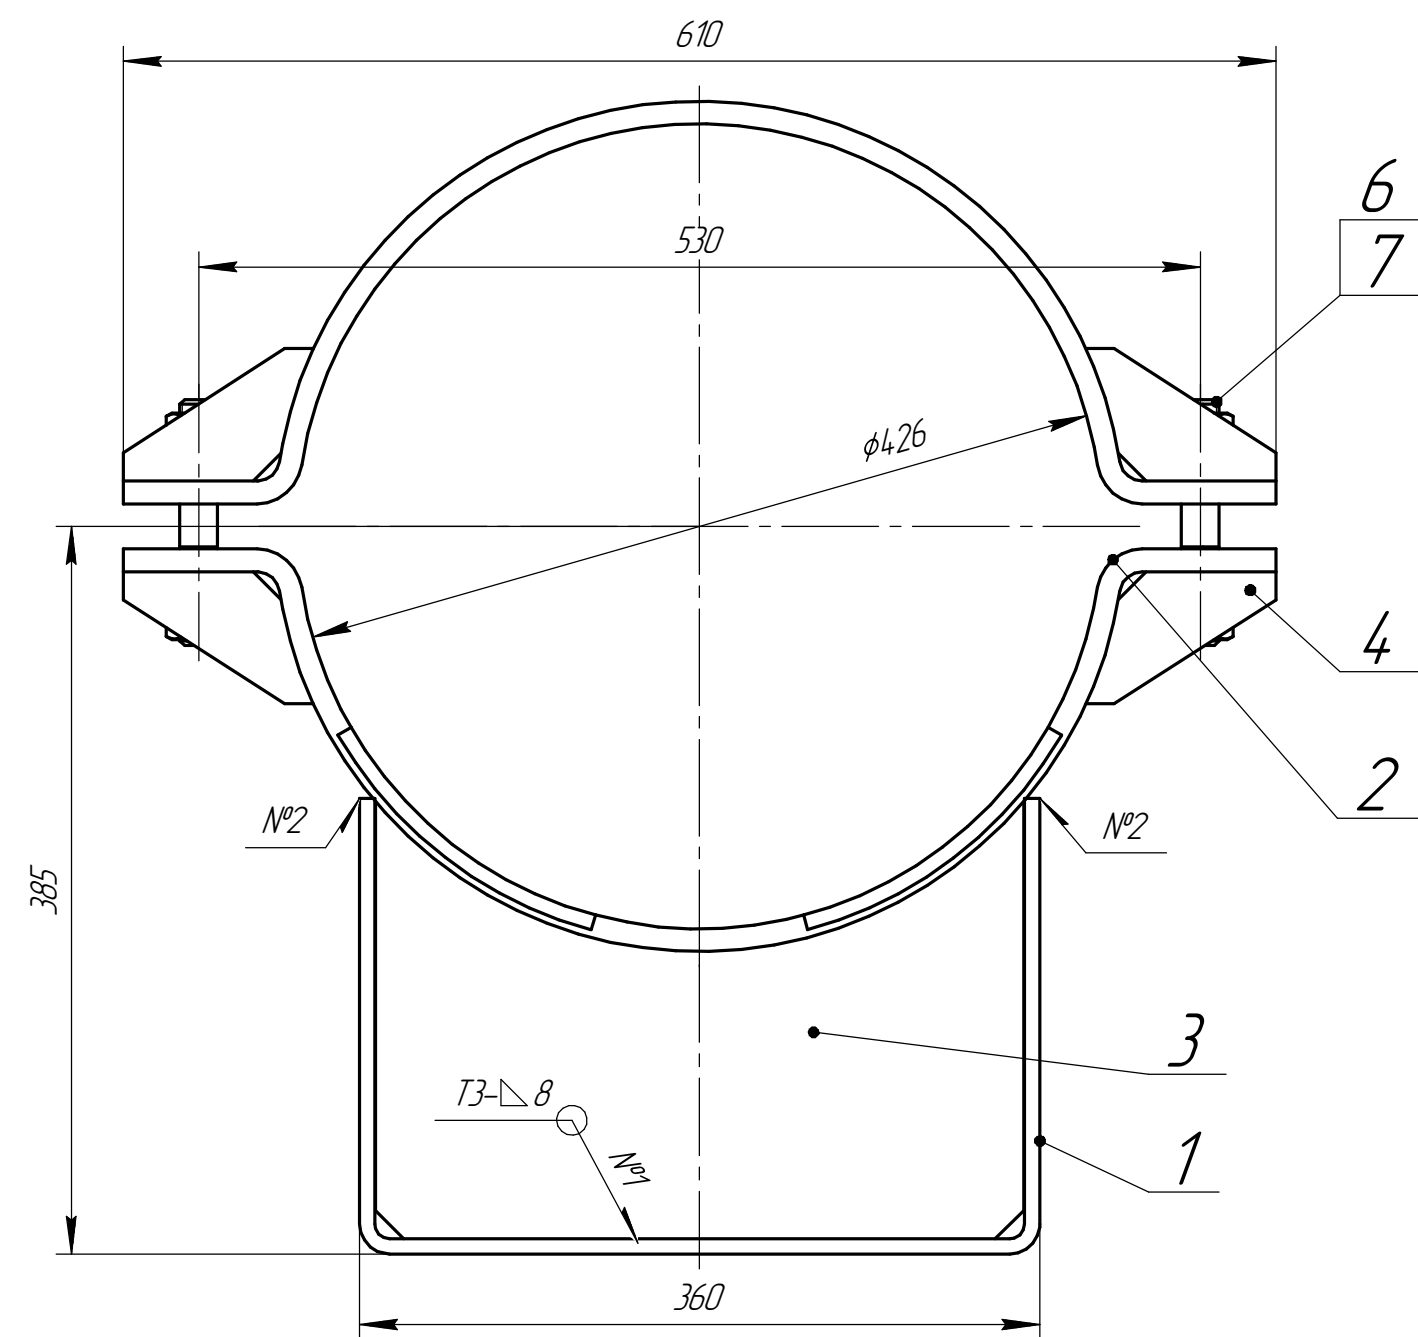


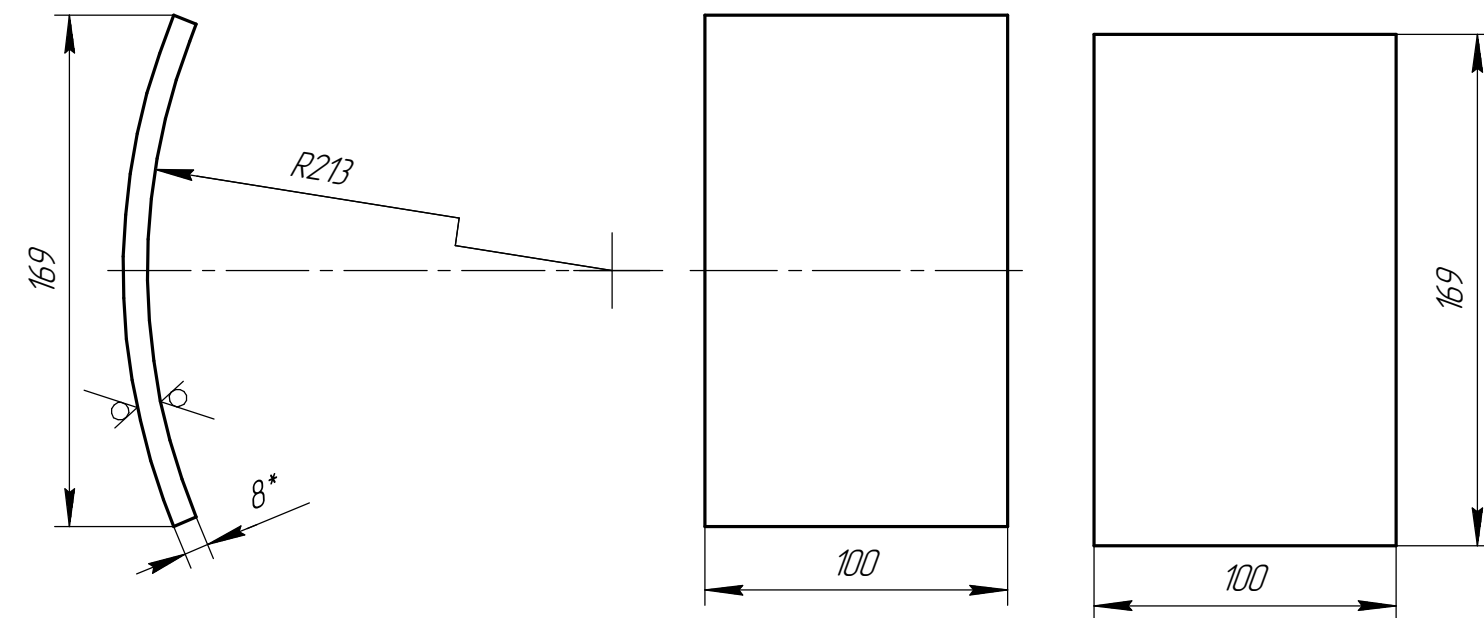


Det. poz. 5 (1:2,5)

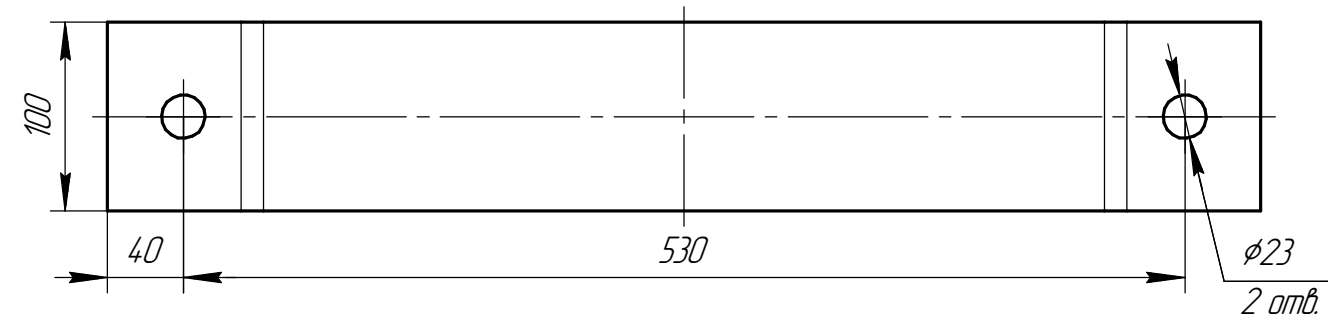


Det. poz. 2

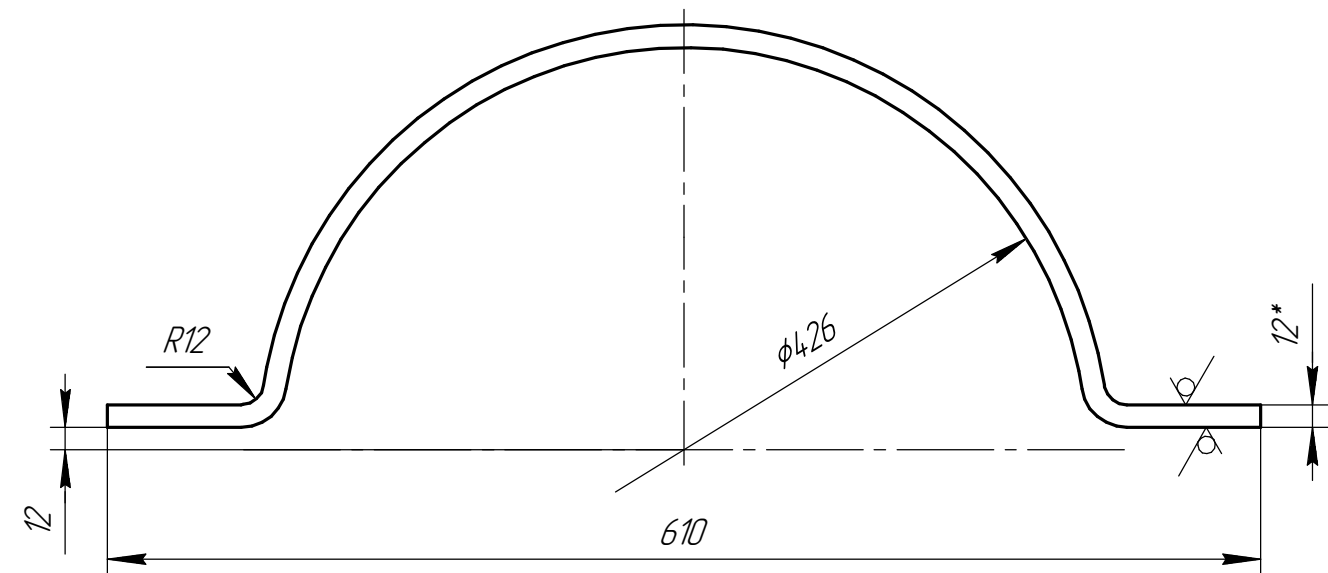


Q (1:5)

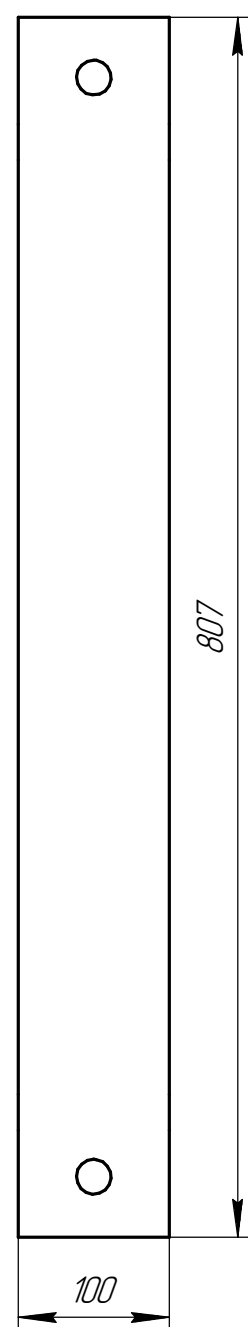

Det. poz. 4 (1:2)

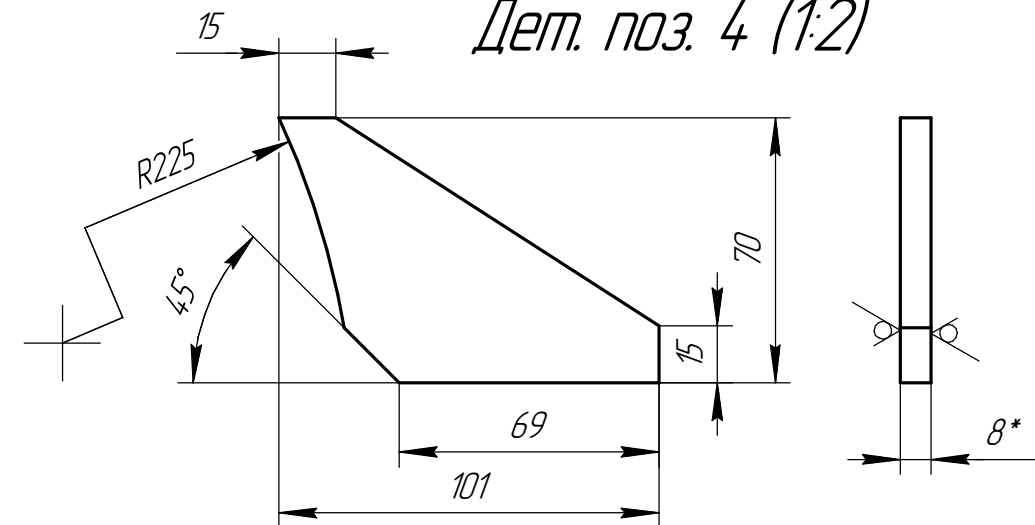

Det. poz. 3

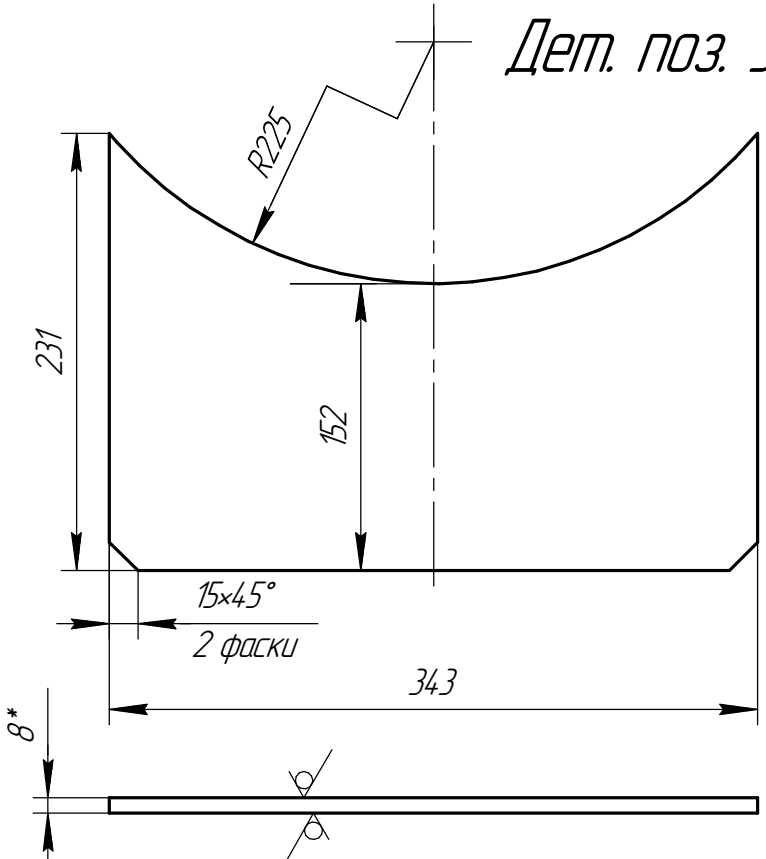

1. Общие допуски по ГОСТ 30893.1: H17, h17, ±IT17/2.
2. *Размеры для справок.
3. Материалы:
 - Лист ГОСТ 19903-2015, 09Г2С ГОСТ 19281-2014;
 - Сварочная проволока Св-08Г2С ГОСТ 2246-70.
4. Сварка по ГОСТ 14771-76.
5. Основные технические требования по СТО 79814-898 131-2009.
6. Площадь покрытия 1,03 м².

Поз.	Обозначение	Наименование	Кол	Прим.
1	816х100х8	Карпус	1	5,12 кг
2	807х100х12	Полухомут	2	7,59 кг
3	231х34-3х8	Ребра	1	3,78 кг
4	101х70х8	Косынка	8	0,24кг
5	169х100х8	Упор	4	1,07 кг
6		Шпилька М20-6дх130.88.40Х ГОСТ 22042-76	2	0,285 кг
7		Гайка М20-6Н.8.35 ГОСТ 5915-70	8	0,071 кг

					Опора 055 СТО 79814-898 131-2009			
Изм./Лист	№ докум.	Подп.	Дата		Опора хомутовая неподвижная			
					Лит.	Масса	Масштаб	
						33,3	1:4	
					Лист	Листов 1		
Н.контр.								
Утв.								