
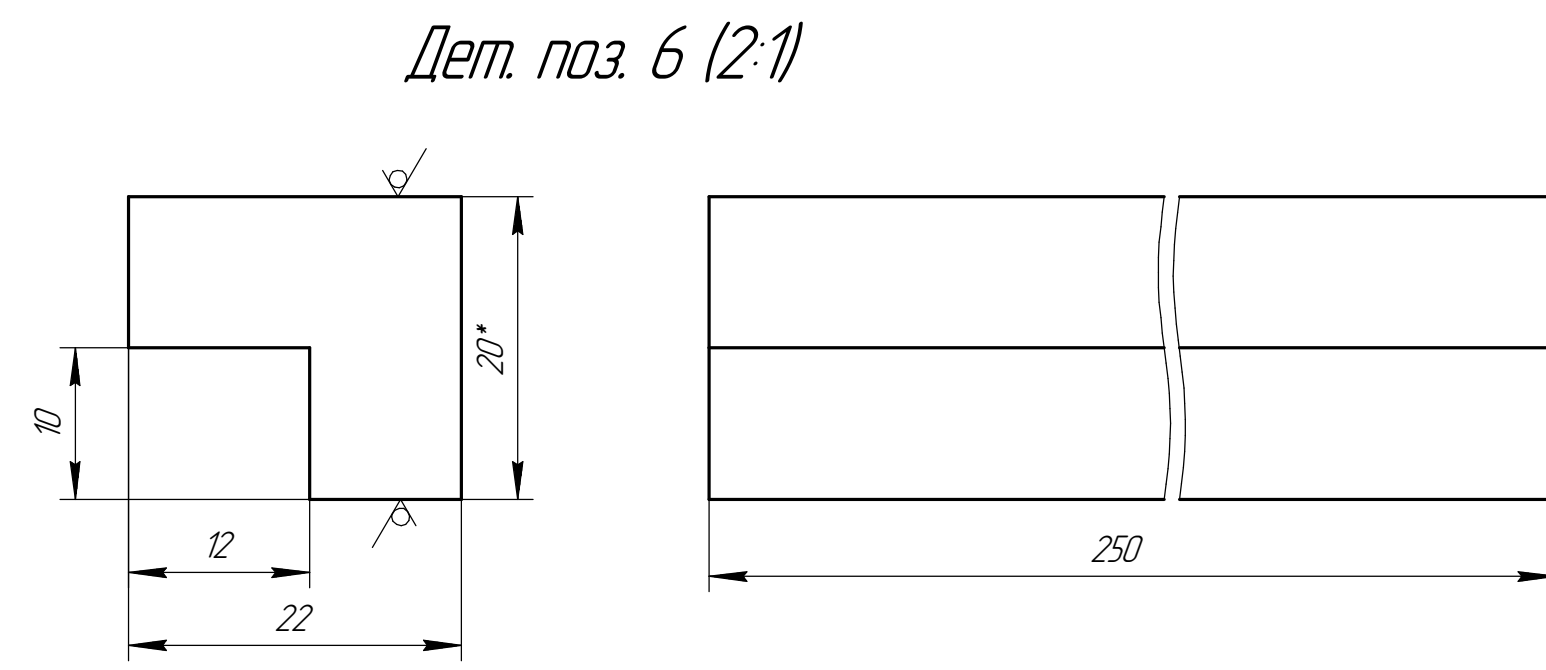
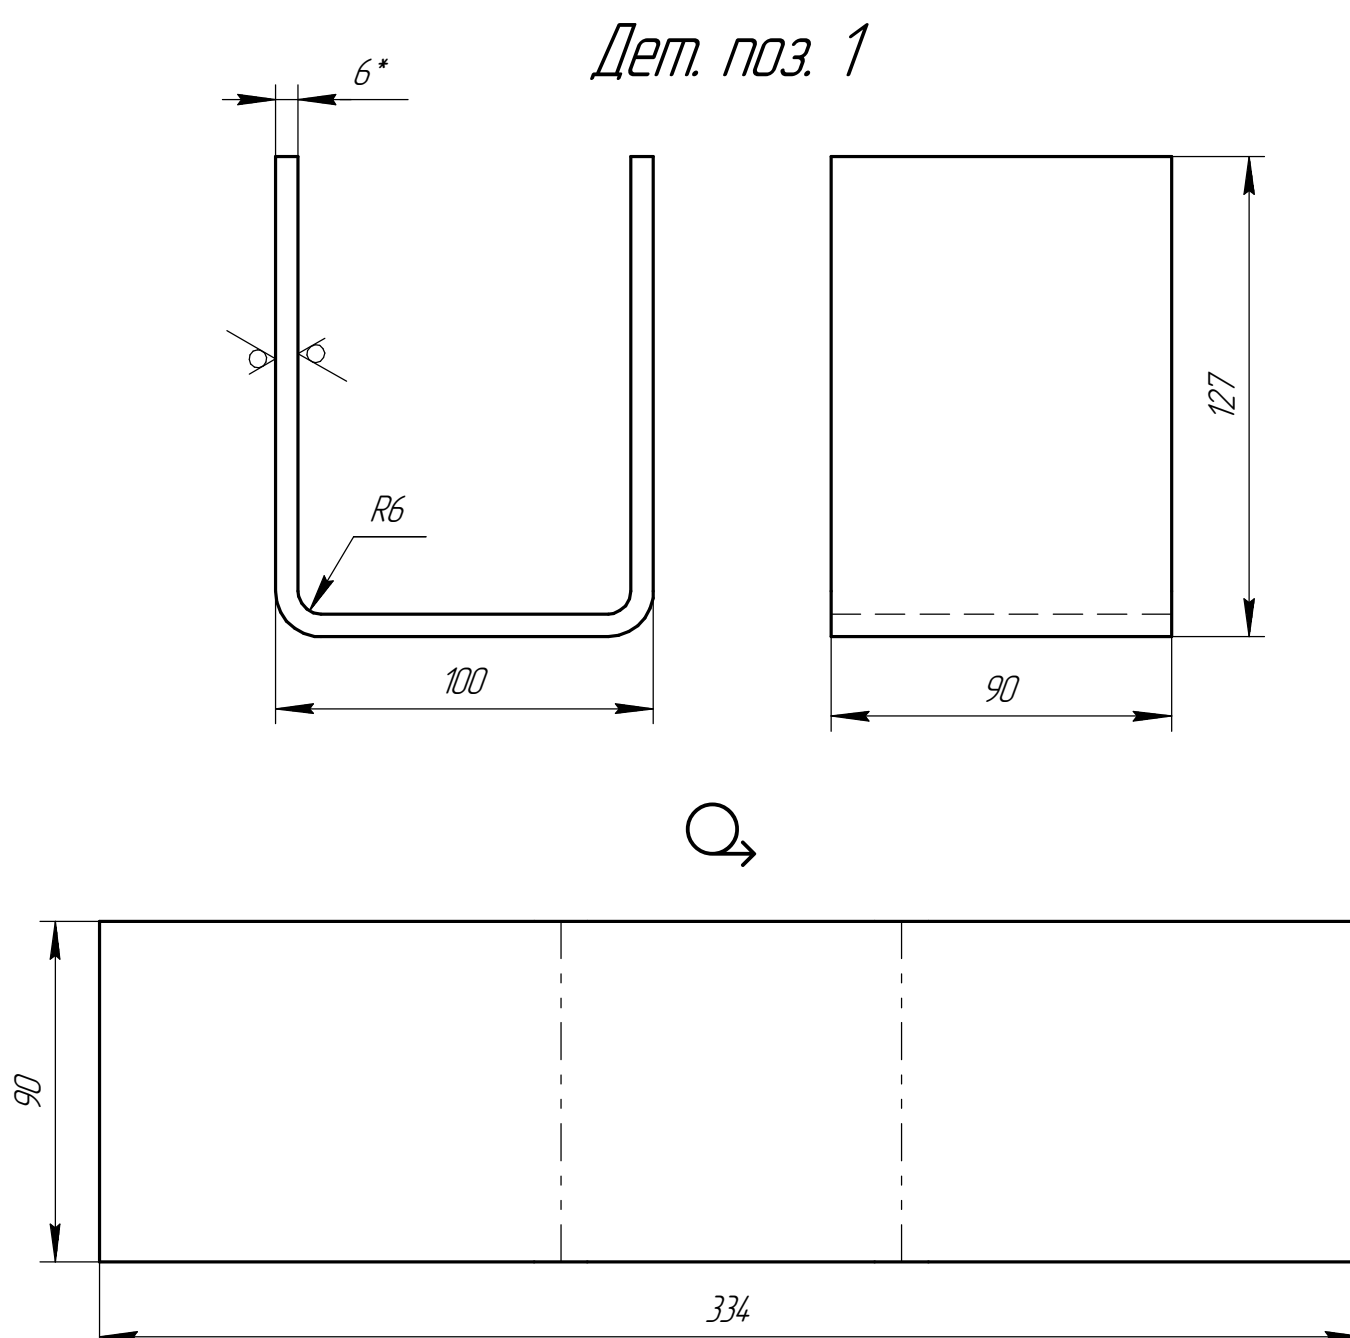
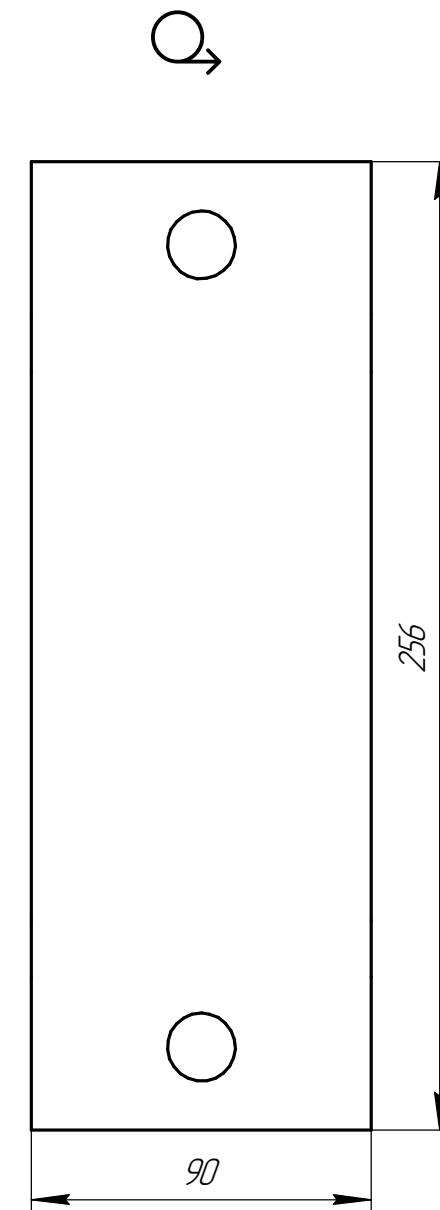
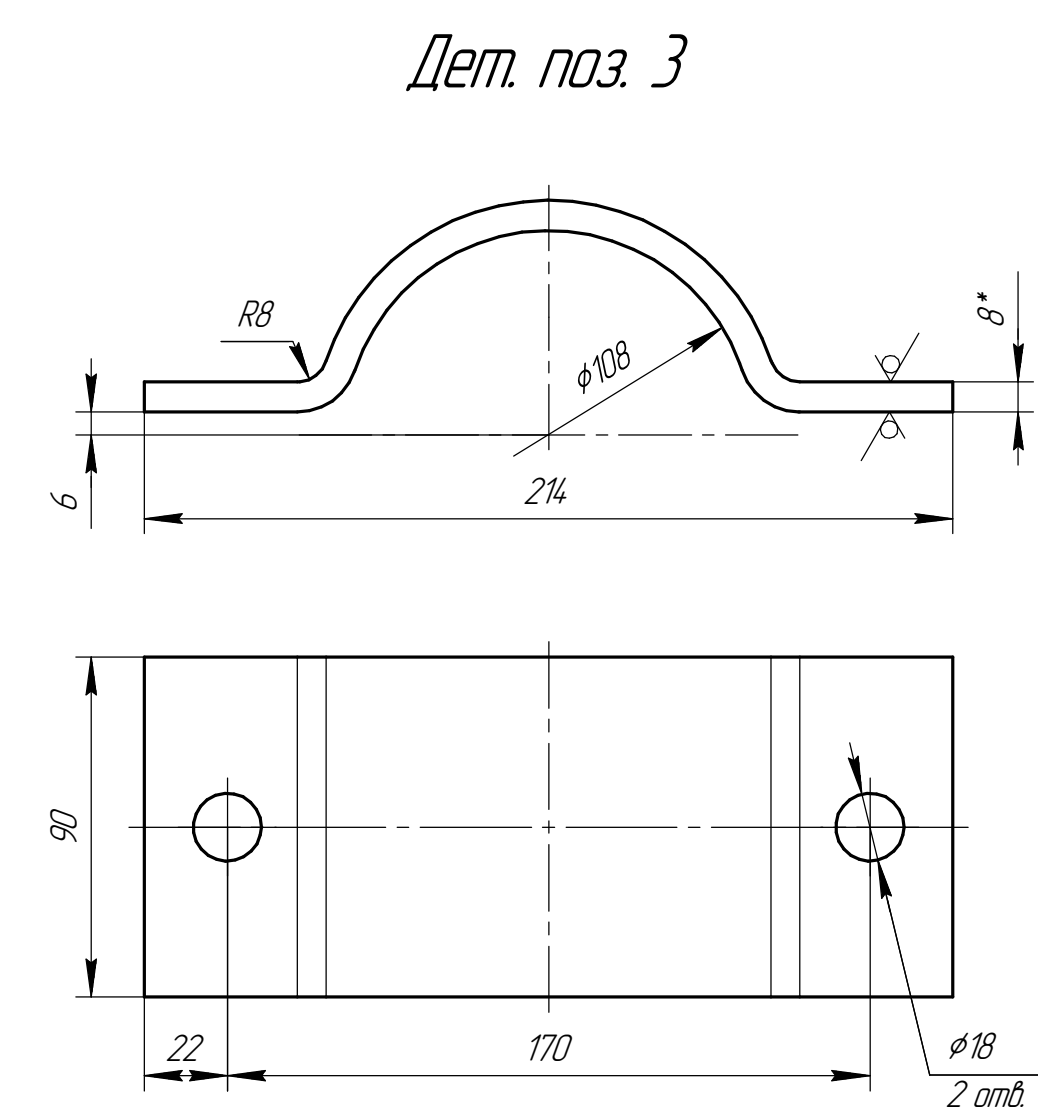
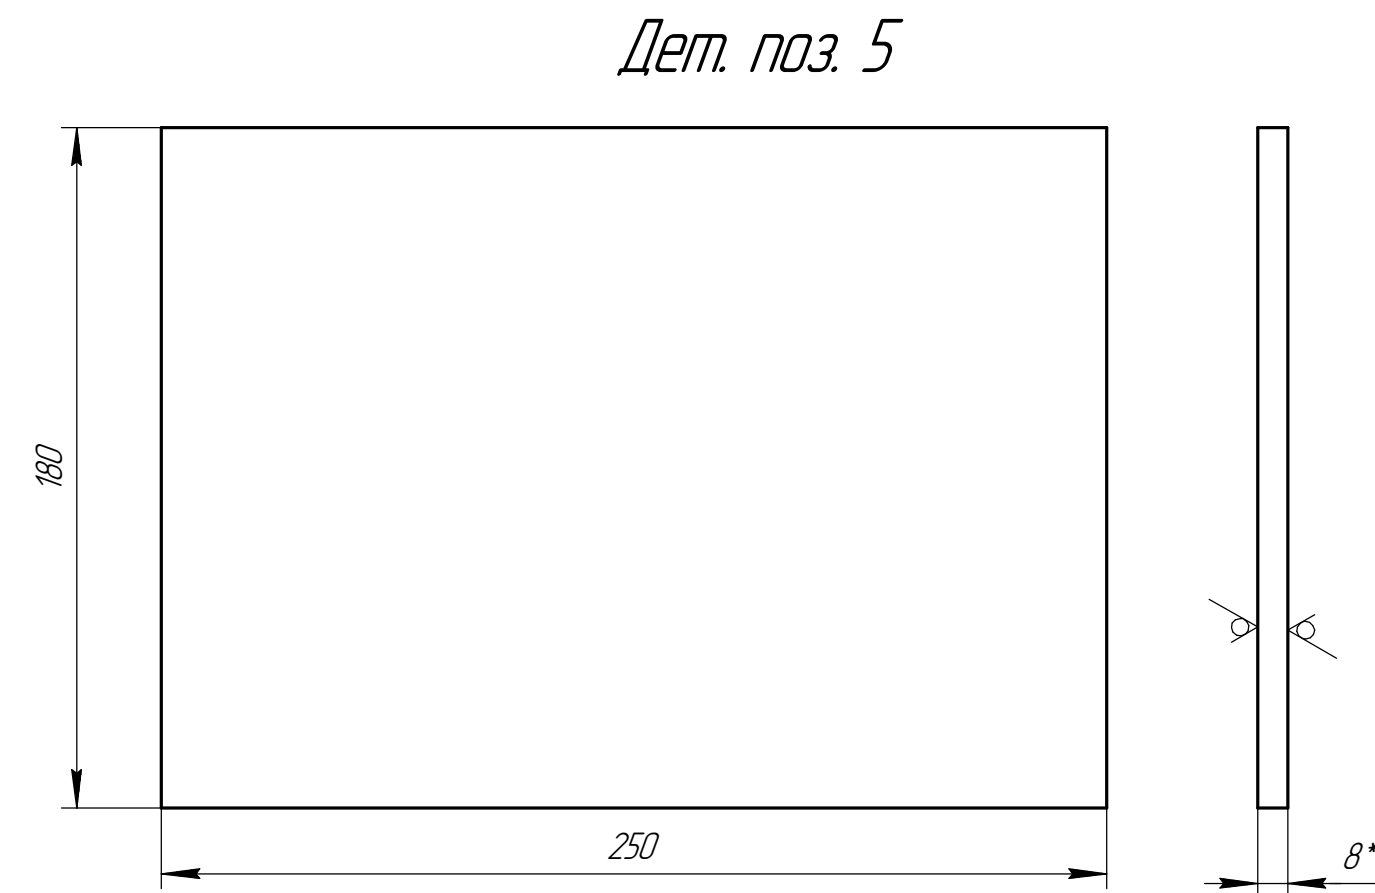
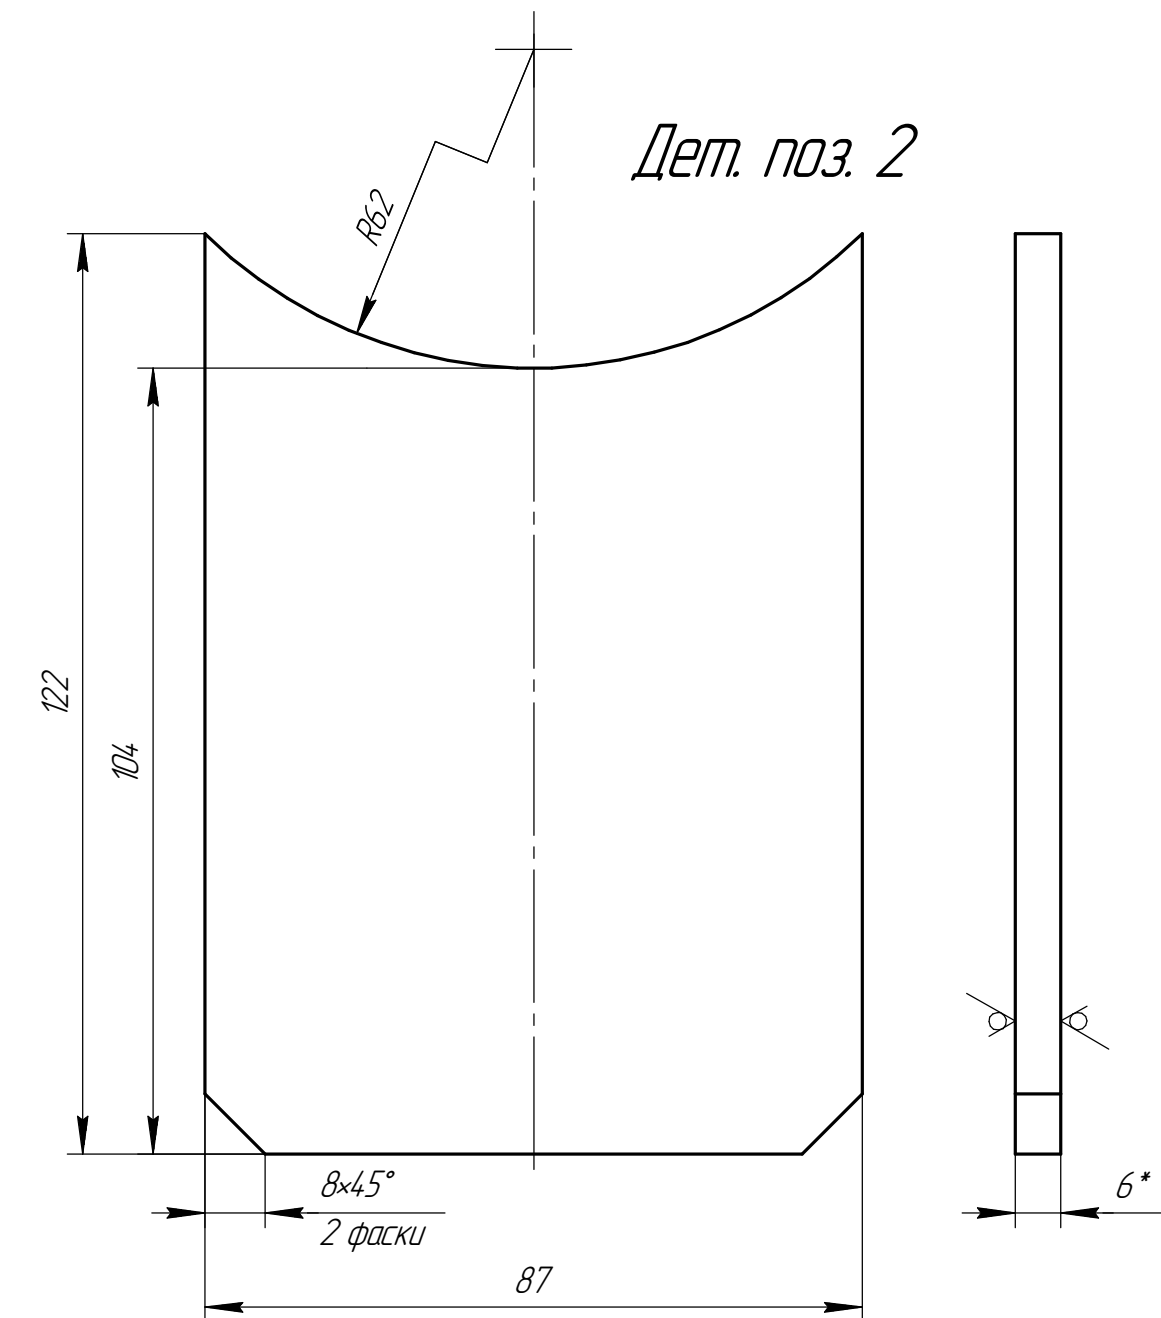
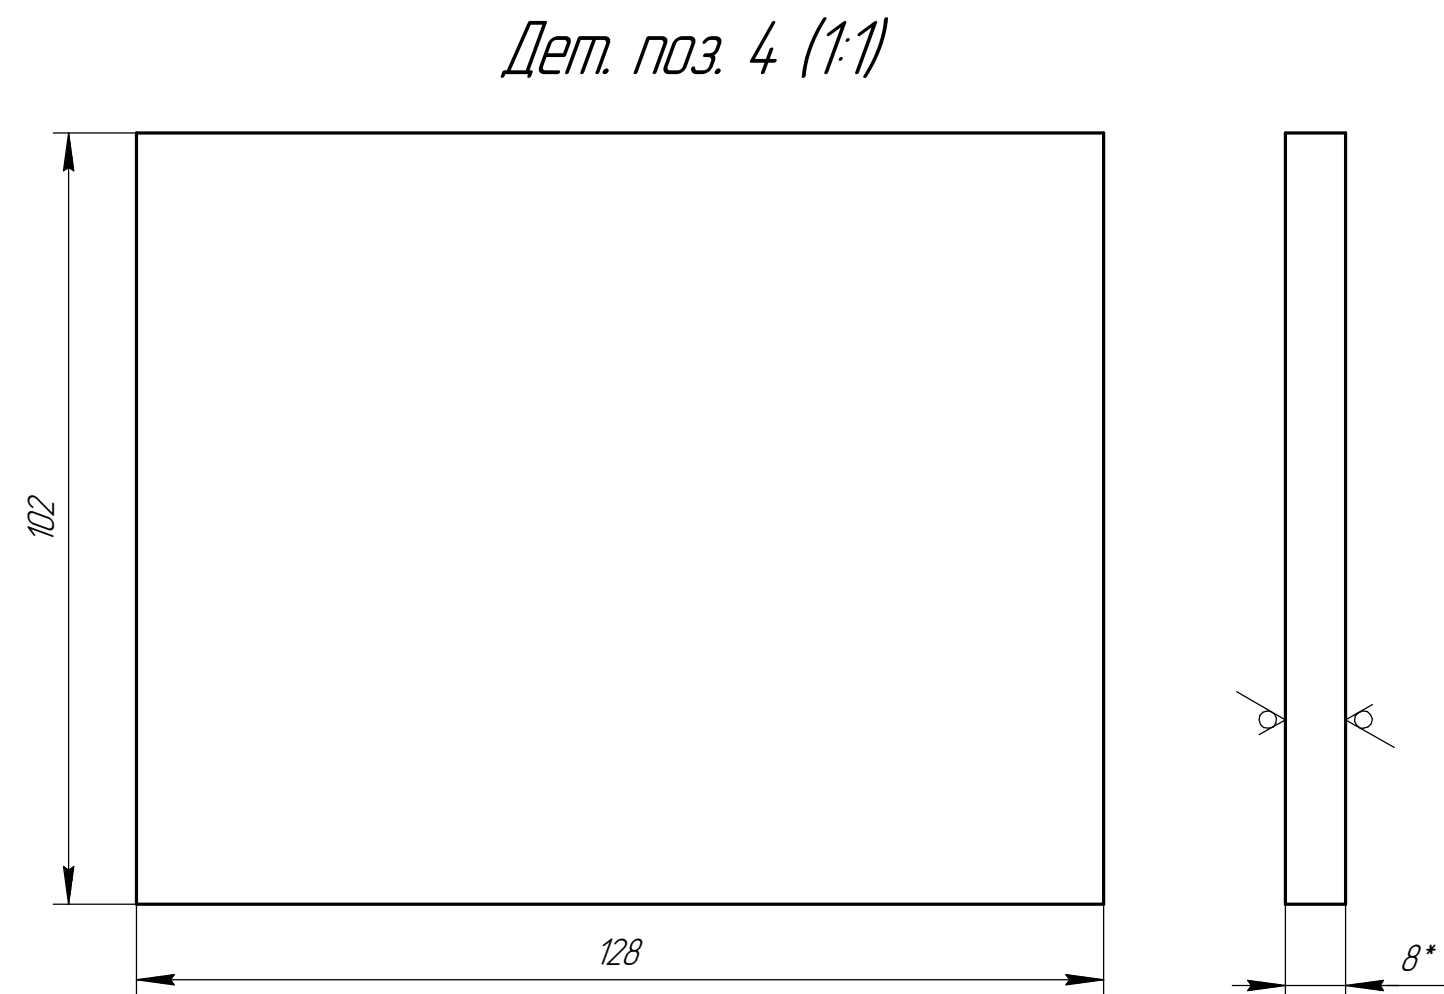


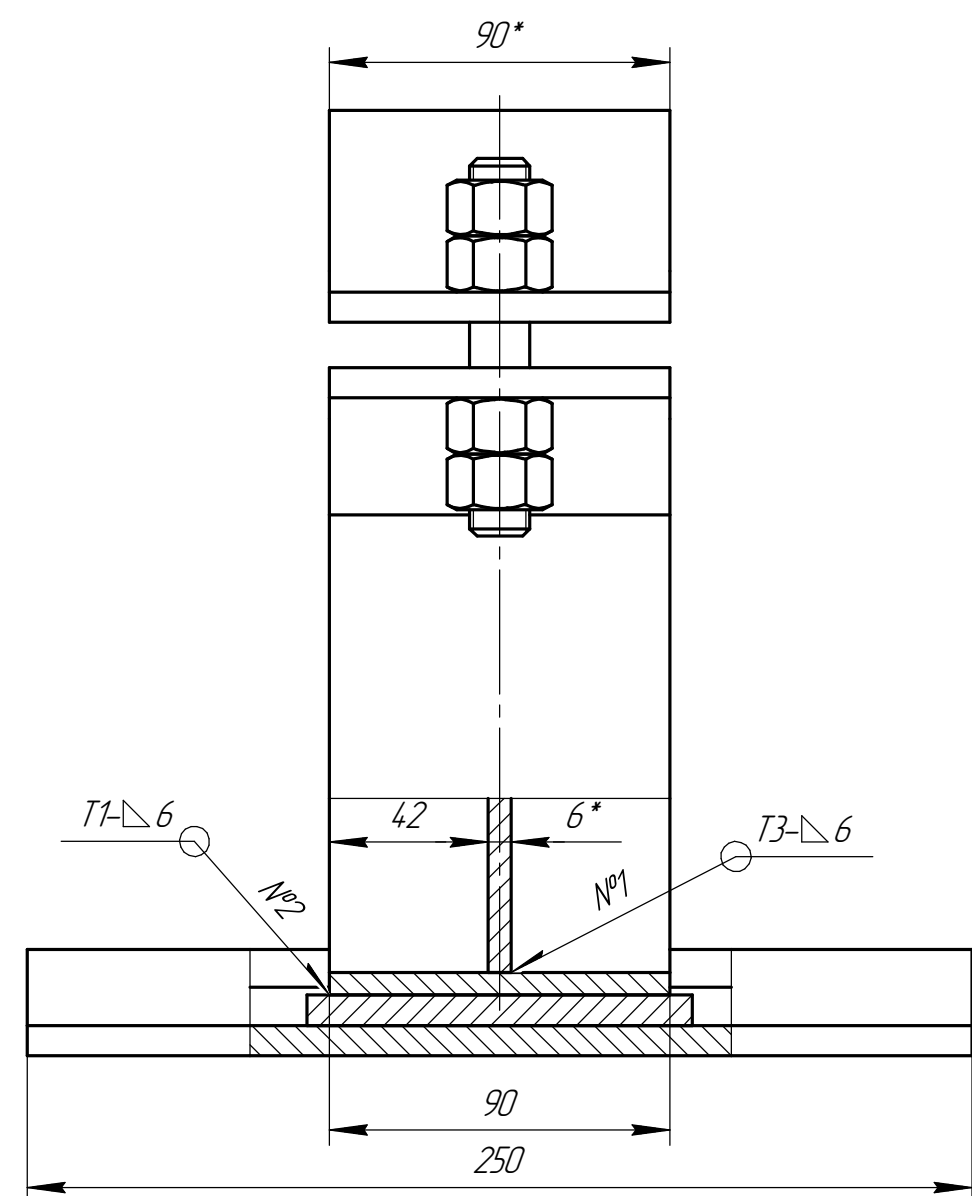

1. Общие допуски по ГОСТ 30893.1 Н17, h17, ±IT17/2.
2. *Размеры для справок.
3. Материалы:
 - Лист ГОСТ 19903-2015, 09Г2С ГОСТ 19281-2014;
 - Паронит ПОН ГОСТ 481-80;
 - Сварочная проволока Св-08Г2С ГОСТ 2246-70.
4. Сварка по ГОСТ 14771-76.
5. Основные технические требования по СТО 79814898 131-2009.
6. Площадь покрытия 0,45 м².

Поз	Обозначение	Наименование	Кол	Прим
1	334х90х6	Карпус	1	1,42 кг
2	122х87х6	Ребра	1	0,45 кг
3	256х90х8	Полхамут	2	1,42 кг
4	128х102х8	Основание	1	0,72 кг
5	250х180х8	Плита направляющая	1	2,83 кг
6	250х22х20	Направляющая	2	0,63 кг
7		Шпилька М16-6х100.88.40Х ГОСТ 22042-76	2	0,139 кг
8		Гайка М16-6Н.8.35 ГОСТ 5915-70	8	0,038 кг

Онора 113 СТО 79814898 131-2009

					Опора хомутовая направляющая	Лист	Масса	Масштаб
Изм/Лист	№ докум	Подп	Дата				10, 18	1:2
Разработ								
Проект								
Т.контр.						Лист	Листов	1
Н.контр.								
Утв								