



Спроект. №


Инд. № подл.

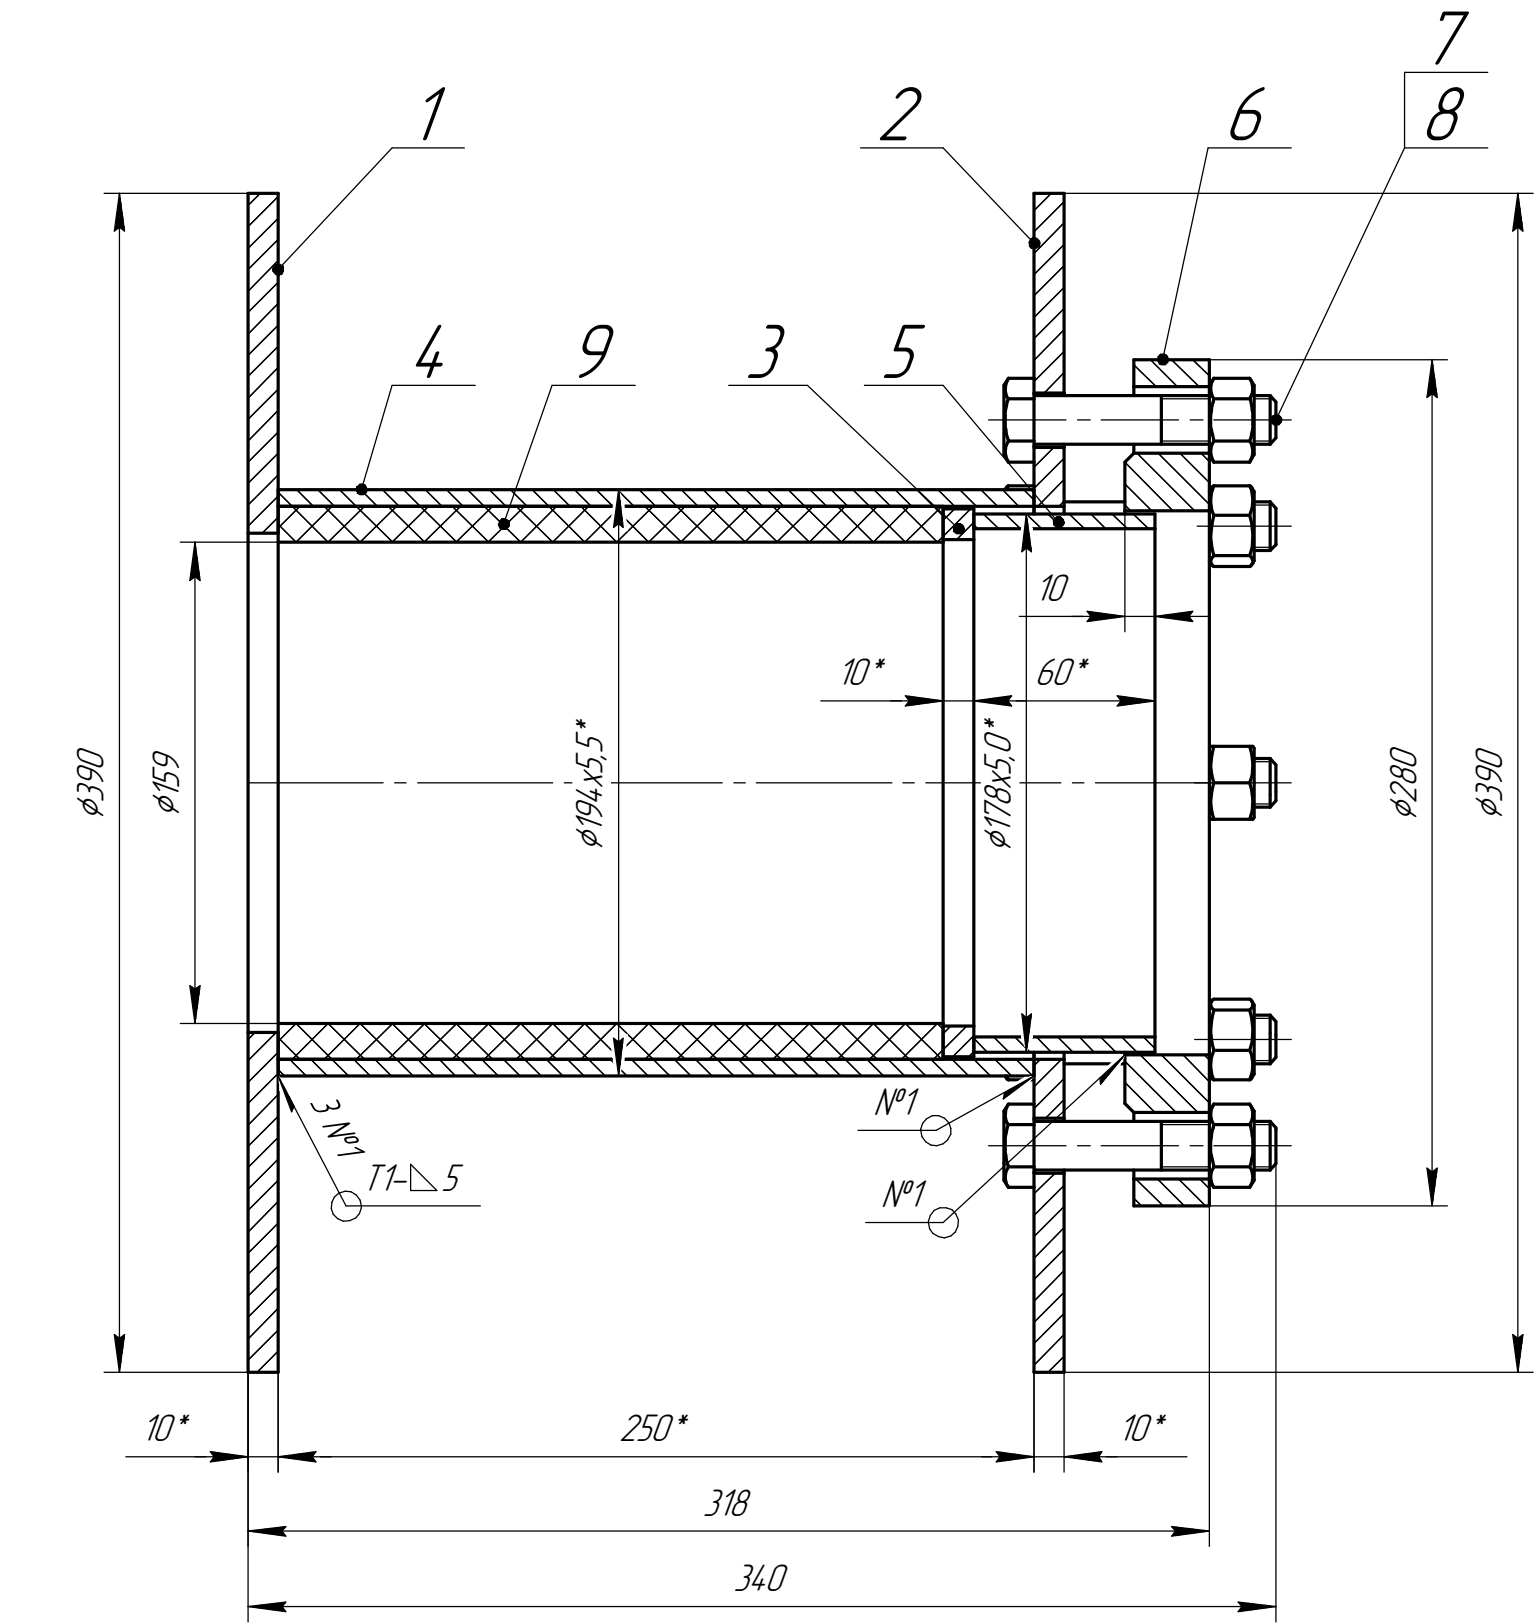


Дет. поз. 4

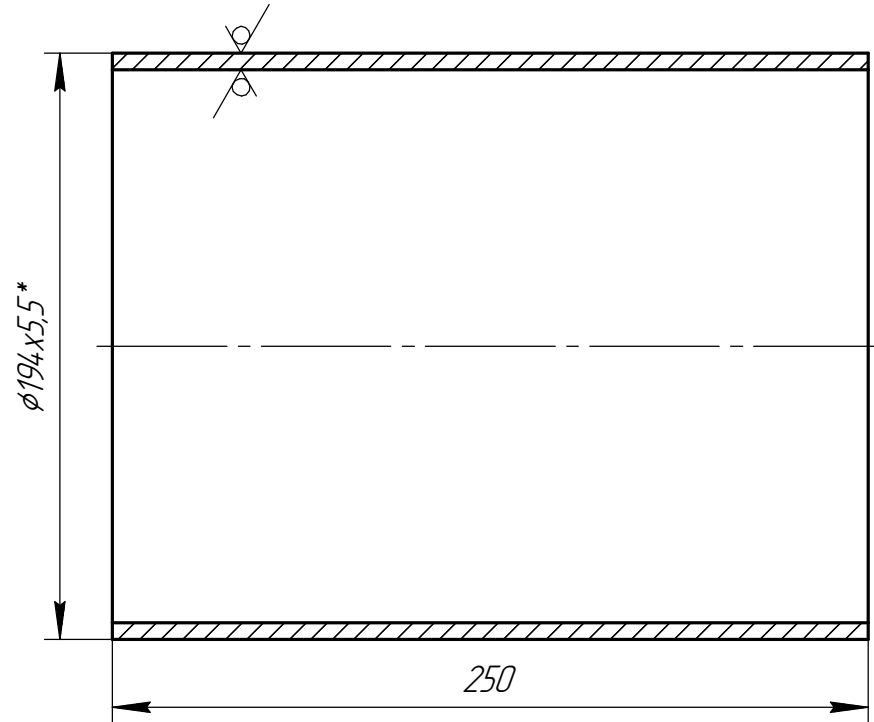

Дет. поз. 5

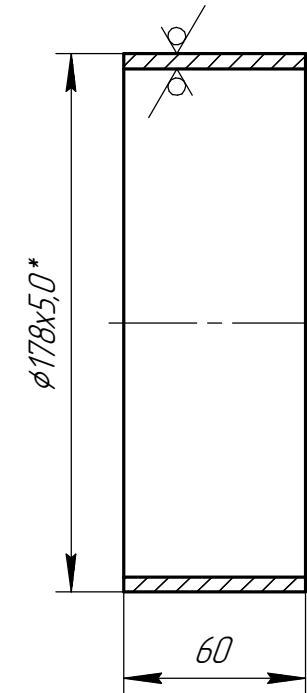


Дет. поз. 6

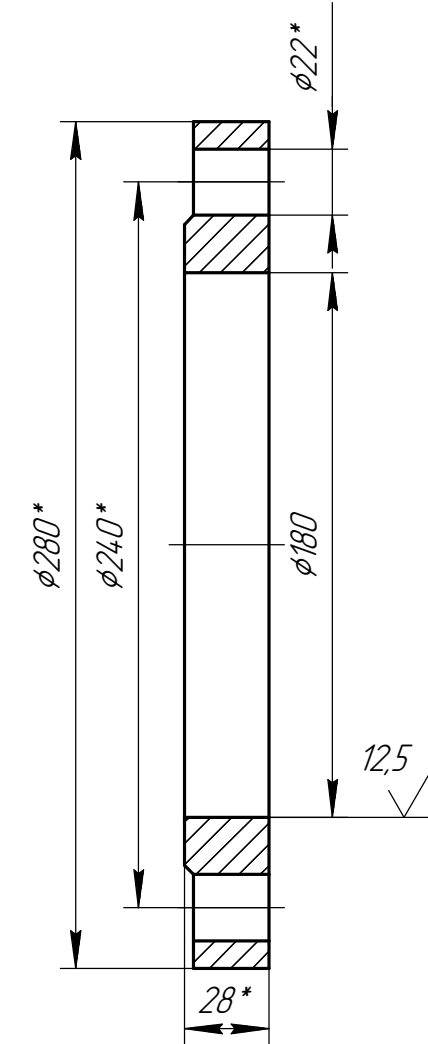


- Общие допуски по ГОСТ 30893.1: H17, h17, ±IT17/2.
- *Размеры для справок.
- Материалы:
 - Лист ГОСТ 19903-2015, Ст3 ГОСТ 14637-89;
 - Труба ГОСТ 10704-91, Ст3 ГОСТ 10705-80;
 - Сварочная проволока Св-08Г2С ГОСТ 2246-70.
- Сварка по ГОСТ 14771-76.
- Дет. поз. 10 условно не показана. На монтаже определить размеры и приварить.


Дет. поз. 1 (1:5)

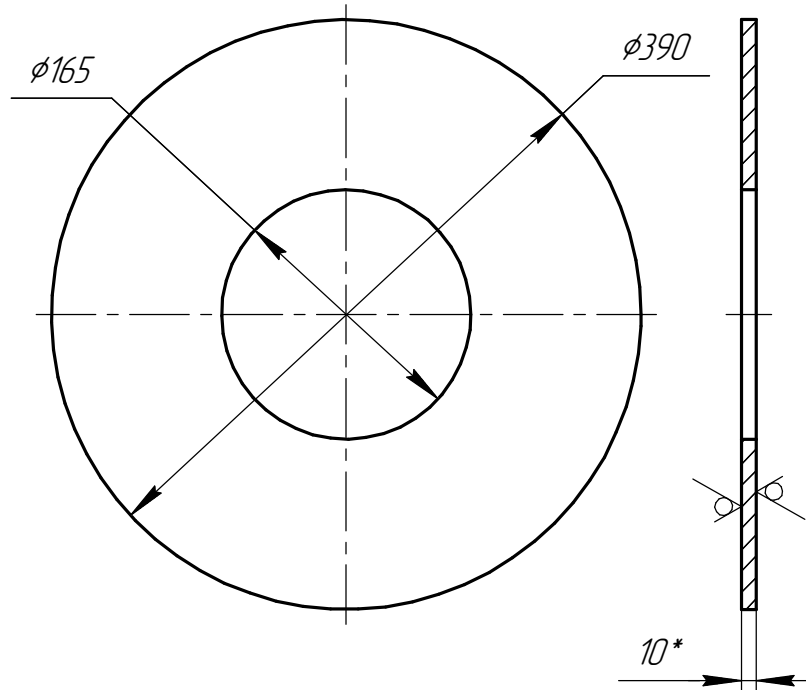

Дет. поз. 2 (1:5)

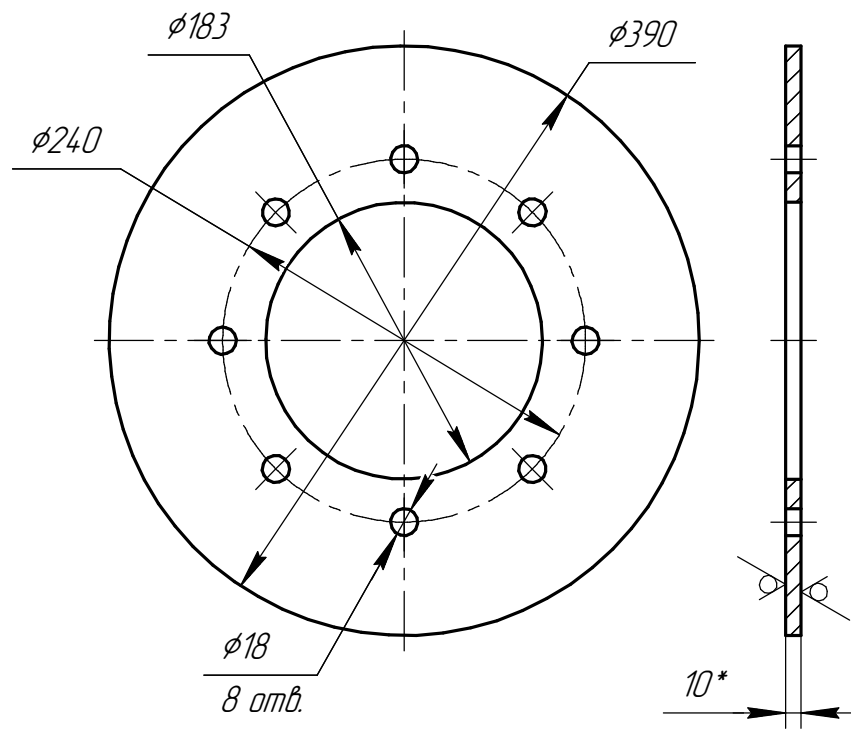

Дет. поз. 3

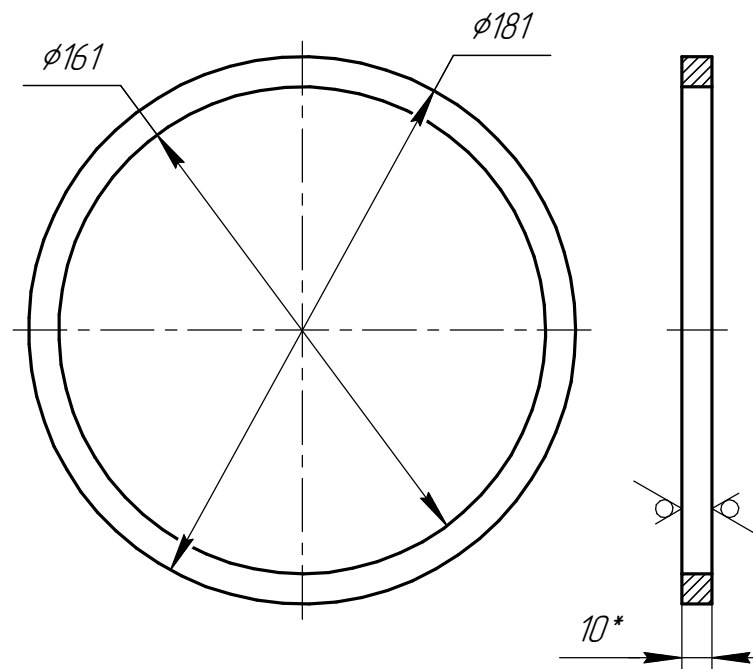

Поз.	Обозначение	Наименование	Кол.	Прим.
1	$\phi 390 \times 10$	Кольцо	1	7,7 кг
2	$\phi 390 \times 10$	Кольцо	1	7,15 кг
3	$\phi 181 \times 10$	Кольцо	1	0,42 кг
4	$\phi 194 \times 5,5$ L=250	Труба	1	6,4 кг
5	$\phi 178 \times 5,0$ L=60	Труба	1	1,28 кг
6		Фланец 1-150В-16 Ст3сп ГОСТ 12820-80	1	7,36 кг
7		Болт М16-6дх80.58.019 ГОСТ 7798-70	8	0,161 кг
8		Гайка М16-6Н.5.019 ГОСТ 5915-70	8	0,038 кг
		Прочие материалы		
9		Набивка сальниковая прографиченная $\phi 12$ мм ГОСТ 5152-84	19	м.п.
10		Арматура $\phi 8$	2,9м.	1,15 кг

Изм.	Лист	№ докум.	Подп.	Дата	24-001-БСК-032/01-24-1-ТС		
Разраб.					Лит.	Масса	Масштаб
Пров.						33,53	1:2,5
Т.контр.					Лист	Листов	1
Н.контр.							
Утв.							

Сальник газонепроницаемый Ду150

Копировал Формат А2