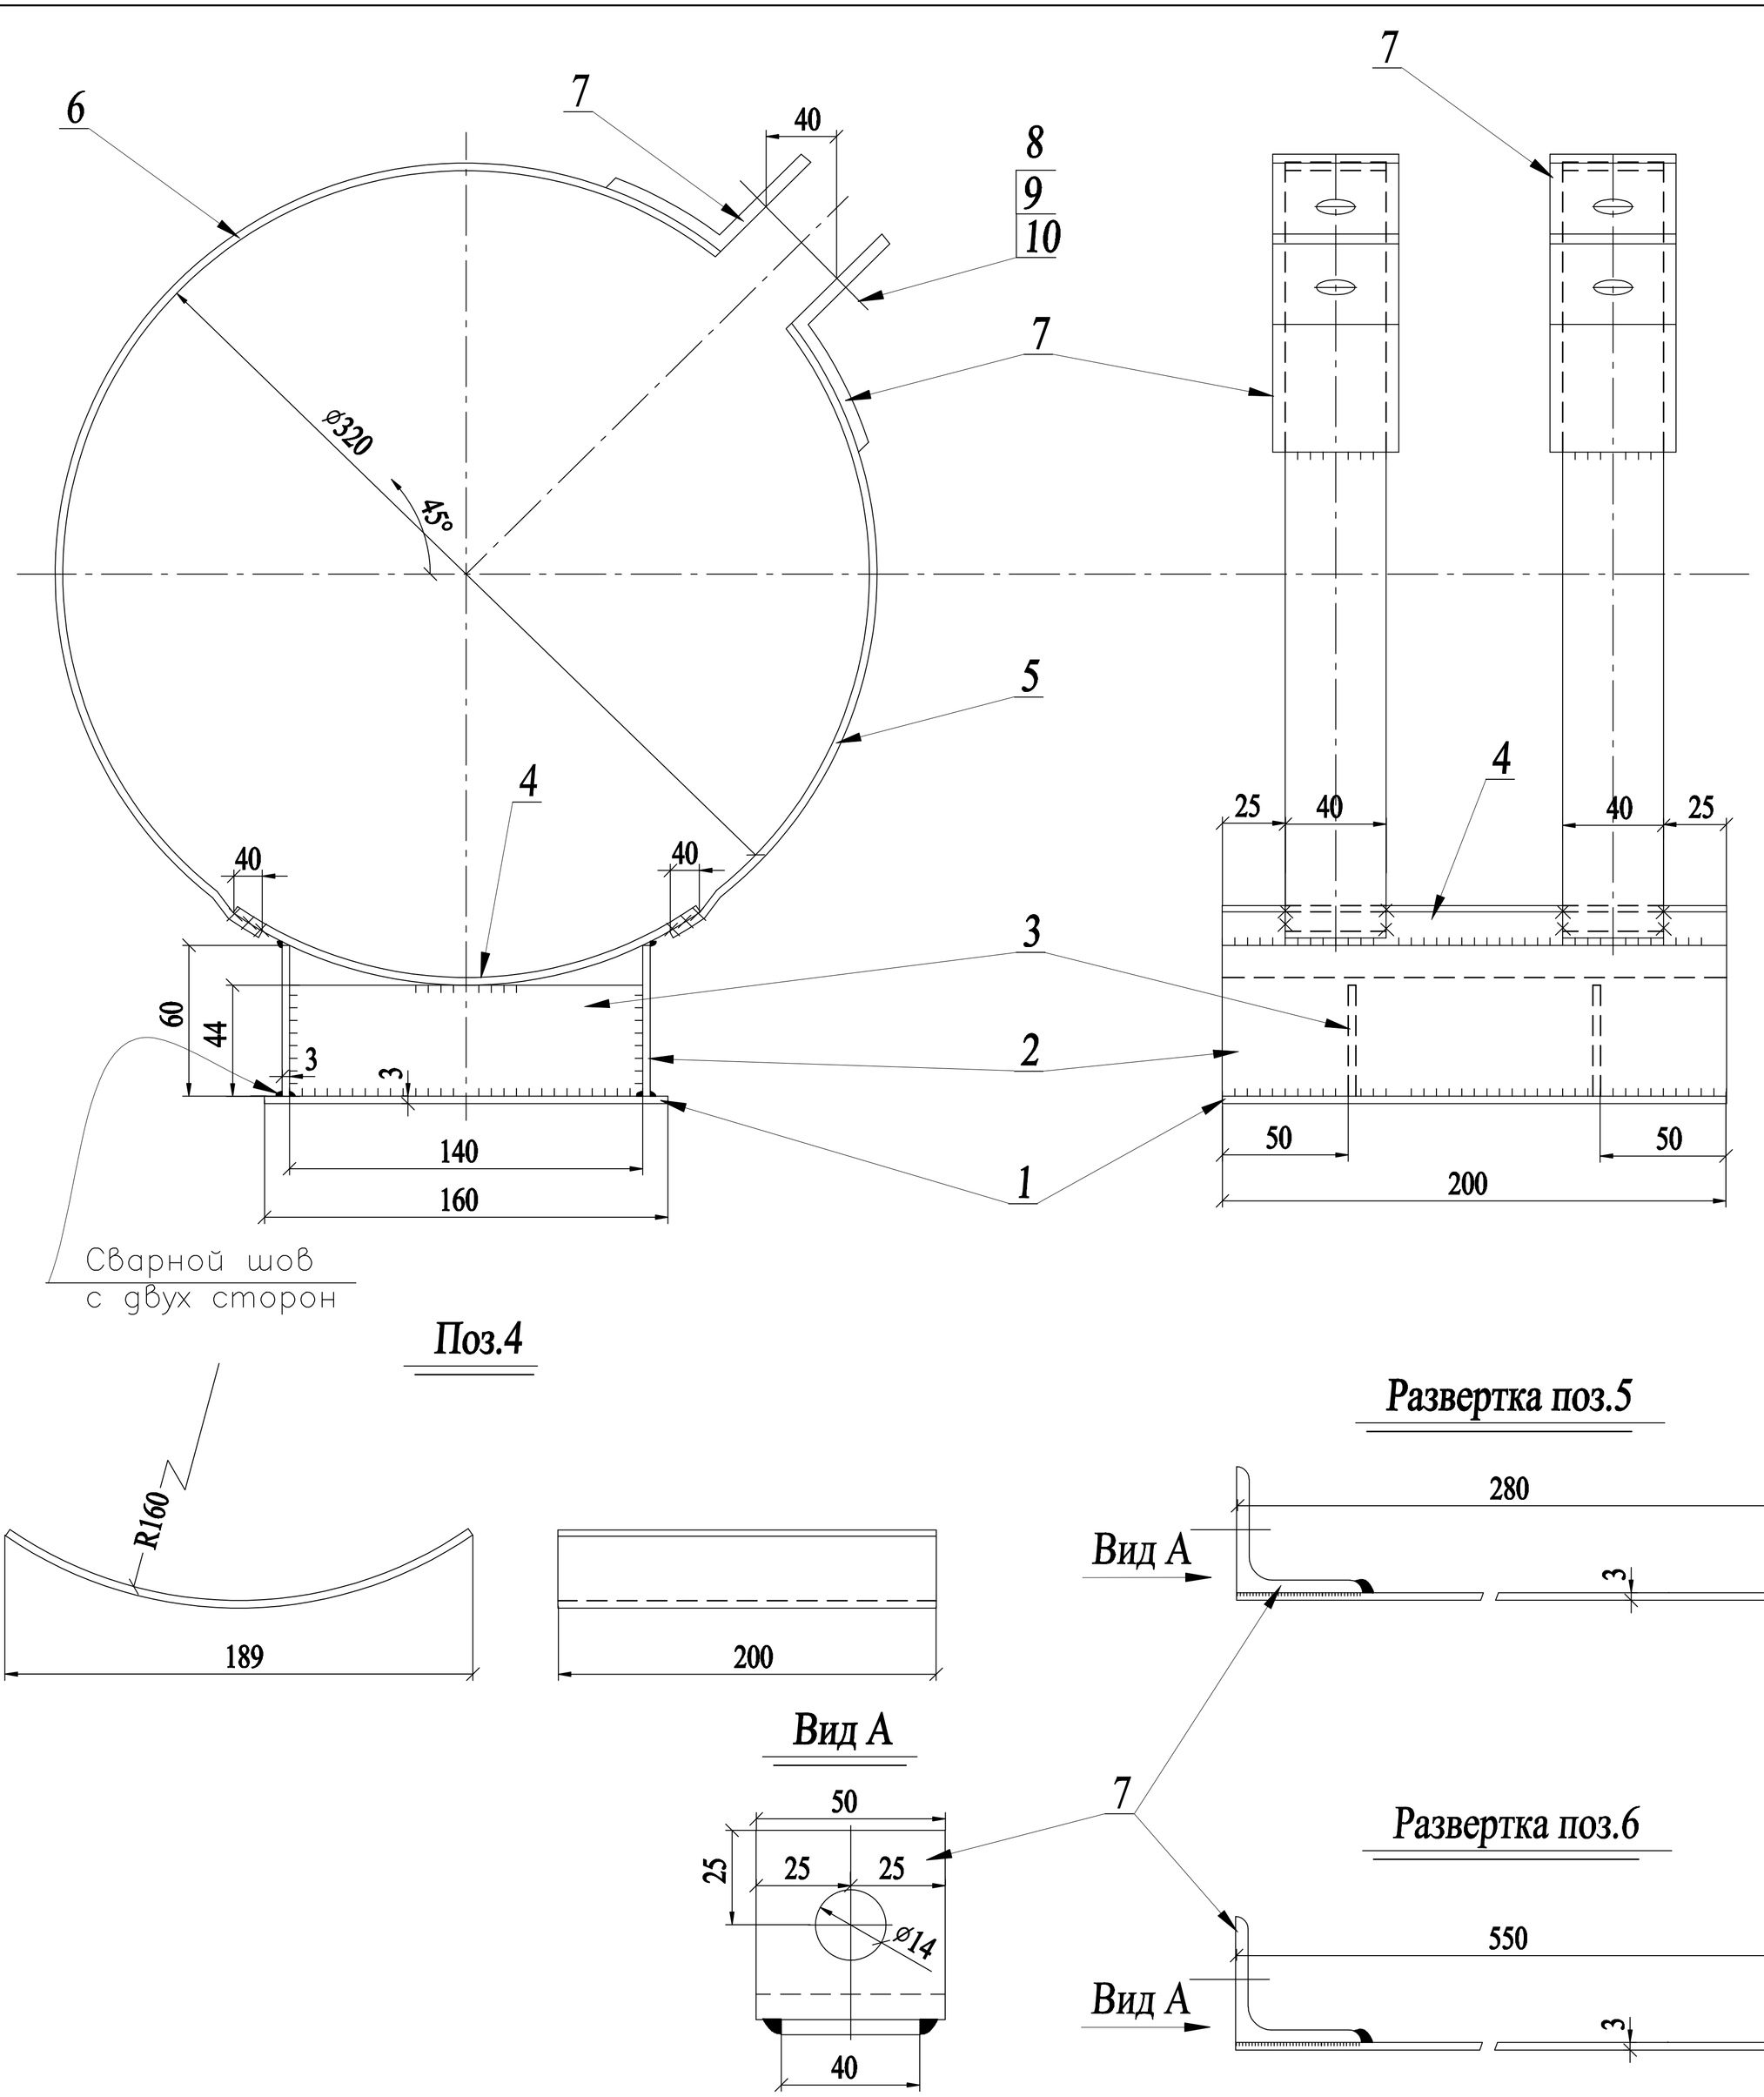

Поз.4

Развертка поз.5

Вид А

7

Развертка поз.6

Поз.3

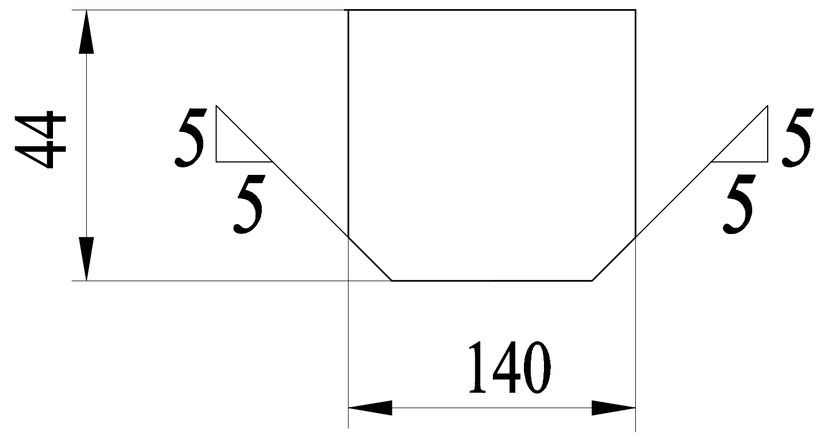

Примечания:

1. Сварные швы - 3 мм
2. Сварка полуавтоматическая по ГОСТ 14771-76 в среде CO2. Сварочная проволока Св-08Г2С по ГОСТ2246-70 диаметром 1,4-2,0 мм.
3. На заводе окрасить грунтом ГФ-021 по ГОСТ 25129-82 в два слоя.
4. Не указанные предельные отклонения размеров по H 14. h 14. ± IT 14/2
5. Опору маркировать: 219/315.100

Выборка металла

Материал		Сечение	Масса в кг	ГОСТ
ГОСТ 19281-88	09Г2С	лист 3	4,1	
		Угол 50х5	0,75	
		Шайба 12	0,02	
		Гайка М12	0,03	
		болт М12х80	0,18	
Итого			5,08	кг

				на сварные швы			0,1	5,18		
	10	4		Шайба 12 ГОСТ 11371-78		0,006	0,02			
	9	2		Гайка М12-7Н.6ГОСТ5915-70*		0,015	0,03			
	8	2		болт М 12	80	0,088	0,18			
	7	4		Угол 50х5	50	0,19	0,75			
	6	2		- 40 х 3	550	0,52	1,04			
	5	2		- 40 х 3	280	0,26	0,52			
	4	1		- 200 х 3	200	0,94	0,94			
	3	2		- 44 х 3	140	0,145	0,29			ср.угл.
	2	2		- 60 х 3	200	0,28	0,56			
	1	1		- 160 х 3	200	0,75	0,75			
ОТПР. ЭЛЕМ.	ДЕТ.	Т. КОЛ-ВО	Н.	СЕЧЕНИЕ	ДЛИНА	ШТ. МАССА В КГ	ОБЩ.	ЭЛЕМ.	МАРКА СТАЛИ	ПРИМЕЧАНИЯ

СПЕЦИФИКАЦИЯ СТАЛИ 09Г2С ГОСТ 19281-88

Исполнил		007.ТП.219.СПОк.51.12889.01
Проверил		
Рук.груп.		
Гл.конст.		Опора 219/315.100
Гл.техн.		Серия 1-487-1997.00.000
Гл.инж.	Немиров	

Стадия	Лист	Листов
Р	1	1

ООО НПП "Строительные технологии"