



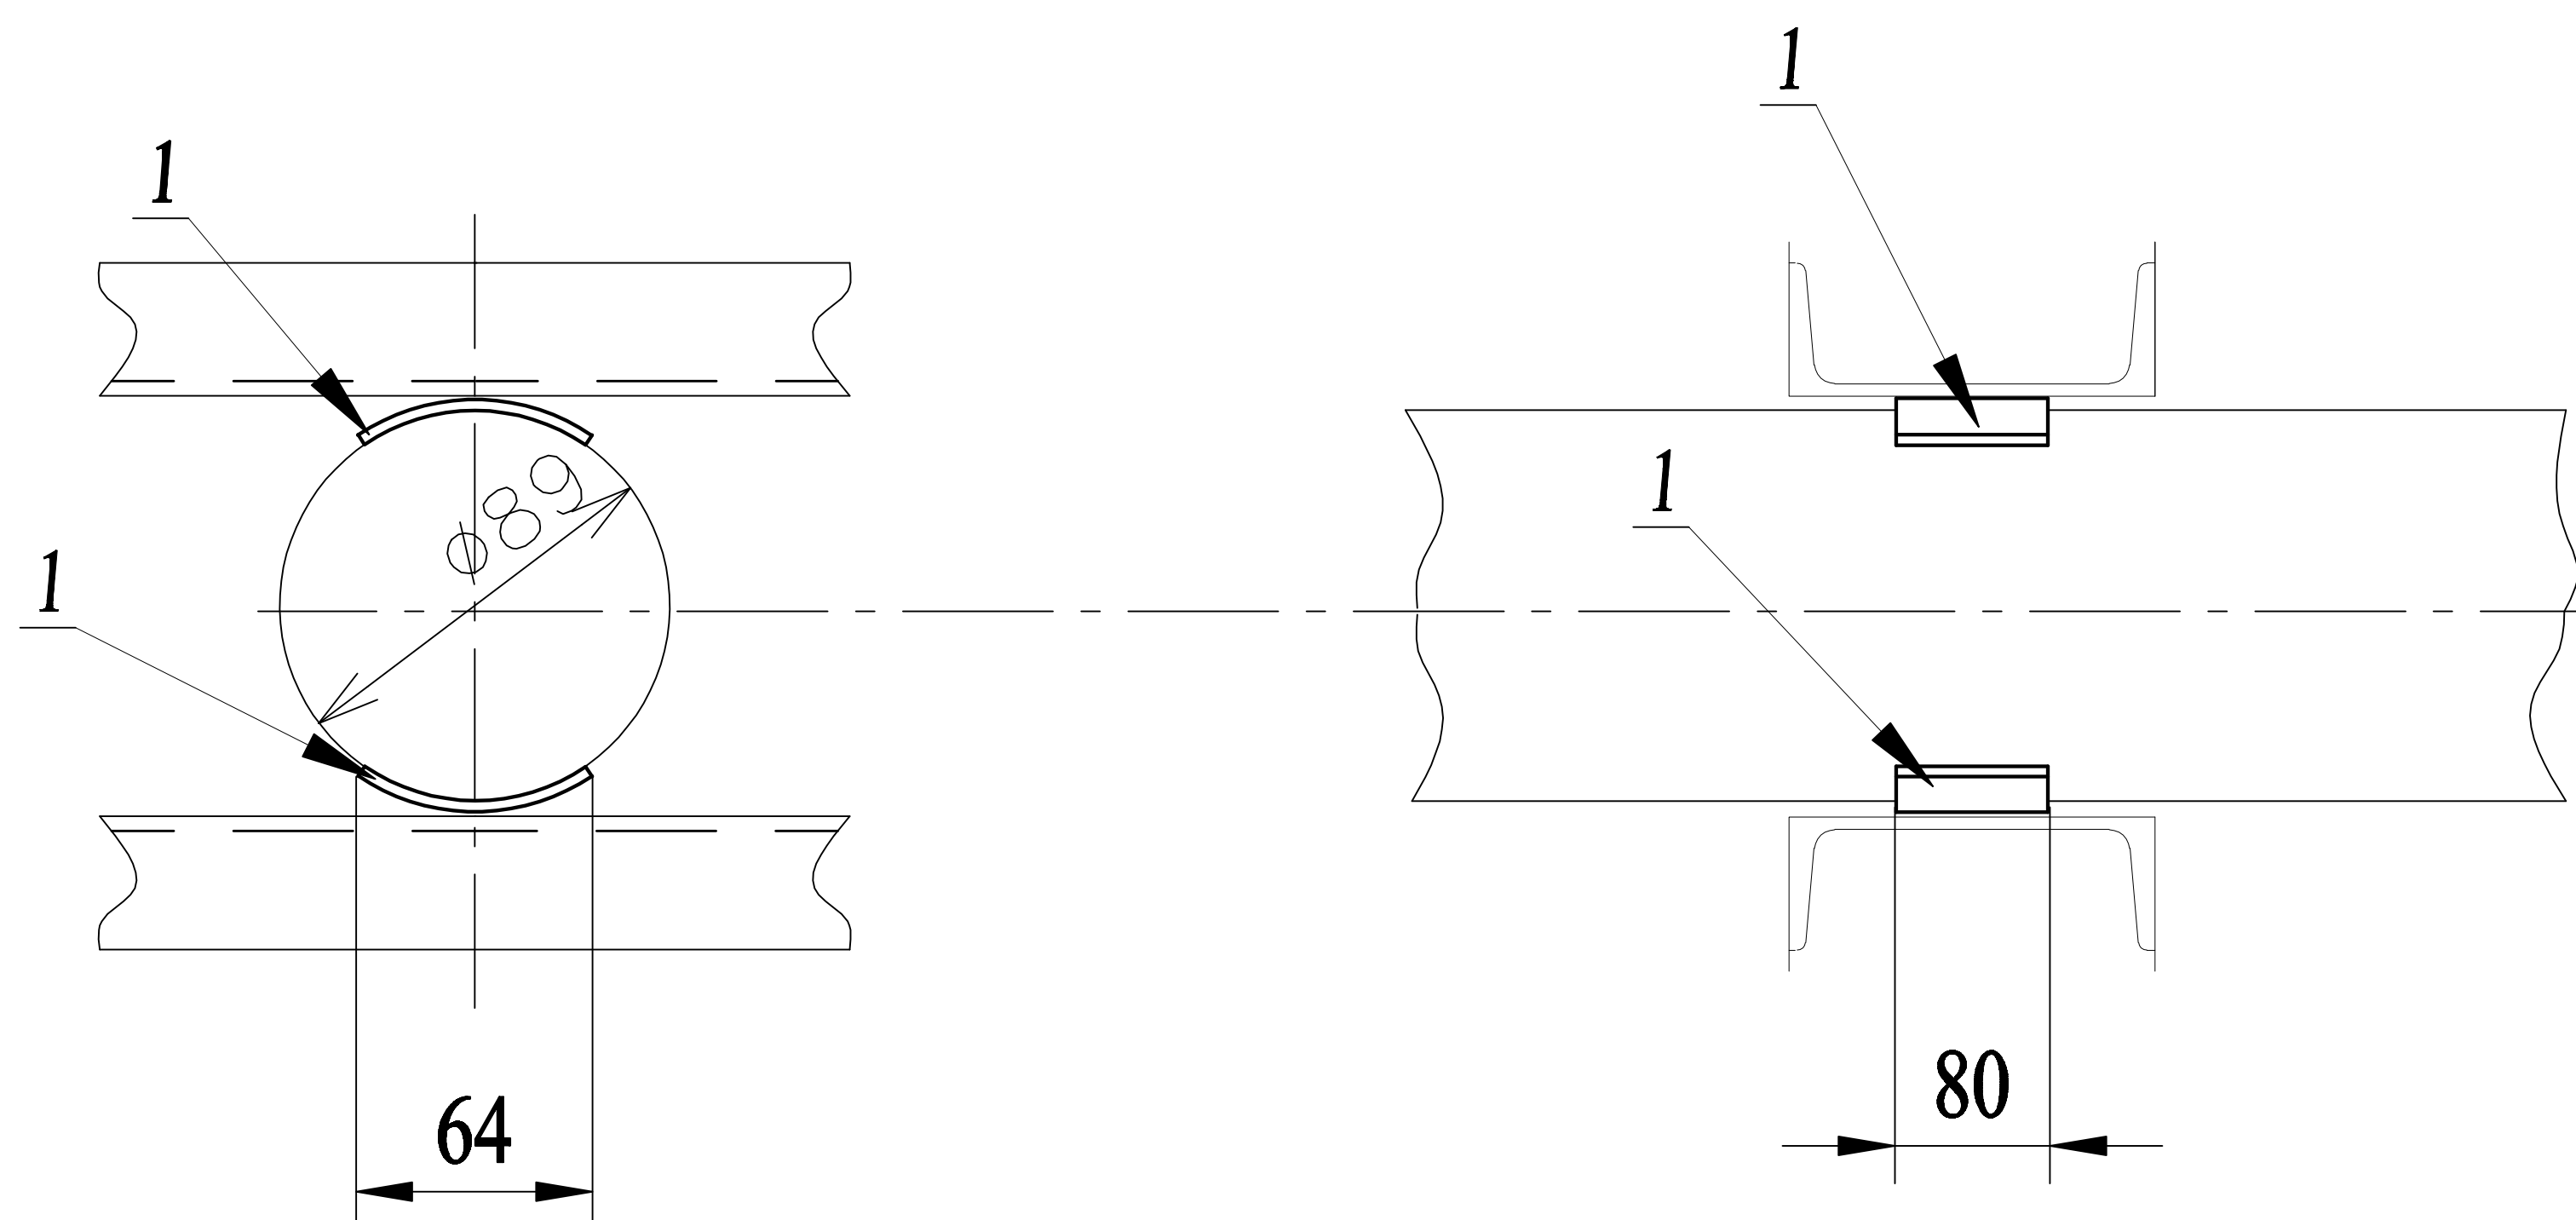

Поз.1

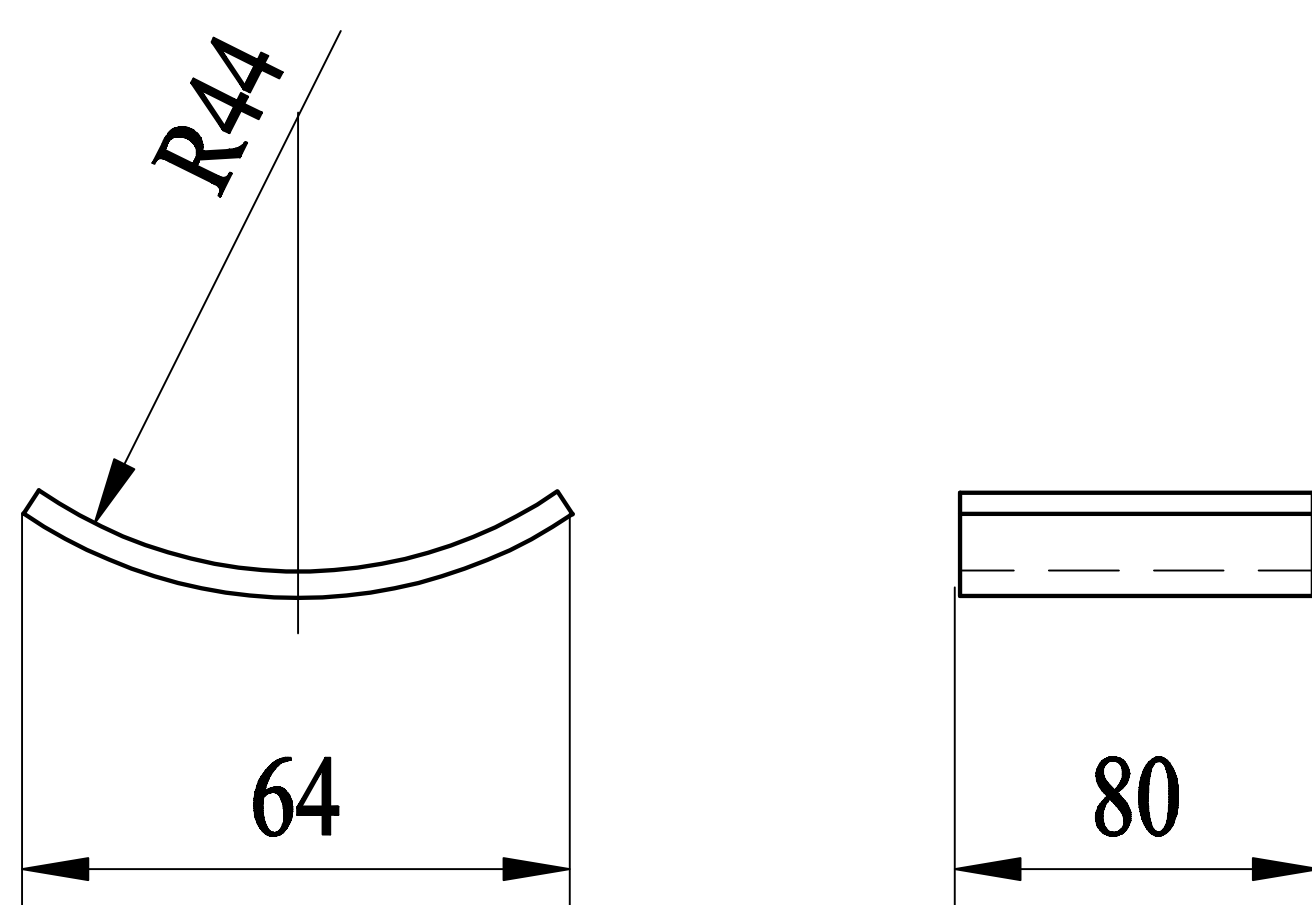

Выборка металла			
Материал		Сечение	Масса в кг
ГОСТ 19281-88	09Г2С	лист 6	0,5
Итого		0,5	кг

1. На заводе окрасить грунтом ГФ-021 по ГОСТ 25129-82 в два слоя.
2. Не указанные предельные отклонения размеров по Н 14. h 4. $\pm IT\ 14/2$
3. Острые кромки притупить радиусом $R = 0,5\text{ мм.}$
4. Опору маркировать: 89-Т10.04

				на сварные швы				0,5		
										ф.л.
	1	2		- 65 х 6	80	0,25	0,5			ф.л.
ОТПР. ЭЛЕМ.	ДЕТ.	Т. КОЛ-ВО	Н.	СЕЧЕНИЕ	ДЛИНА	ШТ.	ОБЩ.	ЭЛЕМ.	МАРКА СТАЛИ	ПРИМЕЧАНИЯ

СПЕЦИФИКАЦИЯ СТАЛИ 09Г2С ГОСТ 19281-88

				007.ТП.89.Т10.000.1804.03				
Исполнил				Опора неподвижная 89-Т10.04	Стадия	Лист	Листов	
Проверил					Р	1	1	
Рук.груп.								
Гл.конст.				Серия 4.903-10 выпуск 4	ООО НПП "Строительные технологии"			
Гл.техн.								
Гл.инж.	Немиров							