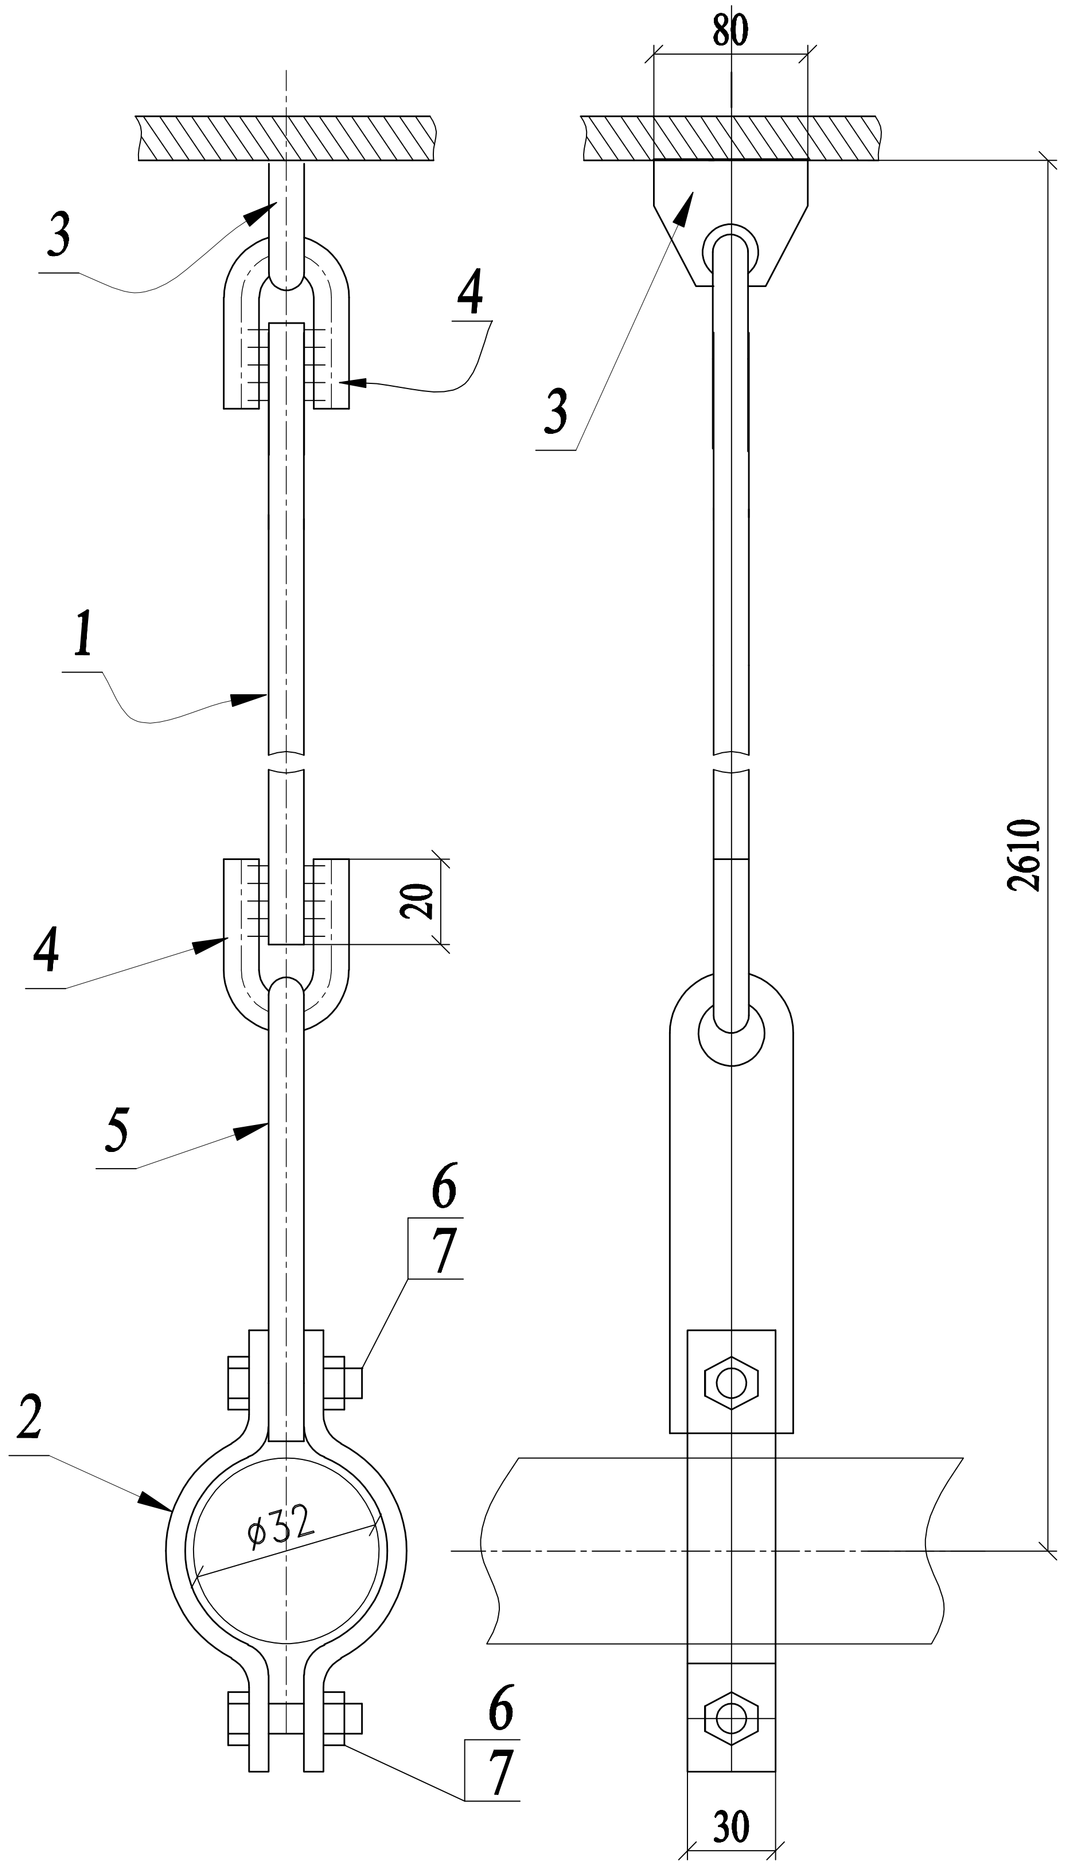

Поз.2

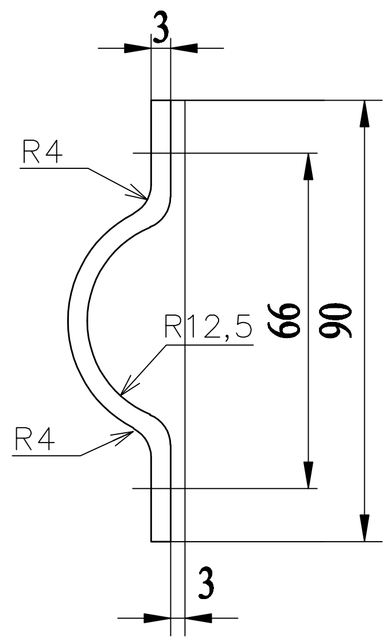

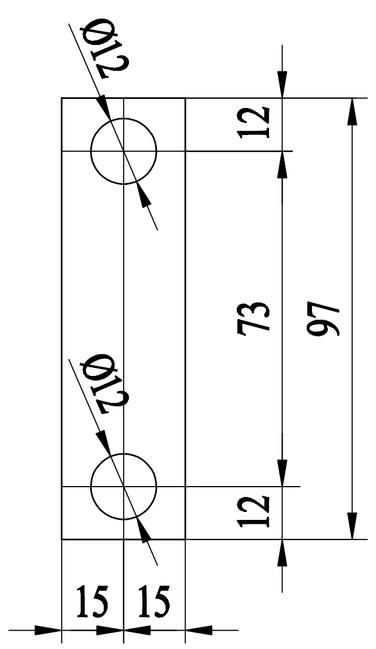

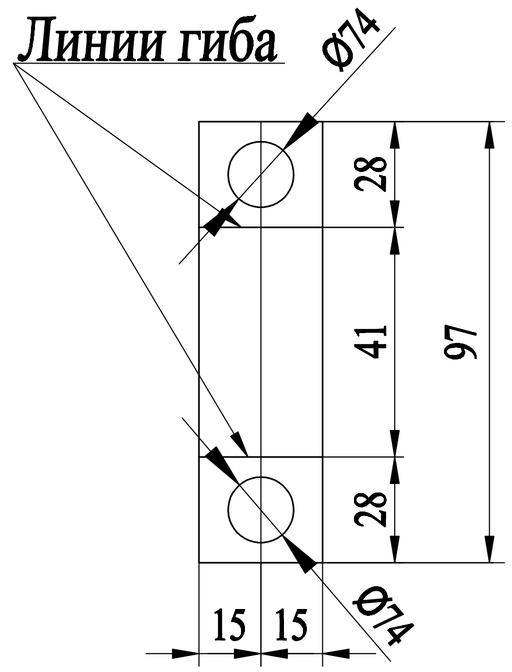

Поз.3

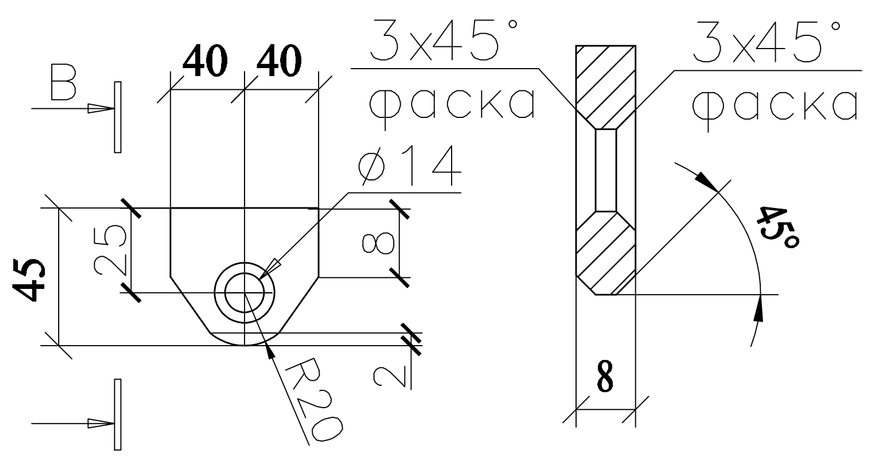

В–В

Примечания:

1. Сварные швы - 6 мм
2. Сварка полуавтоматическая по ГОСТ 14771-76 в среде СО2. Сварочная проволока Св-08Г2С по ГОСТ2246-70 диаметром 1,4-2,0 мм.
3. На заводе окрасить грунтом ГФ-021 по ГОСТ 25129-82 в два слоя. Степень очистки поверхности металлоконструкций от окислов перед окраской - 4 по ГОСТ 9.402-80.
4. Не указанные предельные отклонения размеров по H14, h14, ±IT 1/2
5. Подвеску маркировать Т-22.07 Дн 25

Поз.4

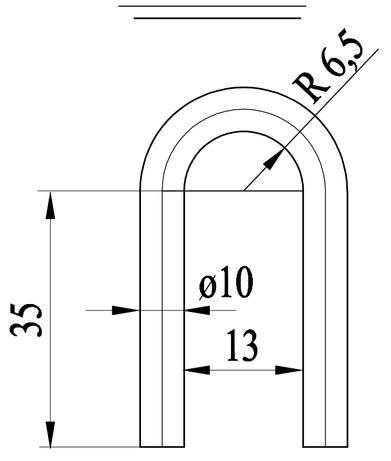

Поз.5

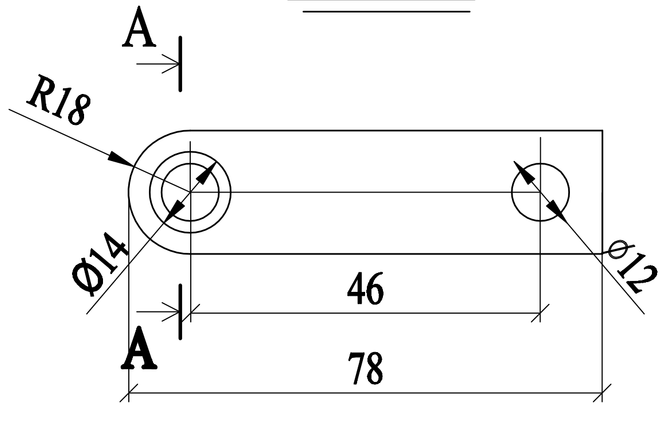

А-А

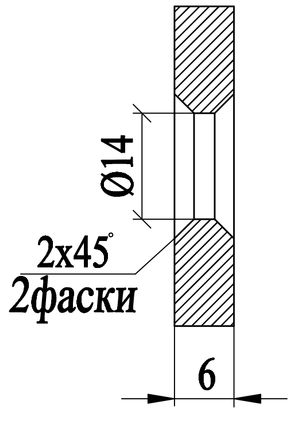

Поз.1

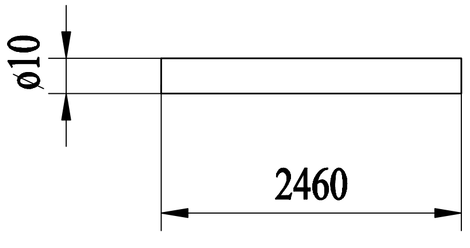

				на сварные швы			0,02	2,232		
	7	4		Гайка М10-7Н.6ГОСТ5915-70*	0,012	0,048				
	6	2		Болт М10х35	35	0,033	0,068			
	5	1		- 36 х 6	78	0,121	0,121			гнуть отв.
	4	2		Круг Ф 10	106	0,065	0,13			выр.по R
	3	1		- 8 х 45	80	0,2	0,2			гнуть
	2	2		- 3 х 30	97	0,065	0,13			нар.резьбу
	1	1		Круг Ф 10	2460	1,515	1,515			
ОТПР. ЭЛЕМ.	ДЕТ.	Т. КОЛ-ВО	Н.	СЕЧЕНИЕ	ДЛИНА	ШТ. МАССА В КГ	ОБЩ.	ЭЛЕМ.	МАРКА СТАЛИ	ПРИМЕЧАНИЯ

СПЕЦИФИКАЦИЯ СТАЛИ 09Г2С ГОСТ 19281-88

		007.ТП.25.Т22.2610.2640.01	
Исполнил		Опора подвесная Т-22.07	Стадия: Р; Лист: 1; Листов: 1
Проверил			
Рук.груп.			
Гл.конст.		Серия 4.903-10 вып. 6	ООО НПП "Строительные технологии"
Гл.техн.			
Гл.инж.	Немиров		