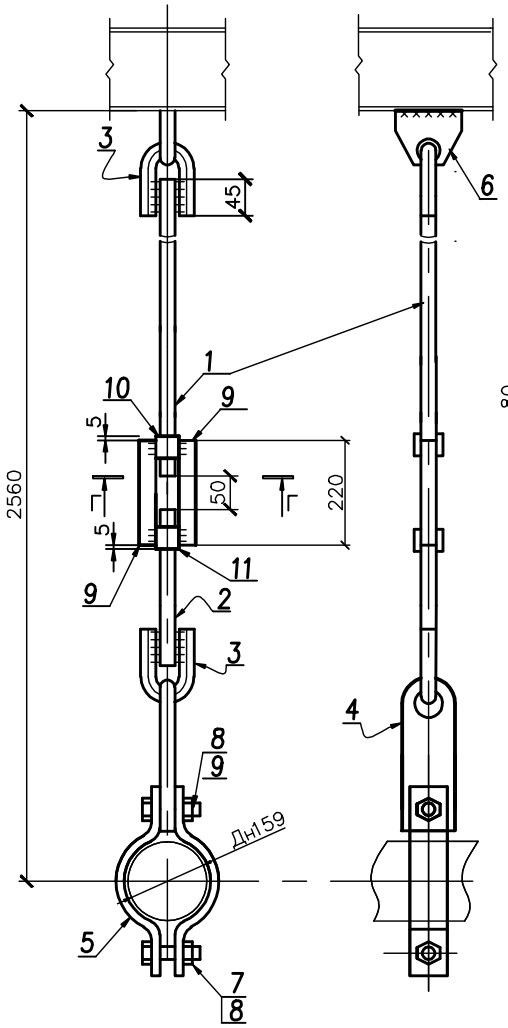

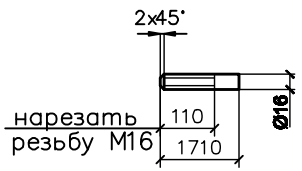

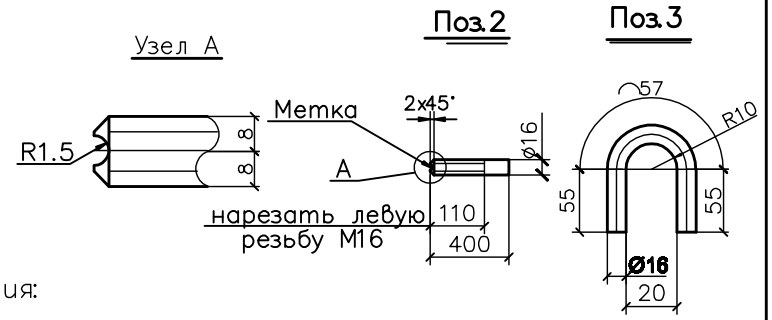

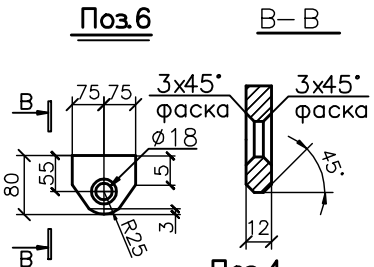

Примечания:

1. Сварные швы – 9 мм.
2. Заводская сварка полуавтоматическая по ГОСТ 14771–76 в среде CO2. Сварочная проволока Св–08Г2С по ГОСТ2246–70 диаметром 0,8–1,6 мм.
3. На заводе окрасить грунтом ГФ–021 по ГОСТ 25129–82 в 2 слоя.
4. Не указанные предельные отклонения размеров по H 14, h 14, ±IT 1/2
5. Опору маркировать Т23.27 Дн 159

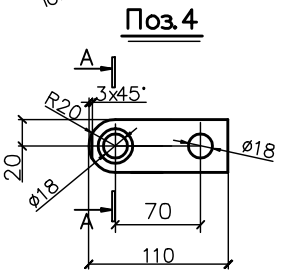

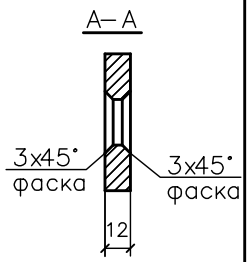

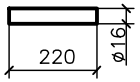

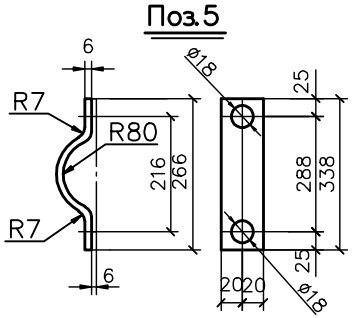

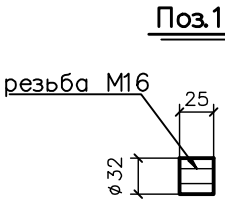

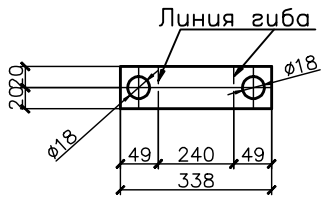

Отпр. элем.	№ дет.	Кол-во т.	Кол-во н.	Сечение	Длина	Масса в кг шт.	Масса в кг общ.	Масса в кг элем.	Марка стали	Примеч.
				на сварку			0,05	7,52		
	11	1		Ф 32	25	0,15	0,15			
	10	1		Ф 32	25	0,15	0,15			
	9	2		Ф 16	220	0,35	0,7			
	8	4		Гайка М 16		0,037	0,15			
	7	2		Болт М16	55	0,121	0,24			
	6	1		– 12 х 80	150	0,66	0,66			
	5	2		– 6 х 40	338	0,61	1,22			
	4	1		–12 х 40	110	0,35	0,35			
	3	2		Ф 16	167	0,26	0,52			
	2	1		Ф 16	400	0,63	0,63			
	1	1		Ф 16	1710	2,7	2,7			

СПЕЦИФИКАЦИЯ СТАЛИ 09Г2С ГОСТ 19281– 89

007.159.Т23.2560.2740.00

Изм	кол.	Исполнил	Подп.	Дата
Гл.конст				
Н.контр.				
Проверил				
Исполнил				

Опора подвесная Дн 159 тип Т23.27 исп I

Стадия	Лист	Листов
Р		

Серия 4.903–10 вып. 6

ООО НПП "Строительные технологии"

Формат