
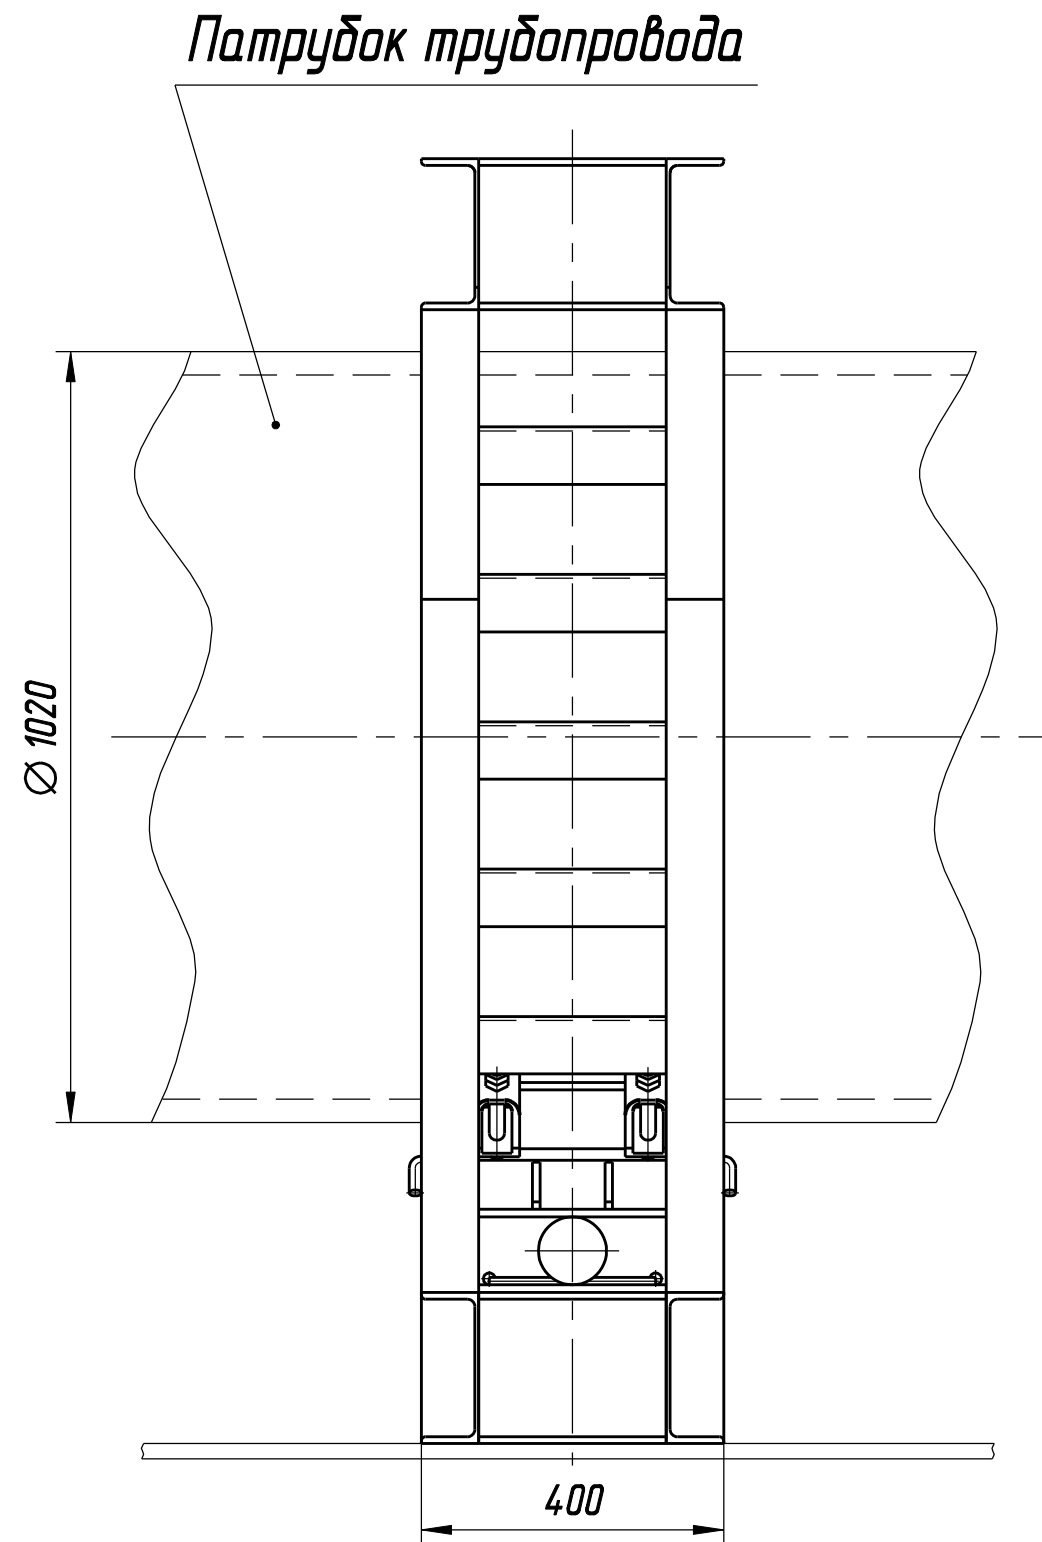


Инв. № подл.	Подп. и дата	Взам инв. №	Инв. № дубл.	Подпись и дата

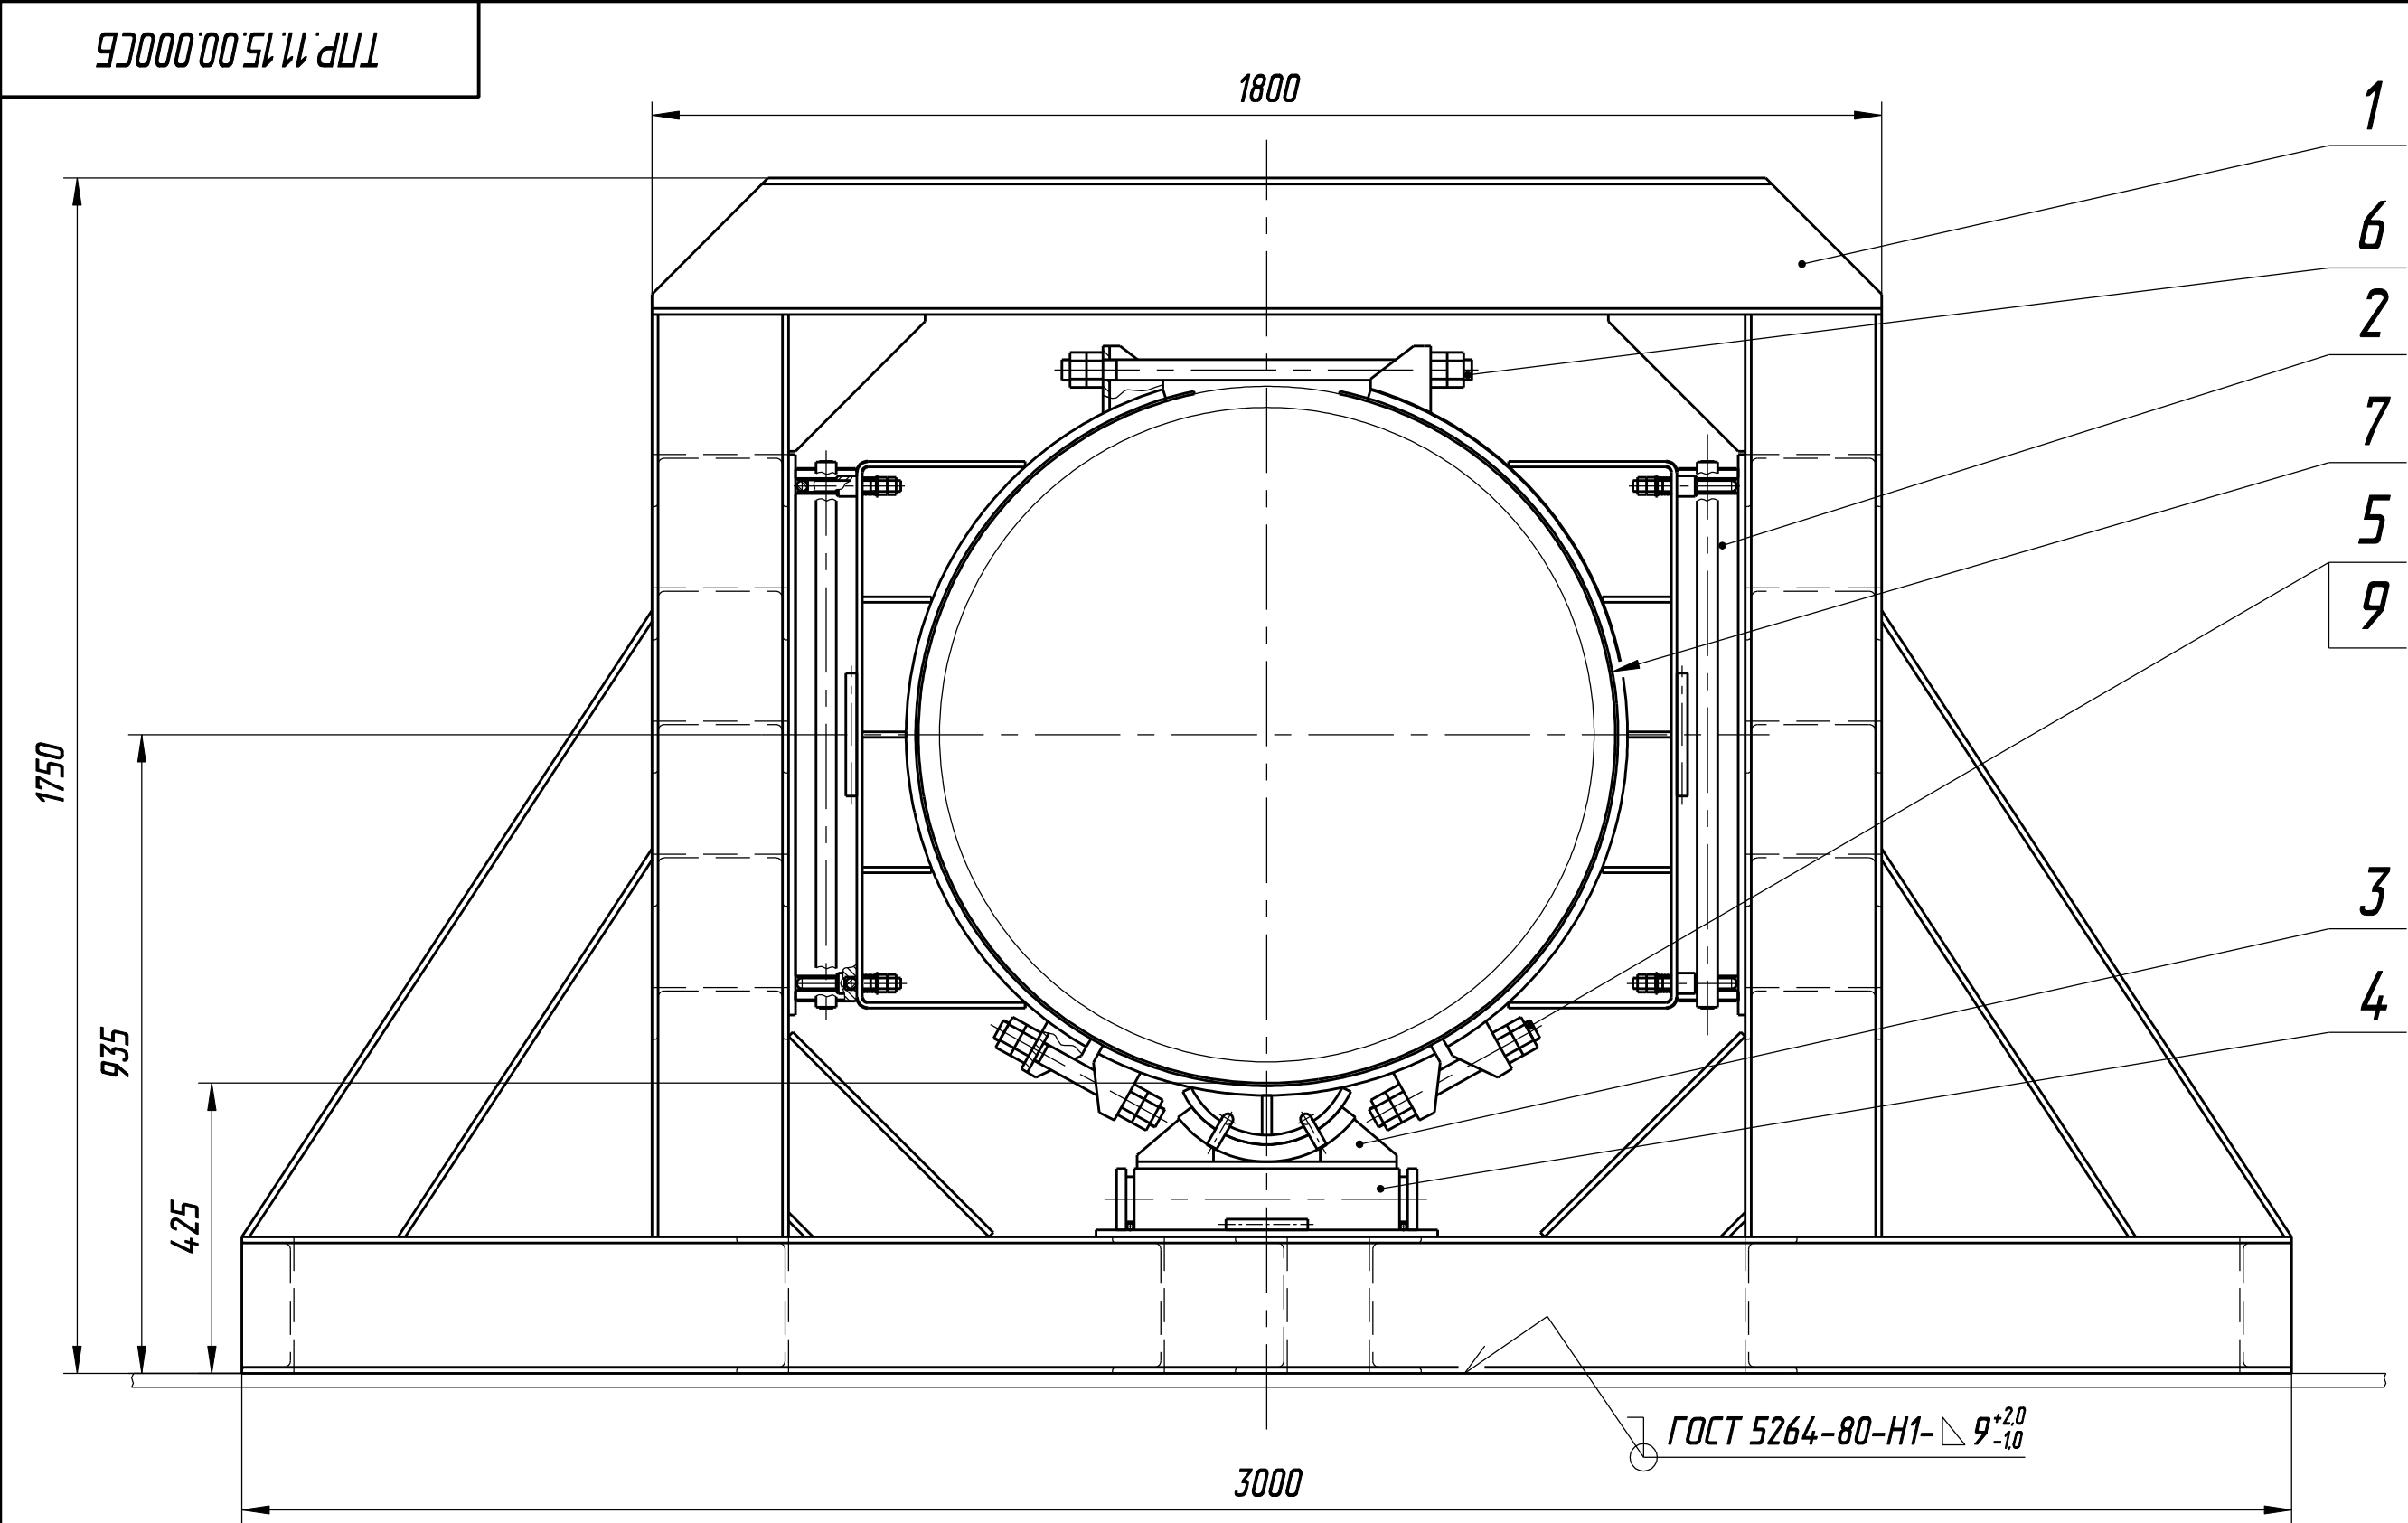

Техническая характеристика

1. Опора предназначена для крепления труб из углеродистой и низколегированной стали при строительстве технологических трубопроводов с наружным диаметром 1020 мм, транспортирующих вещества с температурой от минус 30 до 200 °С и условным давлением P_u до 12 МПа при температуре окружающей среды до минус 70 °С.

2. Допускаемые нагрузки на опору:
- вертикальная Q_v , не более 80 кН;
- боковая T , не более 270 кН.

Величина боковой допускаемой расчётной нагрузки задана при условии отсутствия внешних изгибающих моментов.

3. Перемещение вдоль оси трубы не более 100 мм.

Технические требования

1. Размеры для справок.

2. Сварку производить электродом типа Э50А ГОСТ 9467-75.

3. Покрытие: грунтовка АК-070 ГОСТ 25718-83 в один слой; эмаль ХВ-16 ТУ 6-10-1301-83 в два слоя. Допускаются другие виды антикоррозионного покрытия согласно проекту.

4. Маркировать любым способом, обеспечивающим сохранность маркировки на весь срок эксплуатации, шрифтом не менее 5:
обозначение по чертежу и товарный знак завода-изготовителя.

					ТПР.11.15.00.000СБ			
					Опора катковая направляющая Дн 1020 мм, Ру 12 МПа Сборочный чертеж	Лит.	Масса	Масштаб
Изм.	Лист	№ докум.	Подп.	Дата			1020	1 : 10
Разраб.	Воранков			07.11				
Пров.								
Т. контр.						Лист	Листов 1	
Н. контр.	Воранков			07.11		ОАО "ТИПРОТЮМЕННЕФТЕГАЗ"		
Утв.	Бояркин			07.11				