

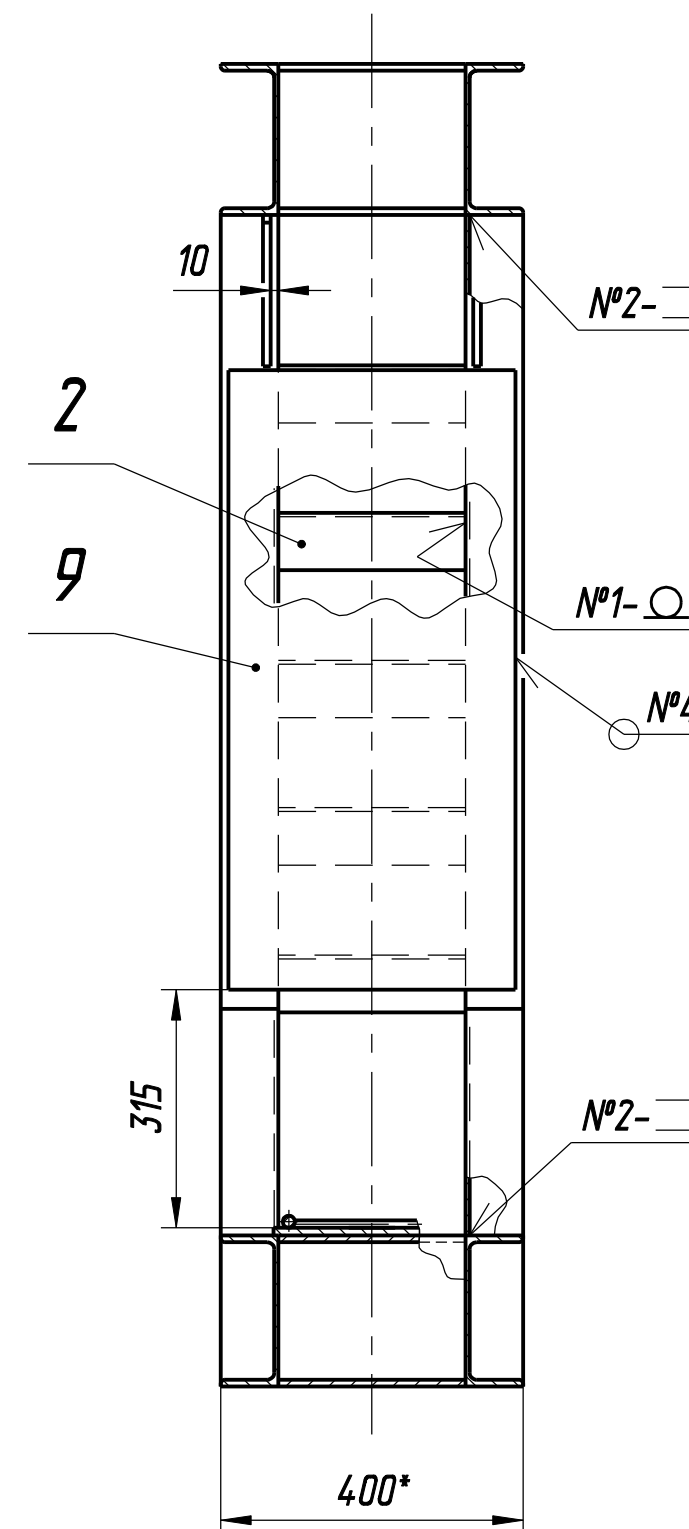


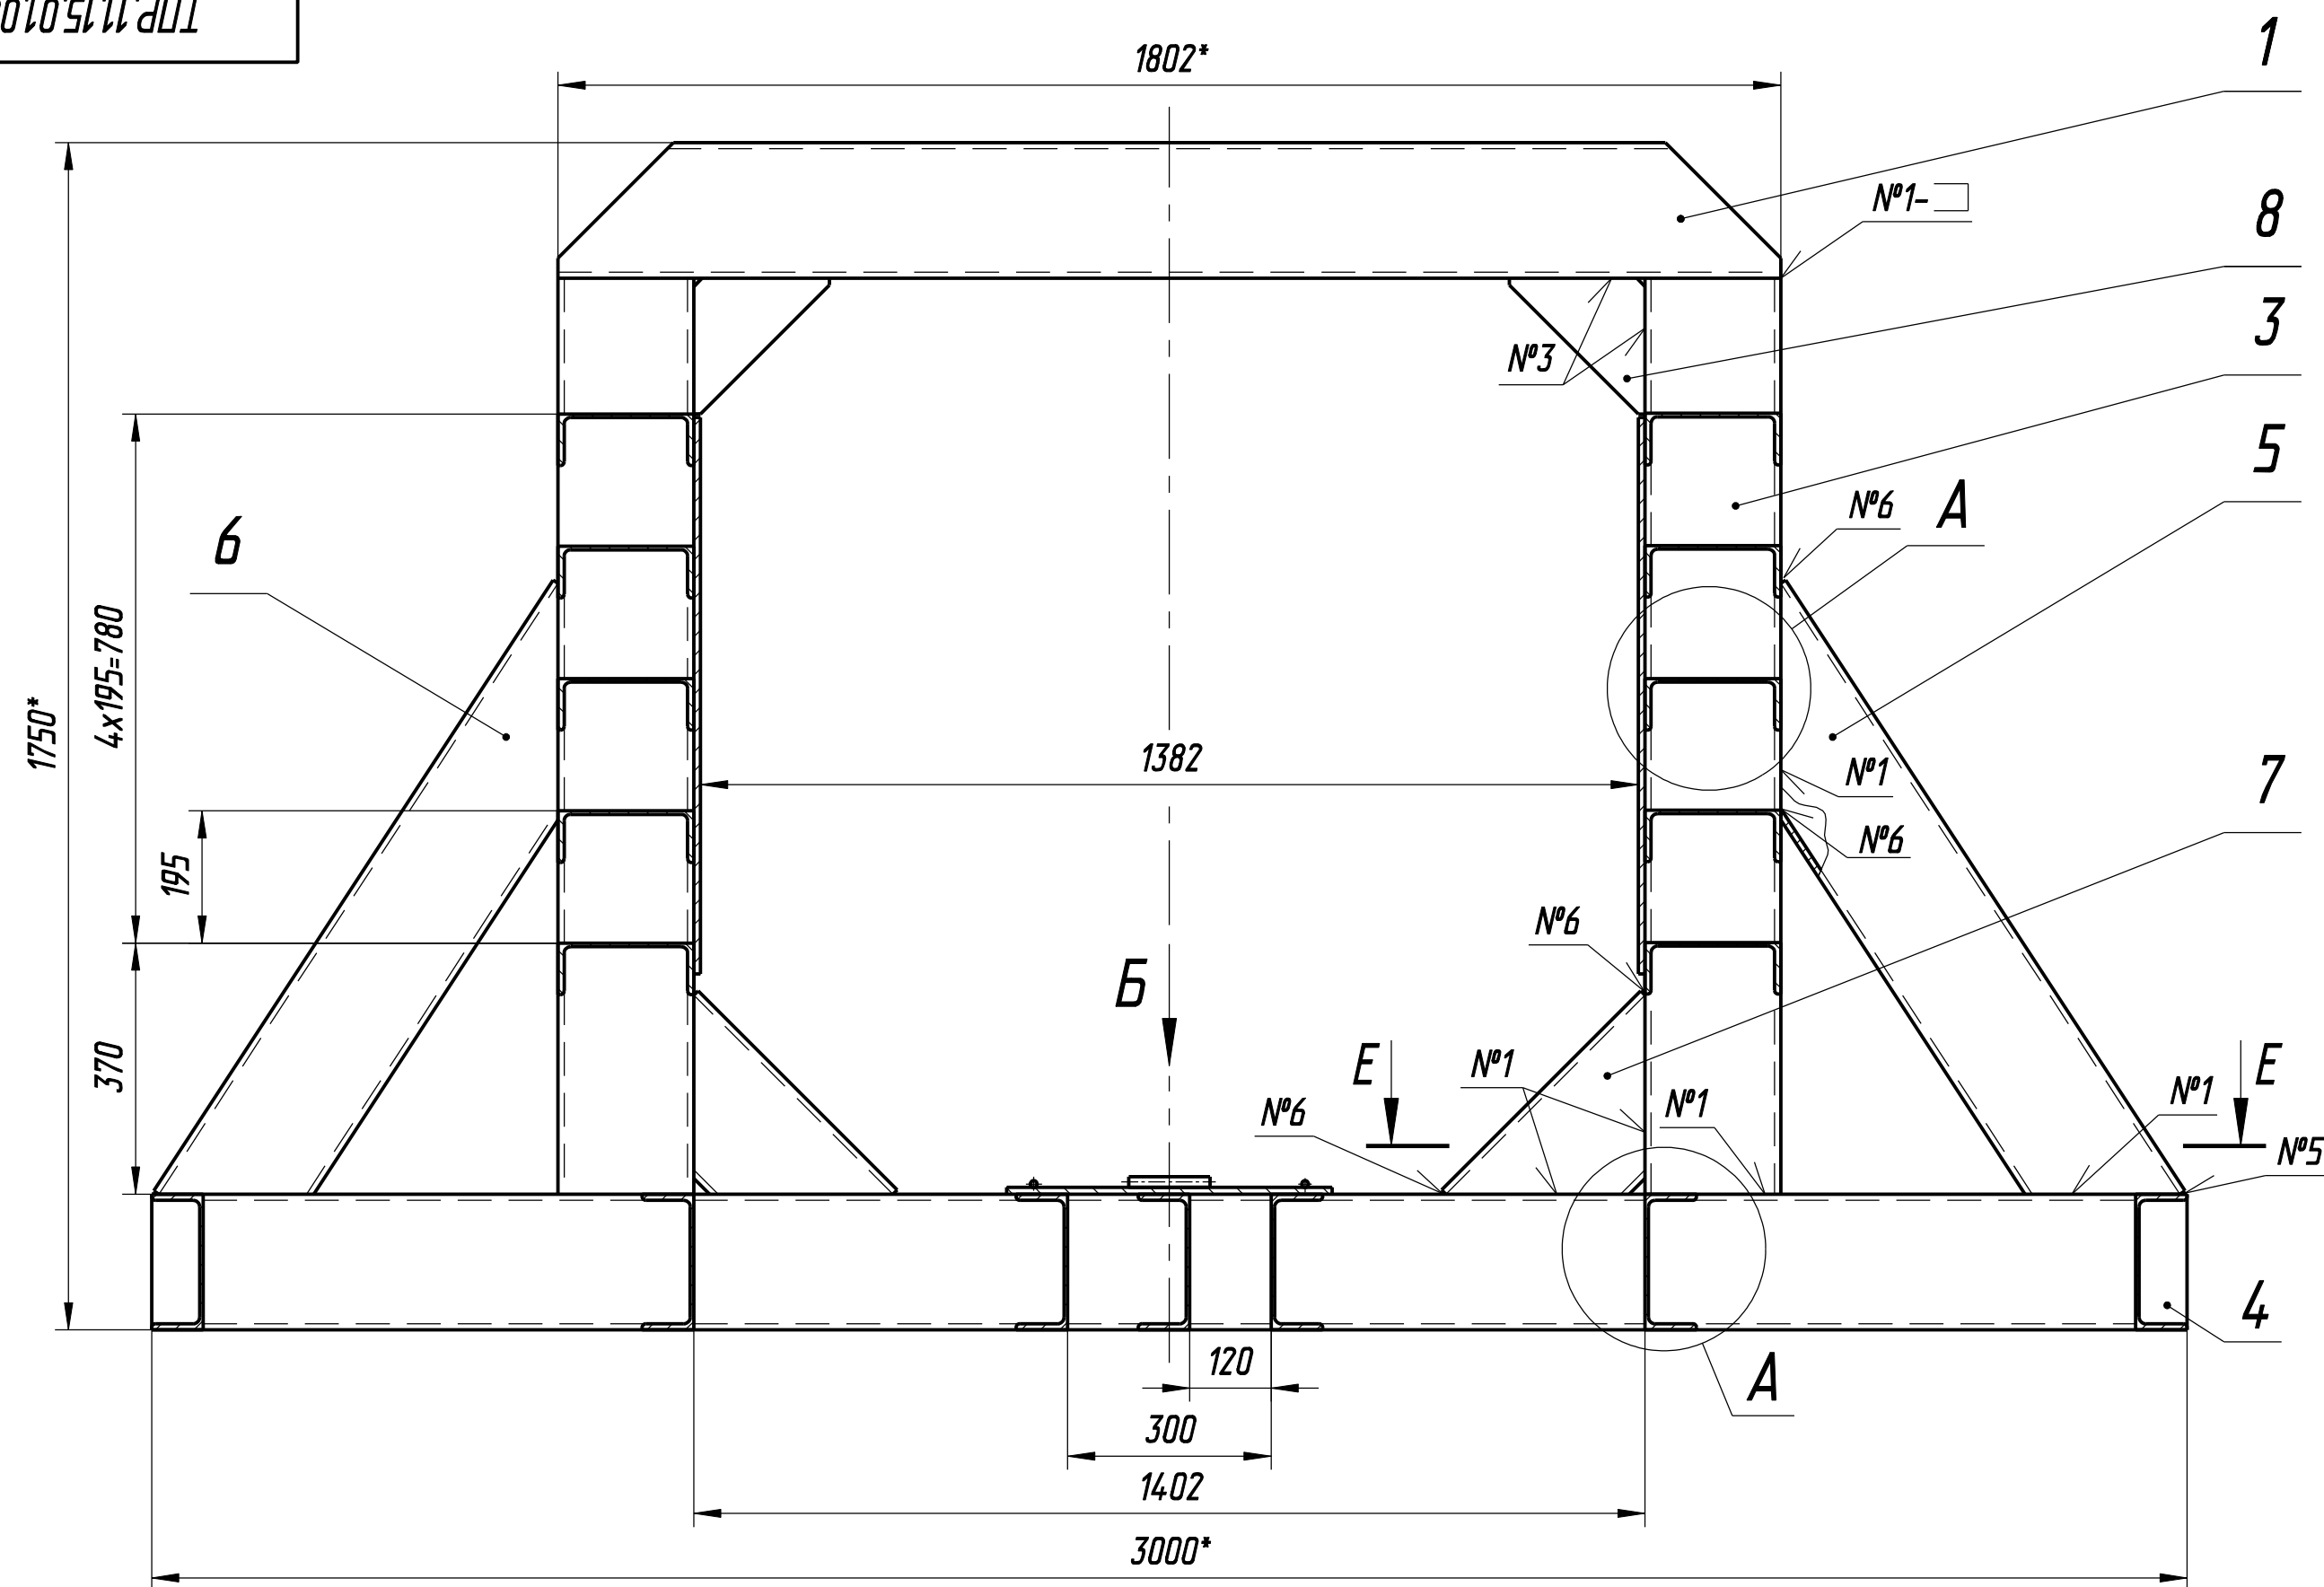


А (1:4)

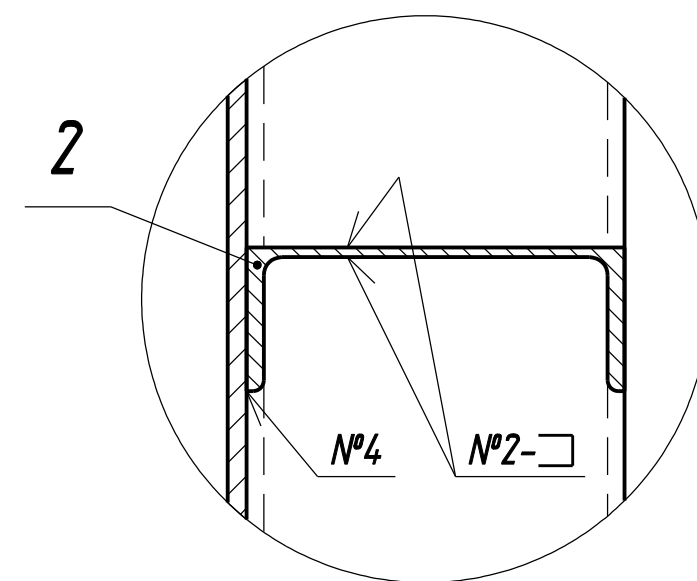


Номер шва	Условное обозначение шва
1	ГОСТ 14771-76-У4-УП
2	-Т1-УП-Δ 6 ^{+2.0} _{-1.0}
3	-Т3-УП-Δ 6 ^{+2.0} _{-1.0}
4	-Н1-УП-Δ 9 ^{+2.0} _{-1.0}
5	ГОСТ 23518-79-У3-УП
6	-Т2-УП
7	Нестандартный
8	Нестандартный


Б (1:4)

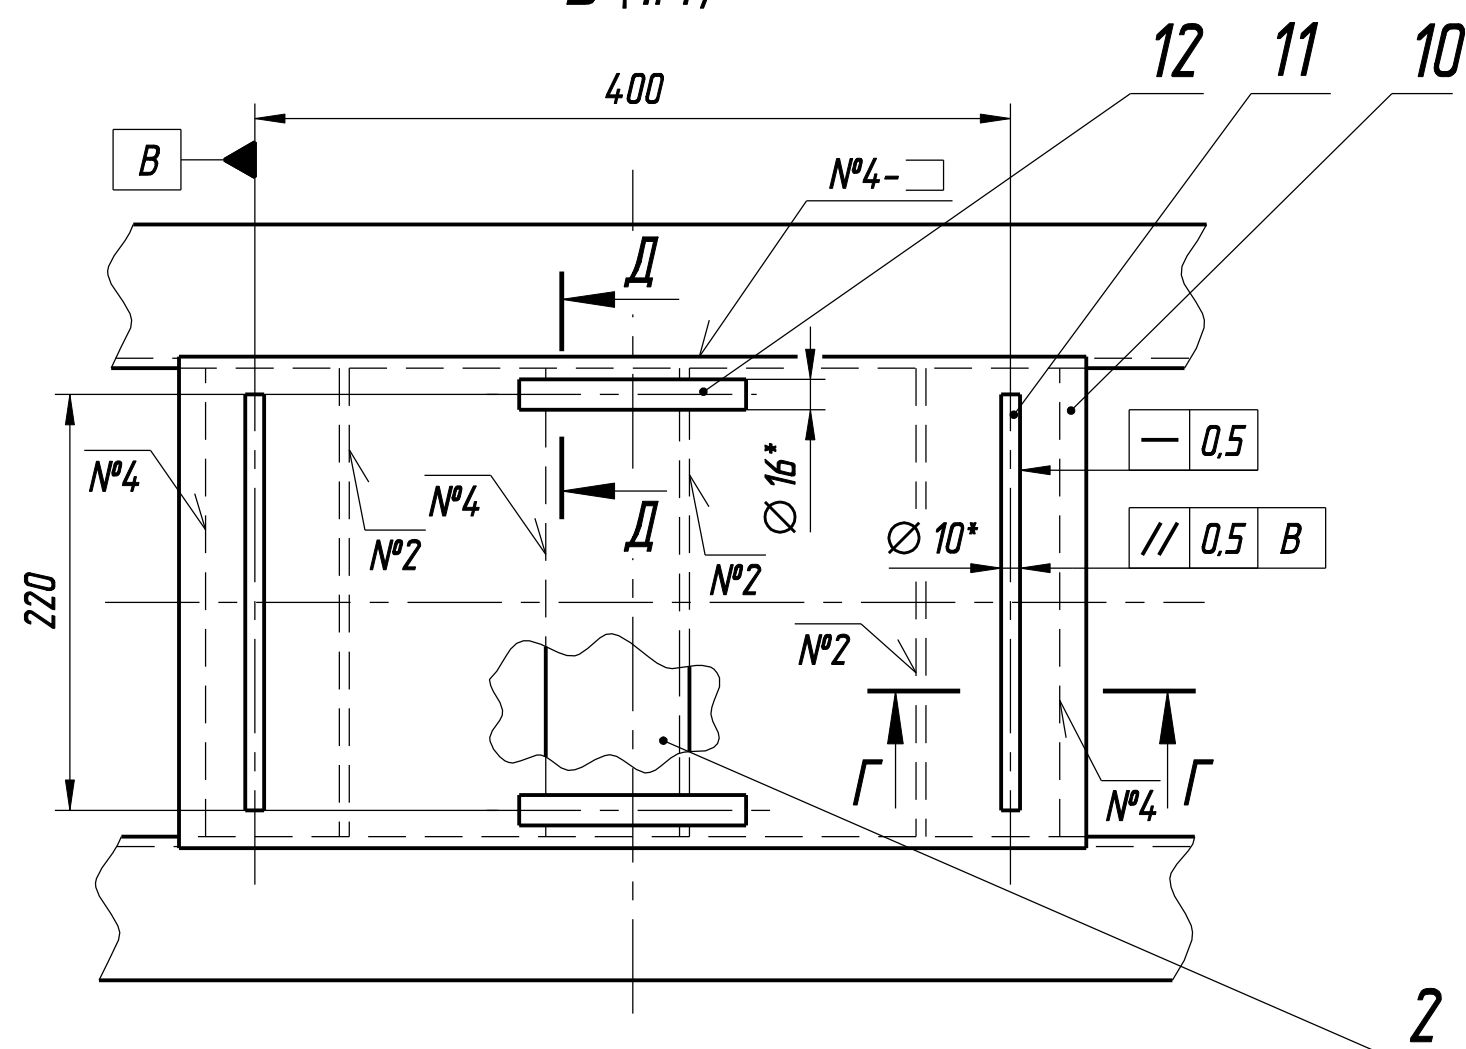


Г-Г (1:1)

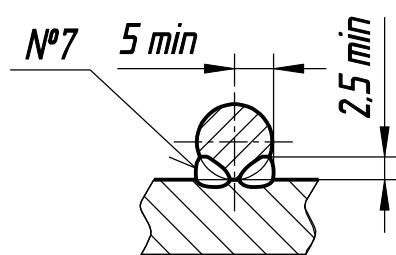

Д-Д (1:1)

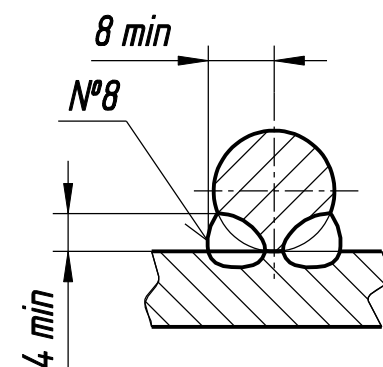

Е-Е

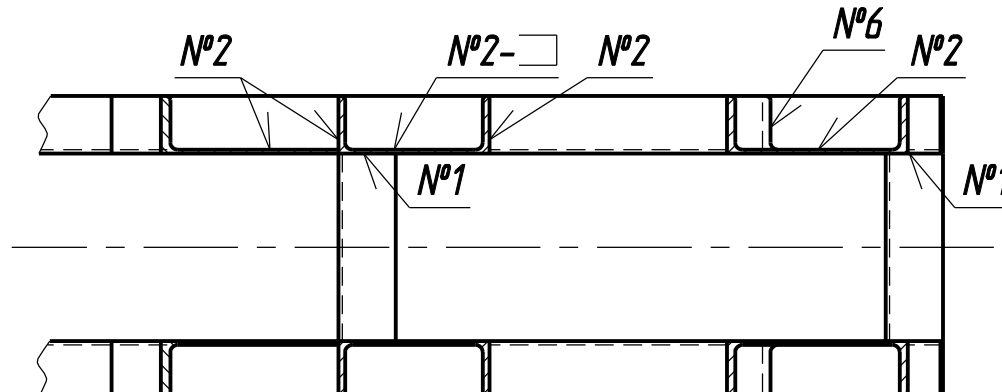

1. *Размеры для справок.

2. Н14, н14, ±IT14/2.

3. Сварочная проволока Св-08Г2С ГОСТ 2246-70.

4. Швы №7, №8 -сварка дуговая в защитном газе.

5. Шерох. обраб. поверхн. дет. БЧ - √Ra 20, √(✓).

6. Покрытие: грунтовка АК-070 ГОСТ 25718-83 в один слой, эмаль ХВ-16 ТУ 6-10-1301-83 в два слоя.

Допускаются другие виды антикоррозионного покрытия согласно проекту.

ТПР.11.15.01.000СБ

					ТПР.11.15.01.000СБ			
					Каркас Сборочный чертеж	Лит.	Масса	Масштаб
Изм.	Лист	№ докум.	Подп.	Дата				
Разраб.		Грушин		07.11			505	1: 10
Пров.		Воронков		07.11				
Т. контр.						Лист	Листов 1	
Н. контр.		Воронков		07.11		ОАО "ГИПРОТЮМЕННЕФТЕГАЗ"		
Утв.								