



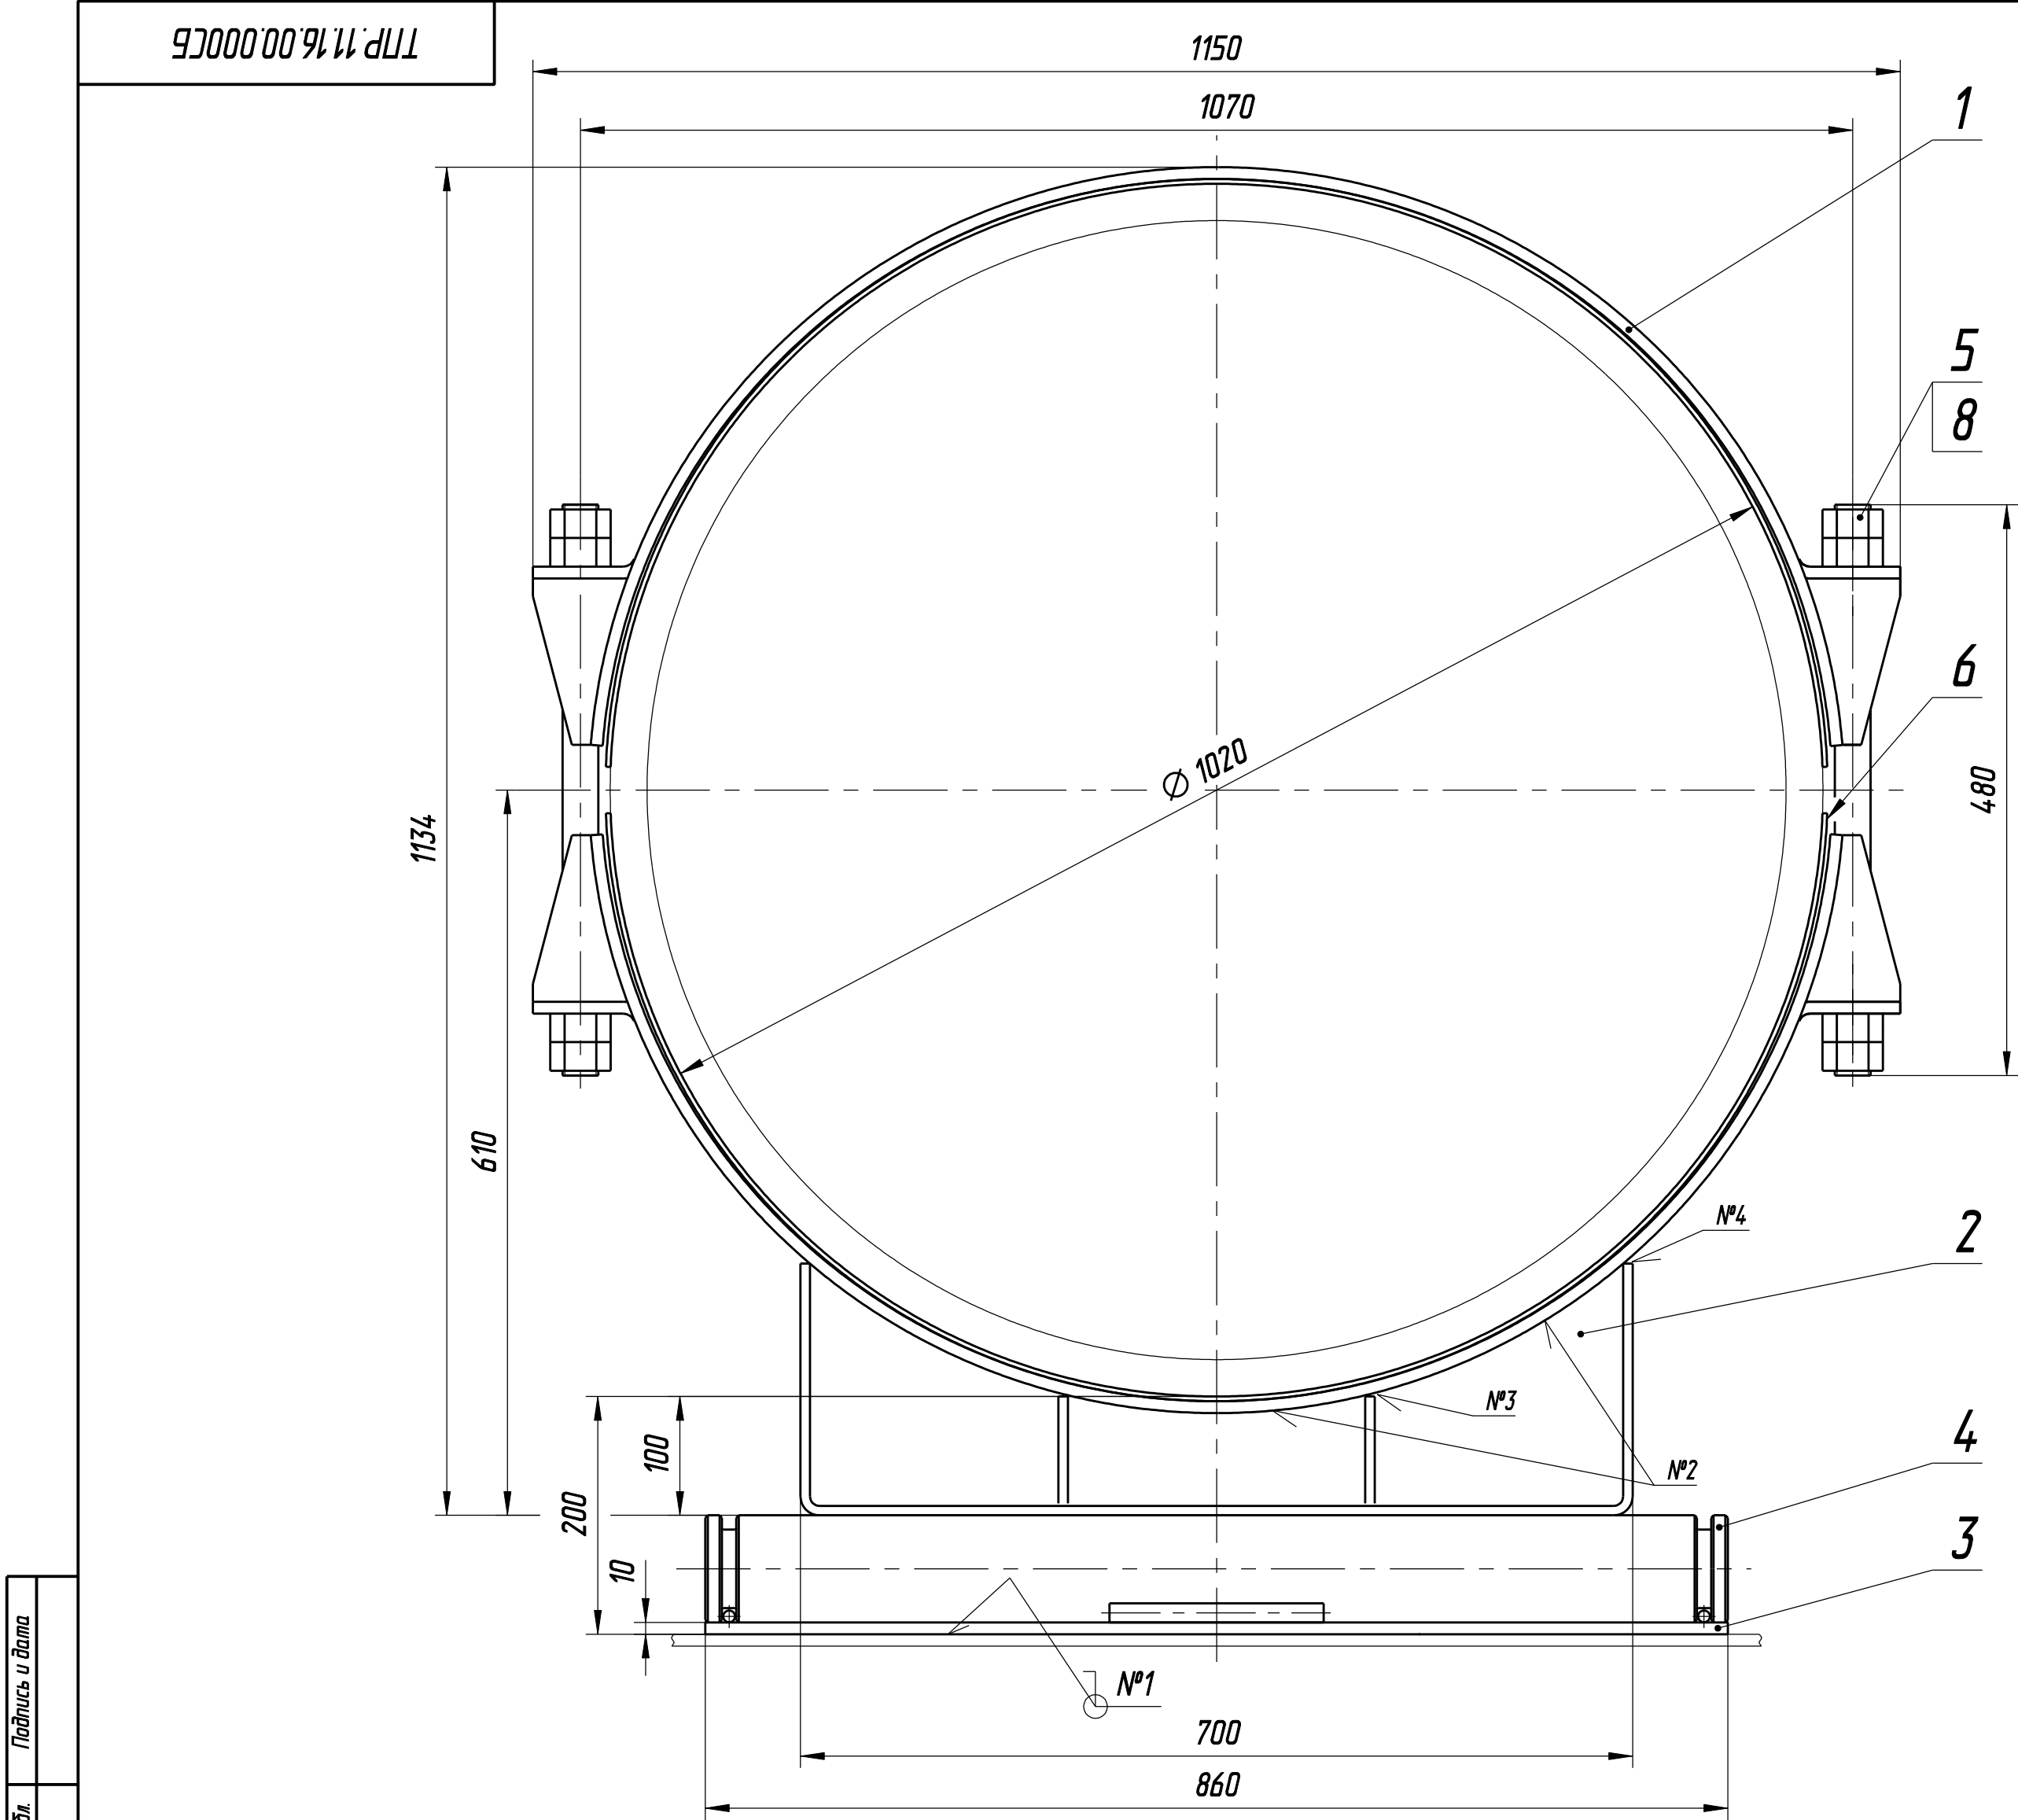

Номер шва	Условное обозначение шва
1	ГОСТ 5264-80-Н1- $\nabla 8^{+2.0}_{-1.0}$
2	ГОСТ 14771-76-Т1-УП- $\nabla 8^{+2.0}_{-1.0}$
3	ГОСТ 23518-79-Т2-УП
4	Нестандартный

Технические требования

- Размеры для справок.
- Сварку шва №1 производить электродами типа Э50А ГОСТ 9467-75, остальных швов – проволокой Св-08Г2С ГОСТ 2246-70.
- Покрытие: грунтовка АК-070 ГОСТ 25718-83 в один слой; эмаль ХВ-16 ТУ 6-10-1301-83 в два слоя.
Допускаются другие виды антикоррозионного покрытия согласно проекту.
- Маркировать любым способом, обеспечивающим сохранность маркировки на весь срок эксплуатации, шрифтом не менее 5: обозначение по чертежу и товарный знак завода-изготовителя.

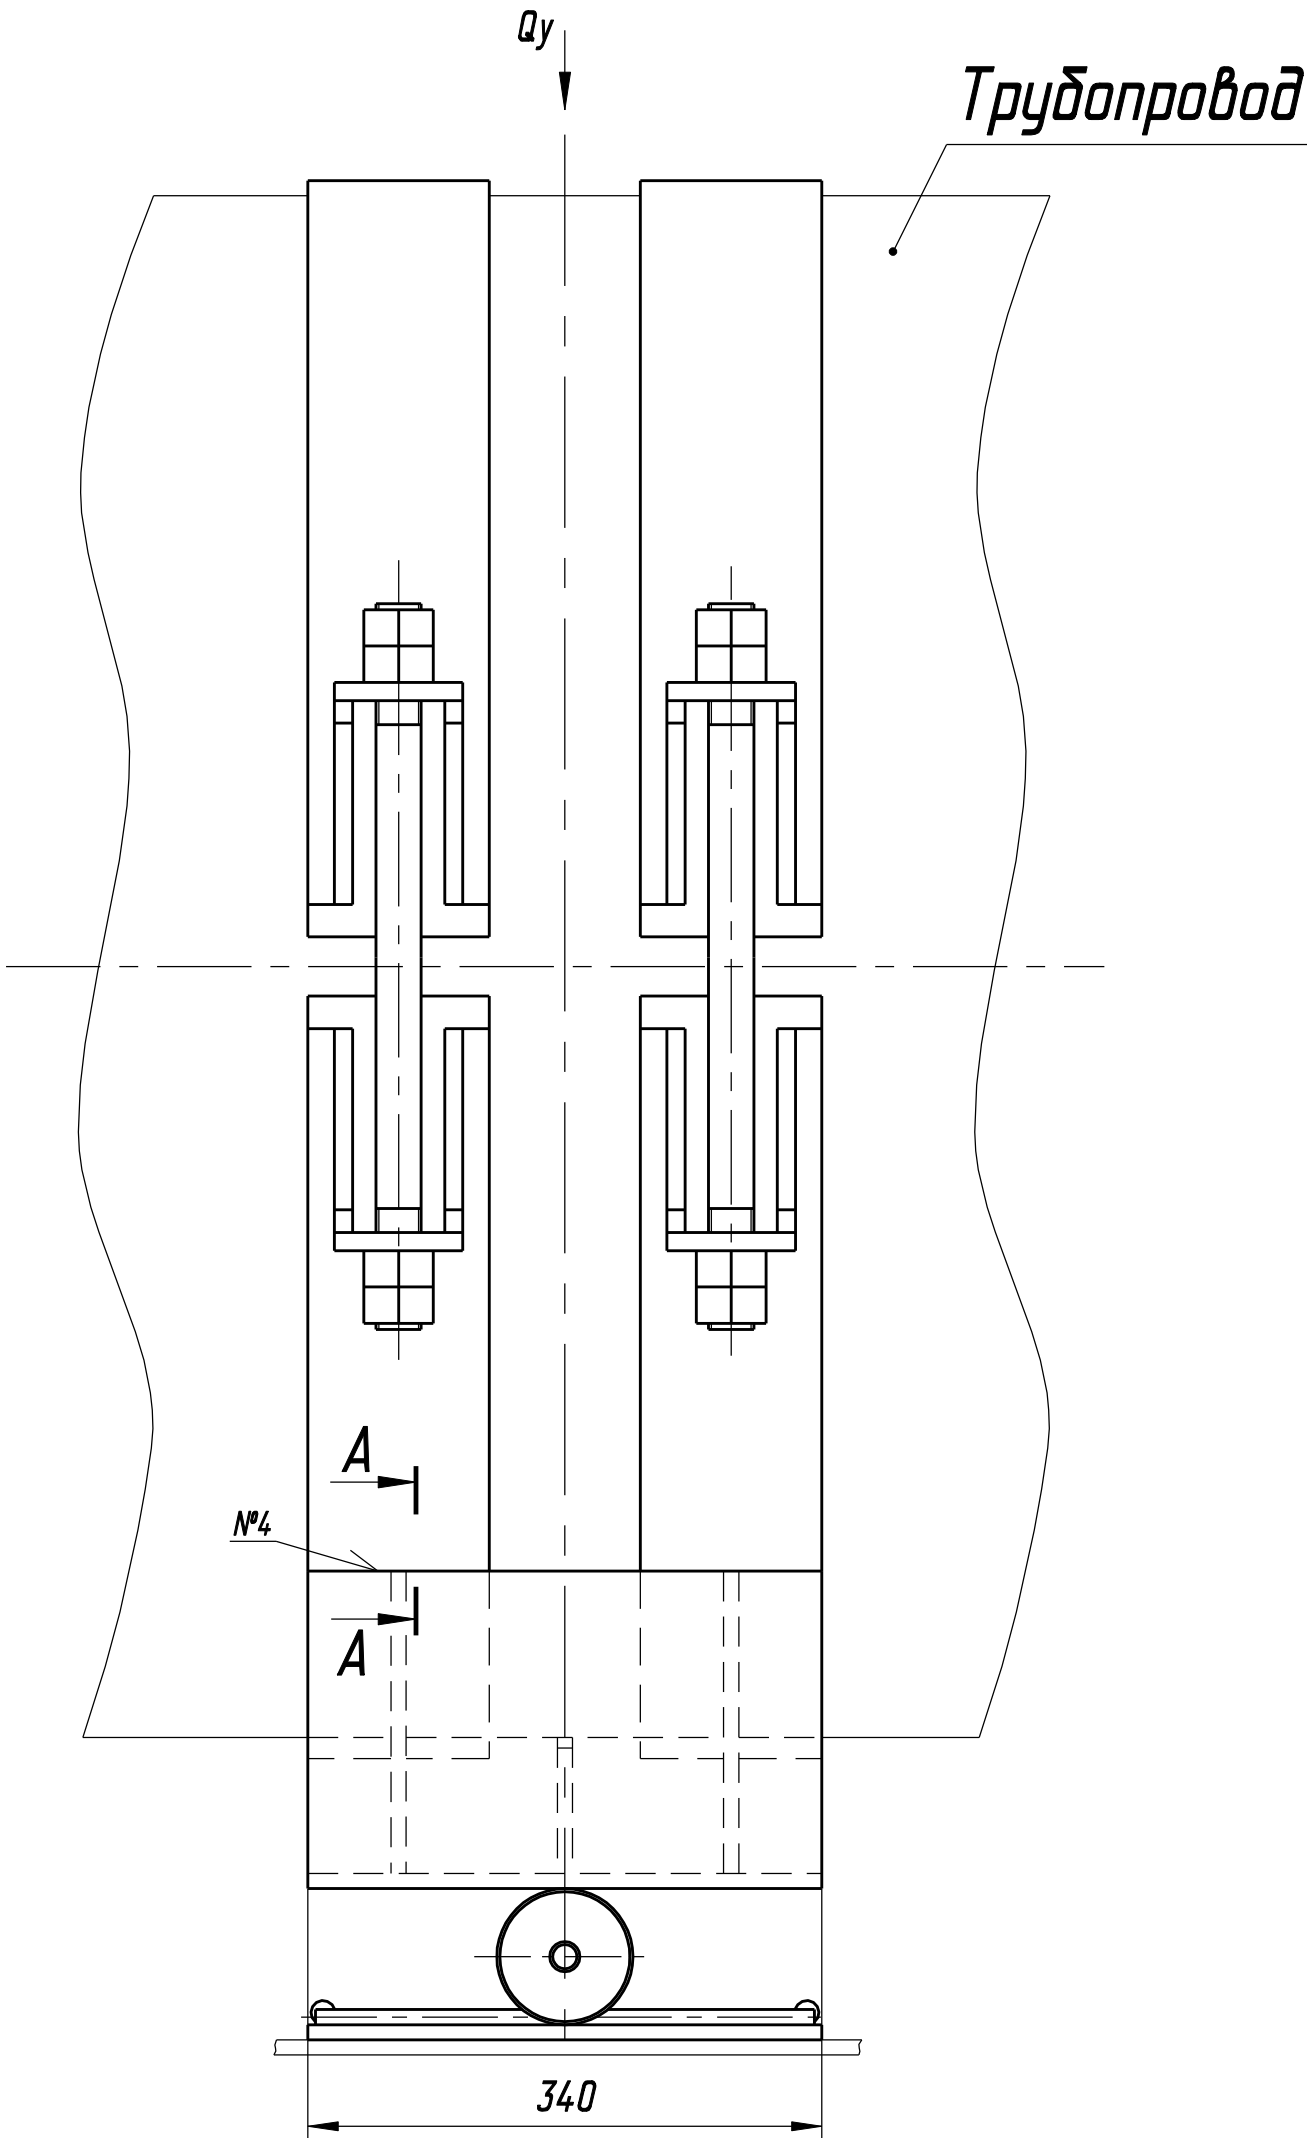

Техническая характеристика

- Опора однокатковая предназначена для крепления труб из углеродистой и низколегированной стали при строительстве технологических трубопроводов с наружным диаметром 1020 мм транспортирующих вещества с температурой от минус 20 до 200 °С и условным давлением P_u до 16 МПа при температуре окружающей среды до минус 70 °С.
- Наибольшая вертикальная нагрузка на опору Q_y – 200 кН (20000 кгс).
- Перемещение вдоль оси трубы не более 240 мм.

					ТПР.11.16.00.000СБ						
					Опора однокатковая для трубопровода Дн 1020мм, Ру 16 МПа Сборочный чертеж			Лит.	Масса	Масштаб	
Изм.	Лист	№ докум.	Подп.	Дата						193	1:5
Разраб.	Воронков			08.11							
Пров.											
Т. контр.						Лист		Листов 1			
Н. контр.	Воронков			08.11		ОАО "ТИПРОТЮМЕННЕФТЕГАЗ"					
Утв.	Бояркин			08.11							